




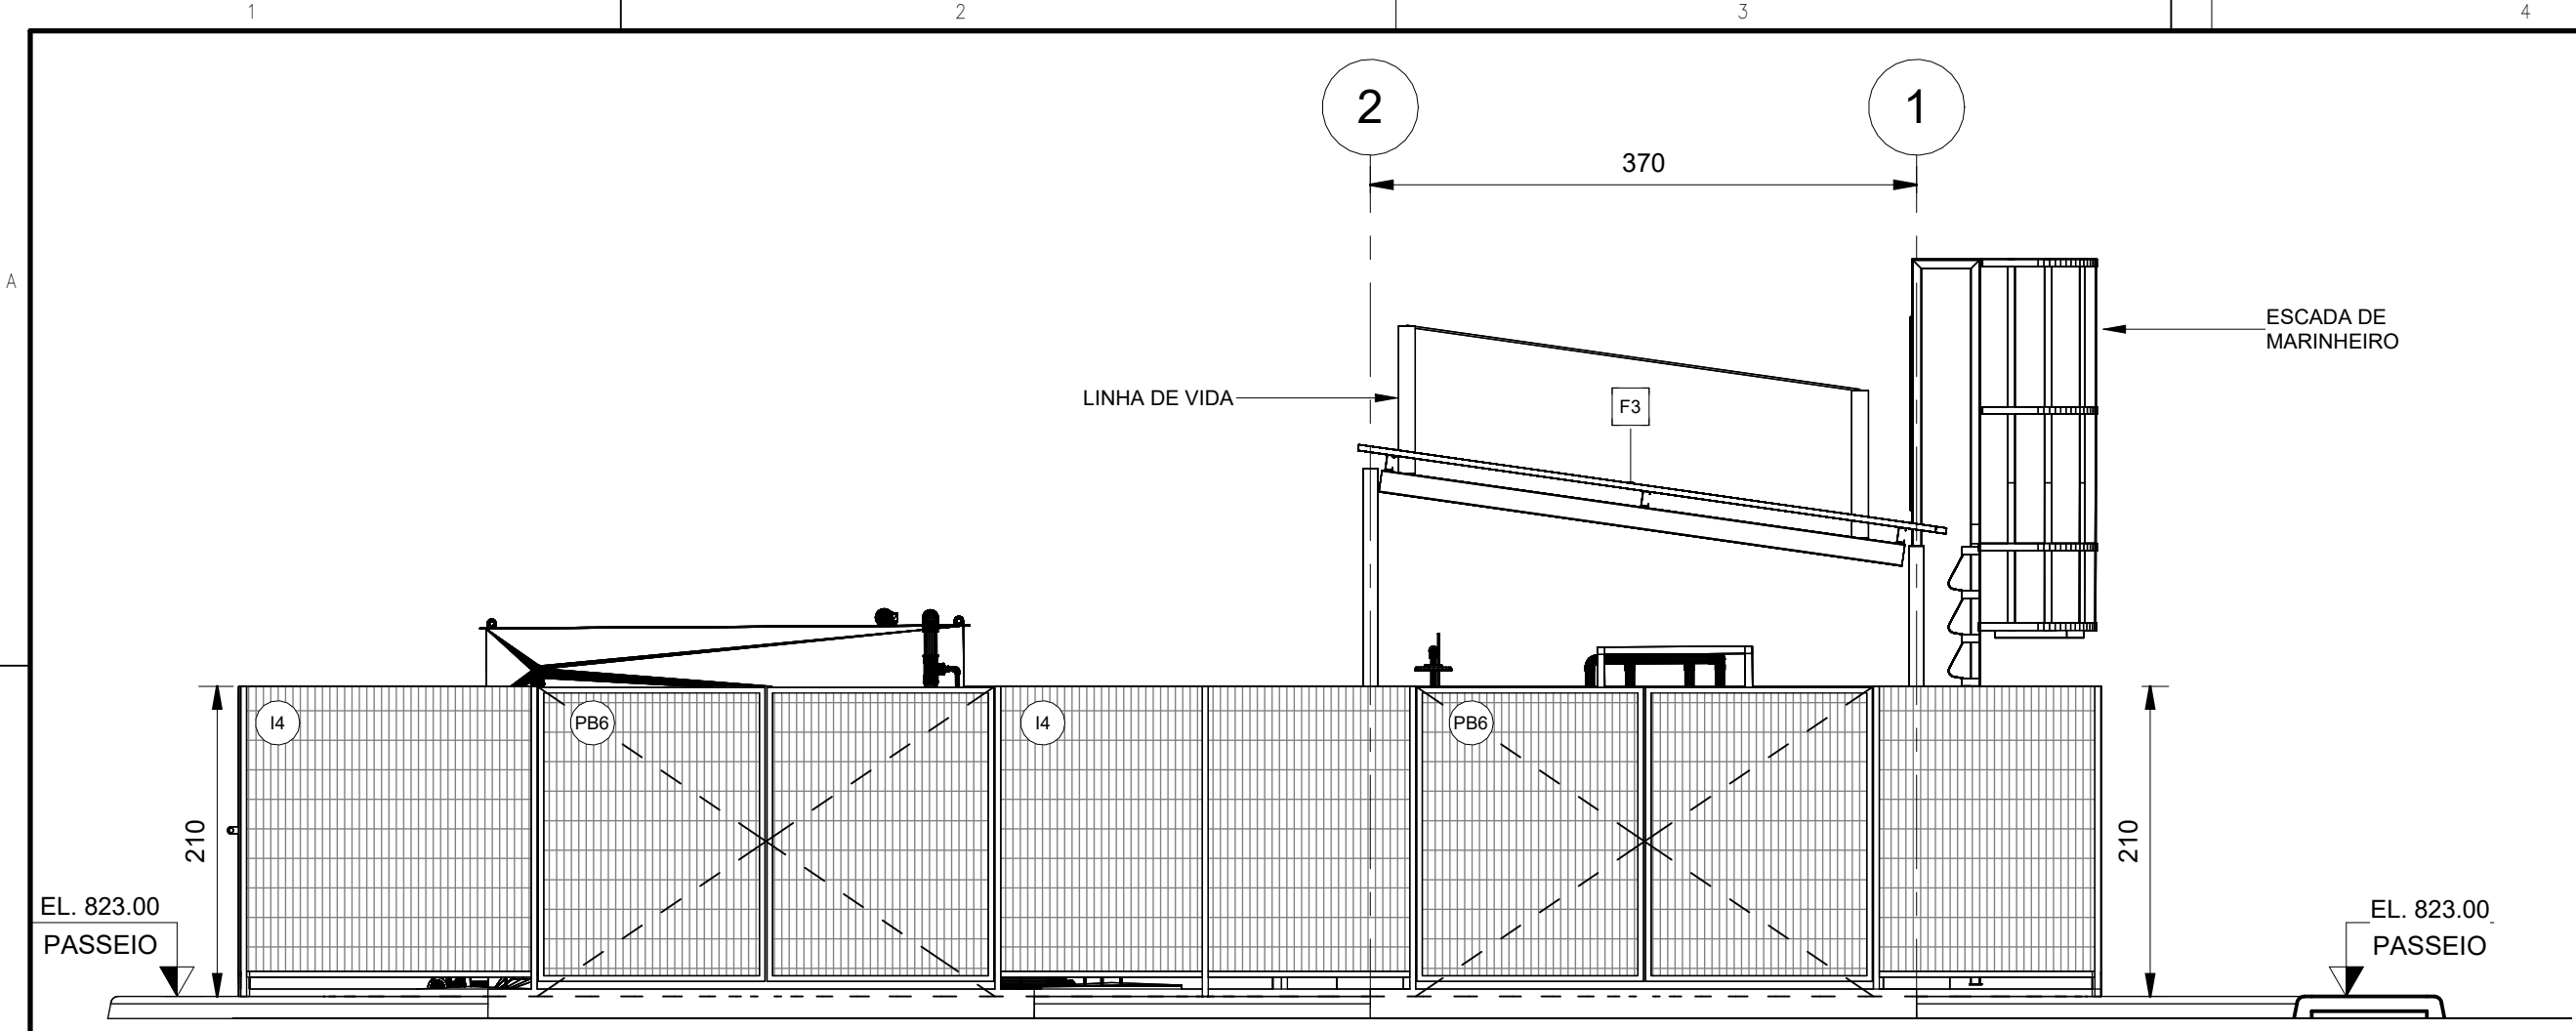


FACHADA 1
1 : 50

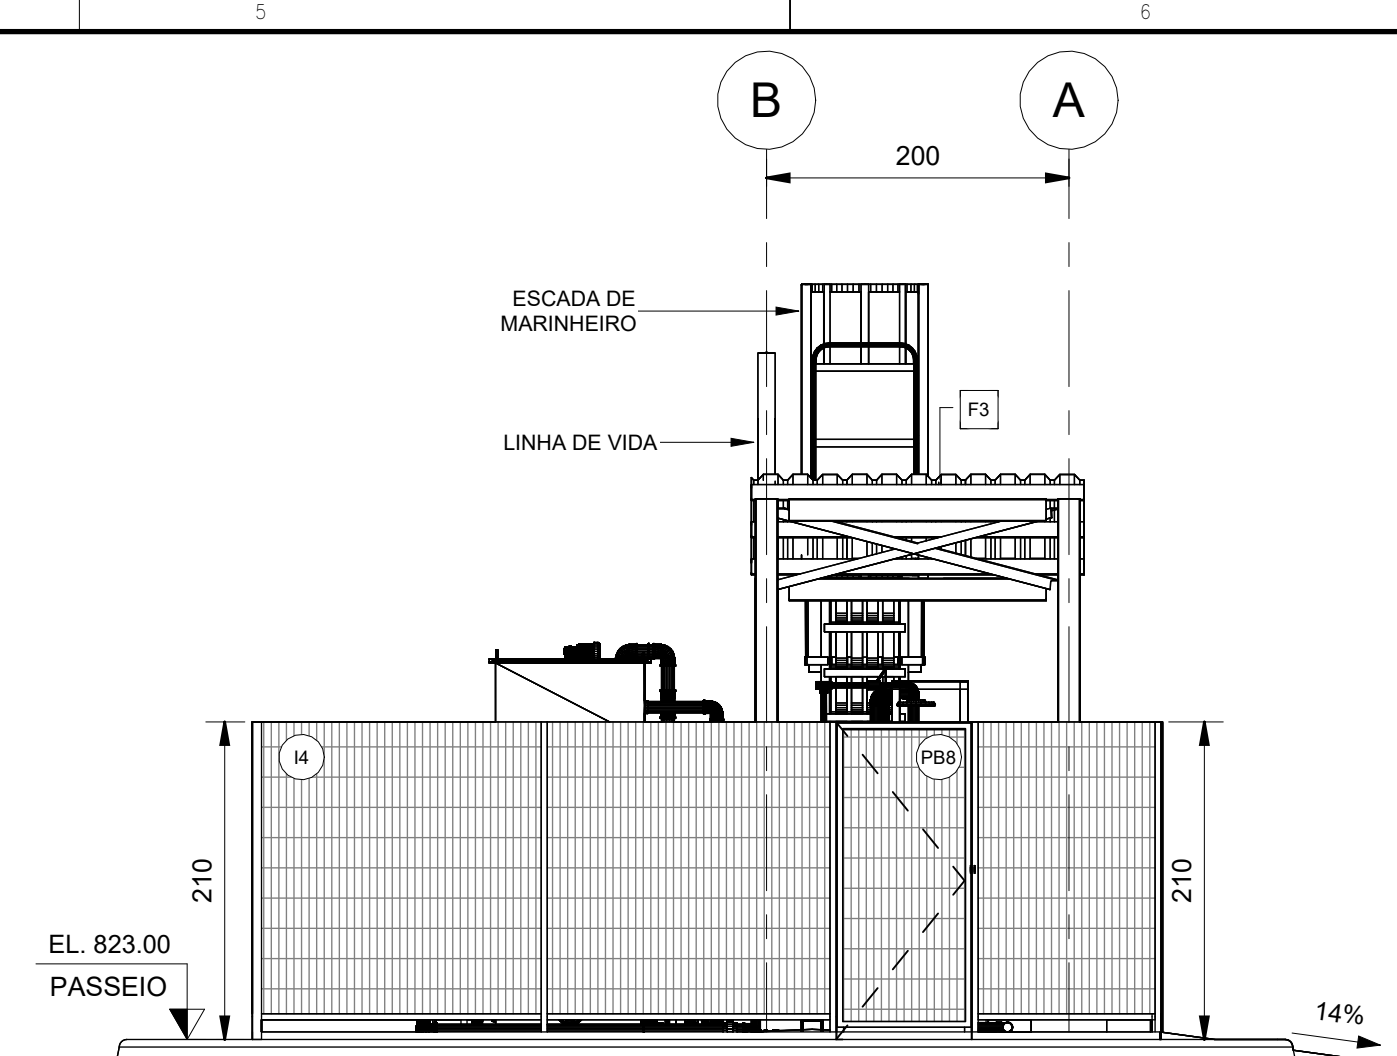


FACHADA 2
1 : 50

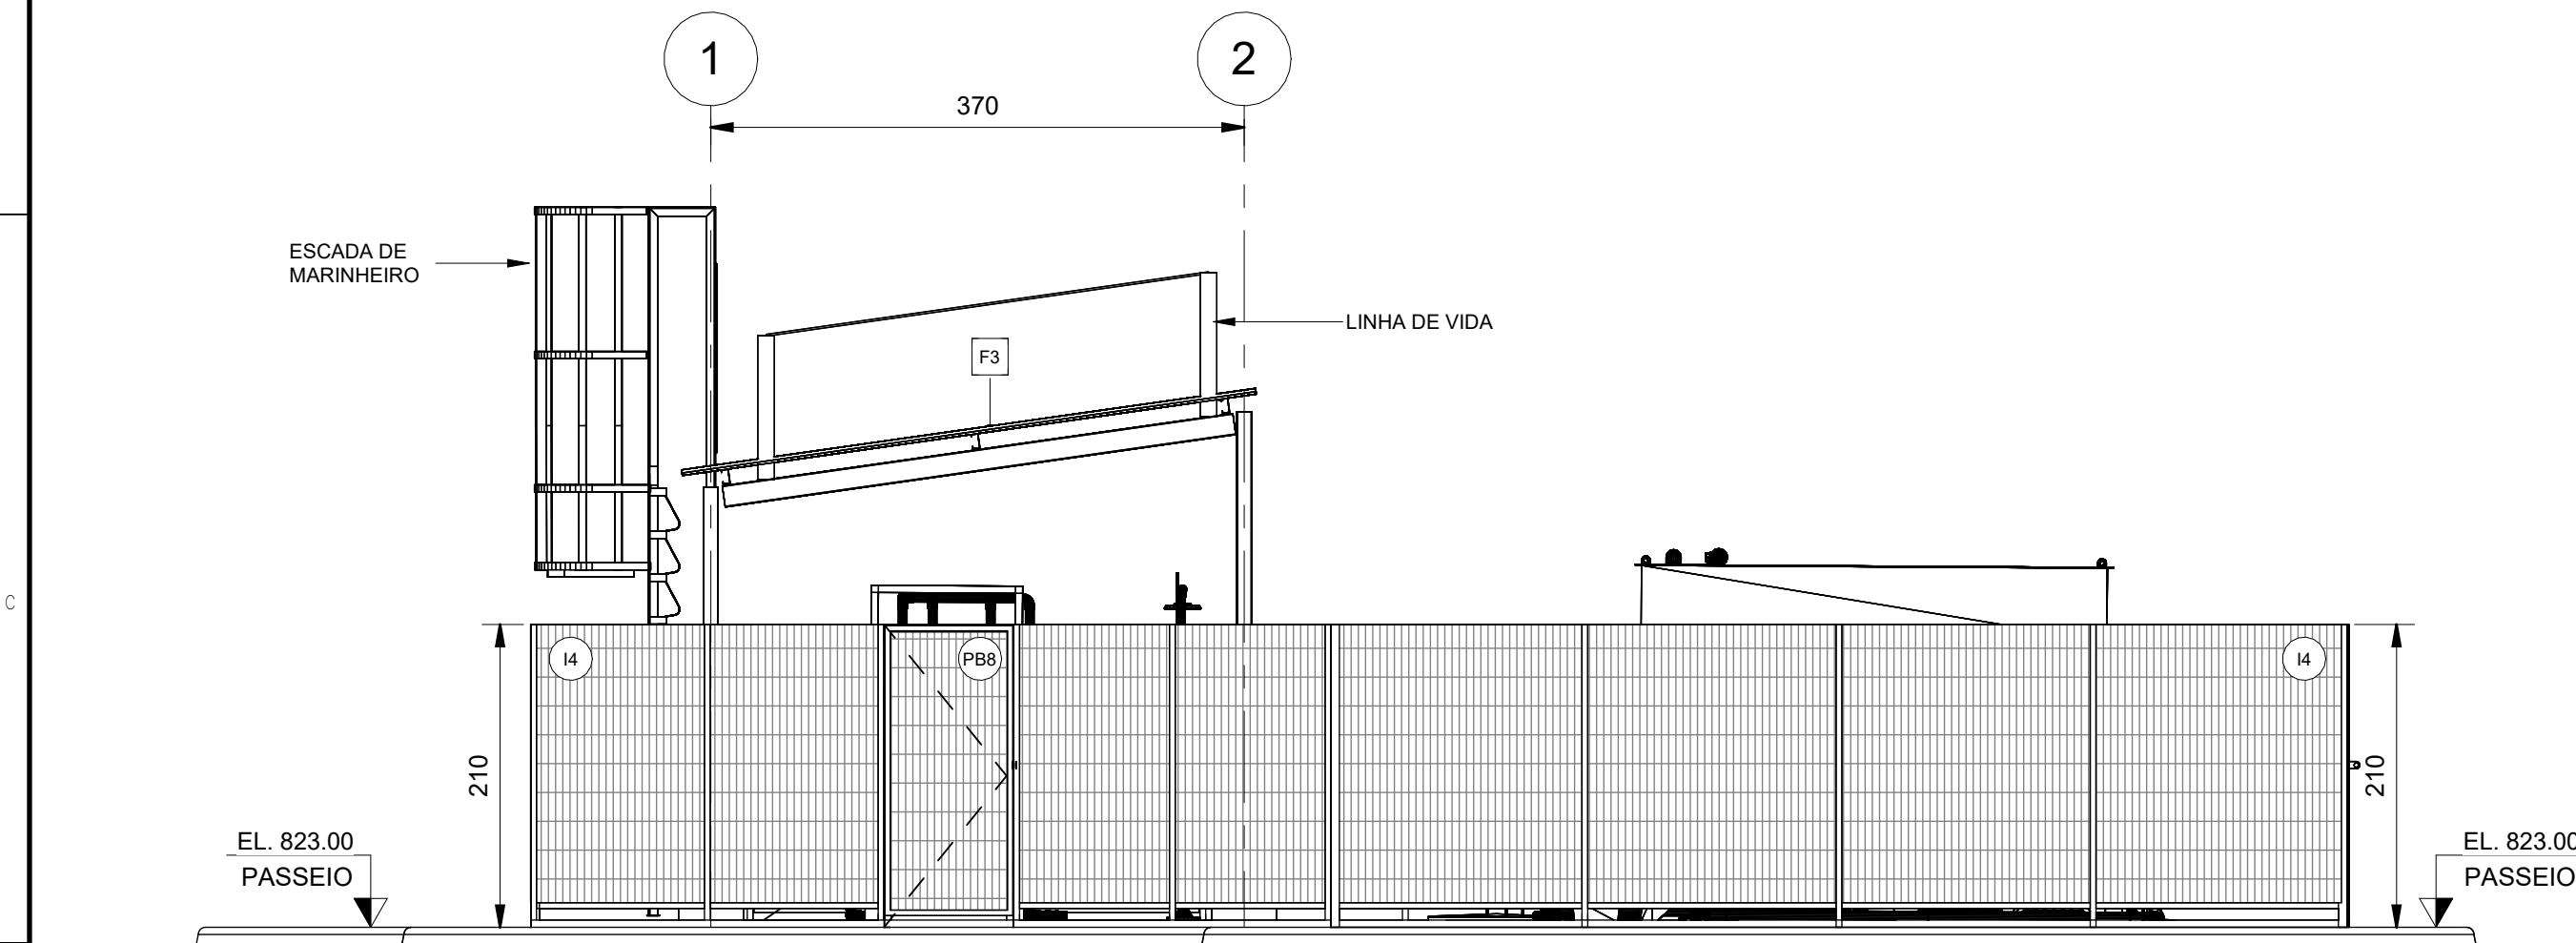


FACHADA 3
1 : 50

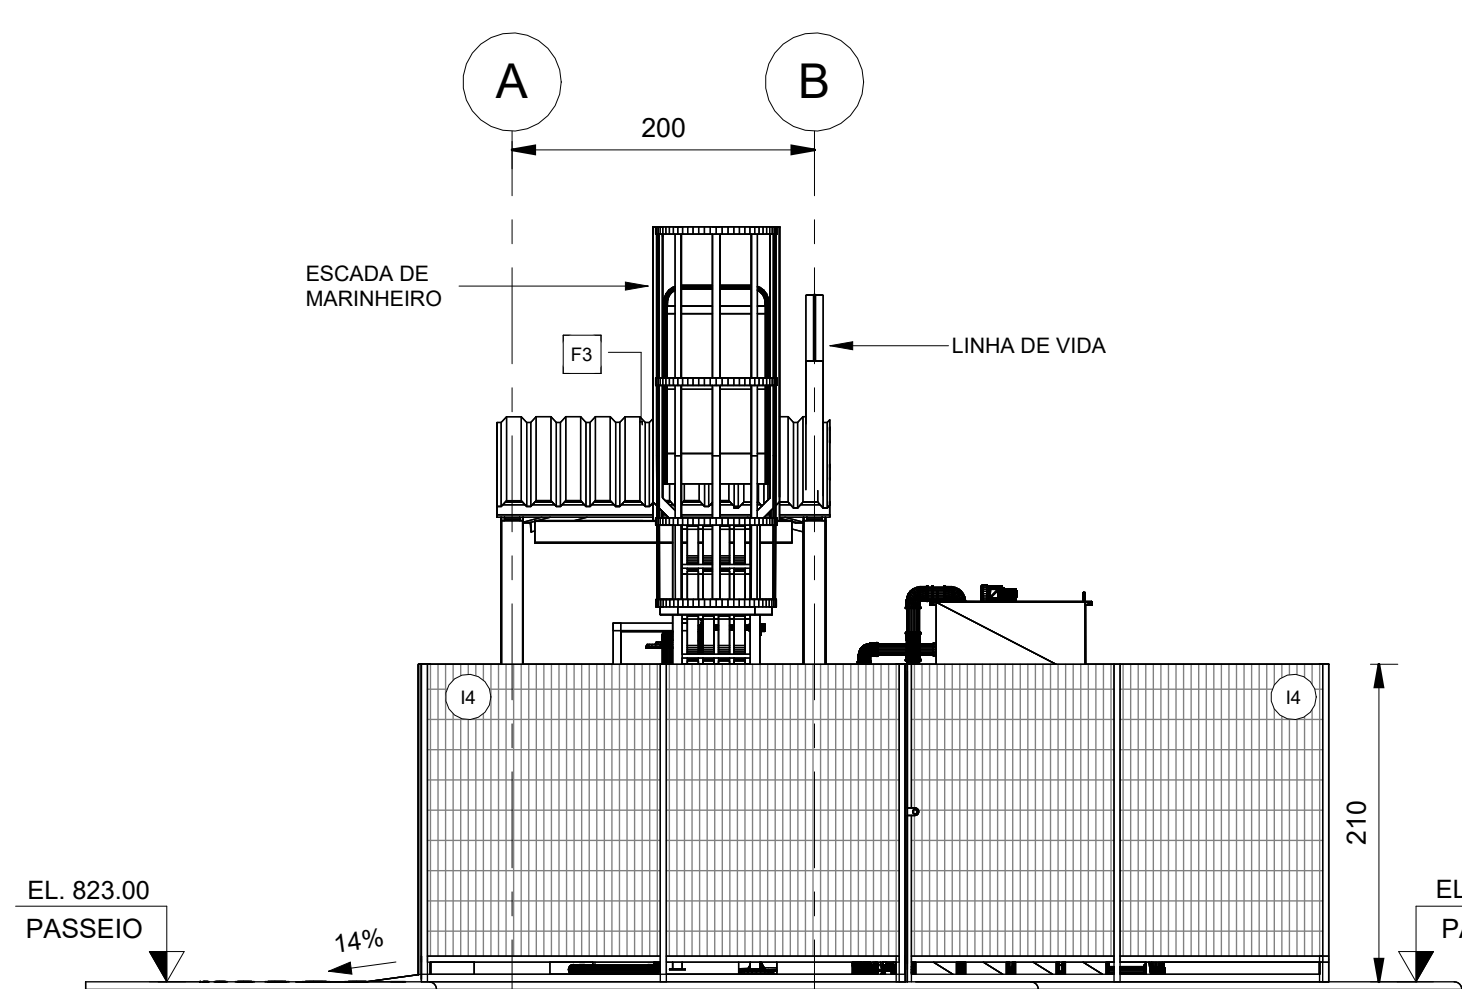


FACHADA 4
1 : 50

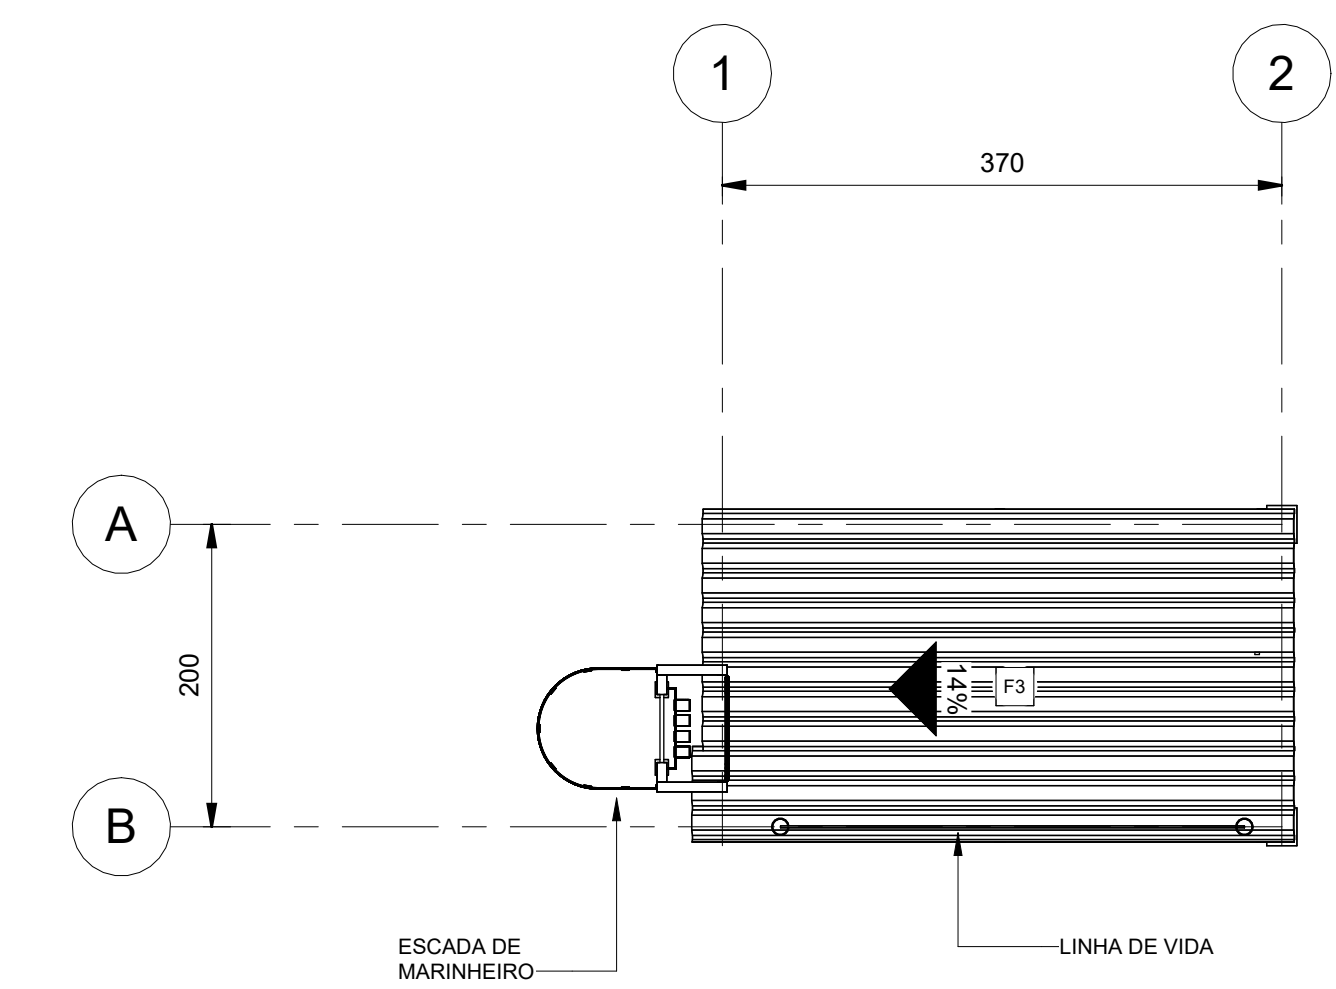

PLANTA DE COBERTURA
1 : 50

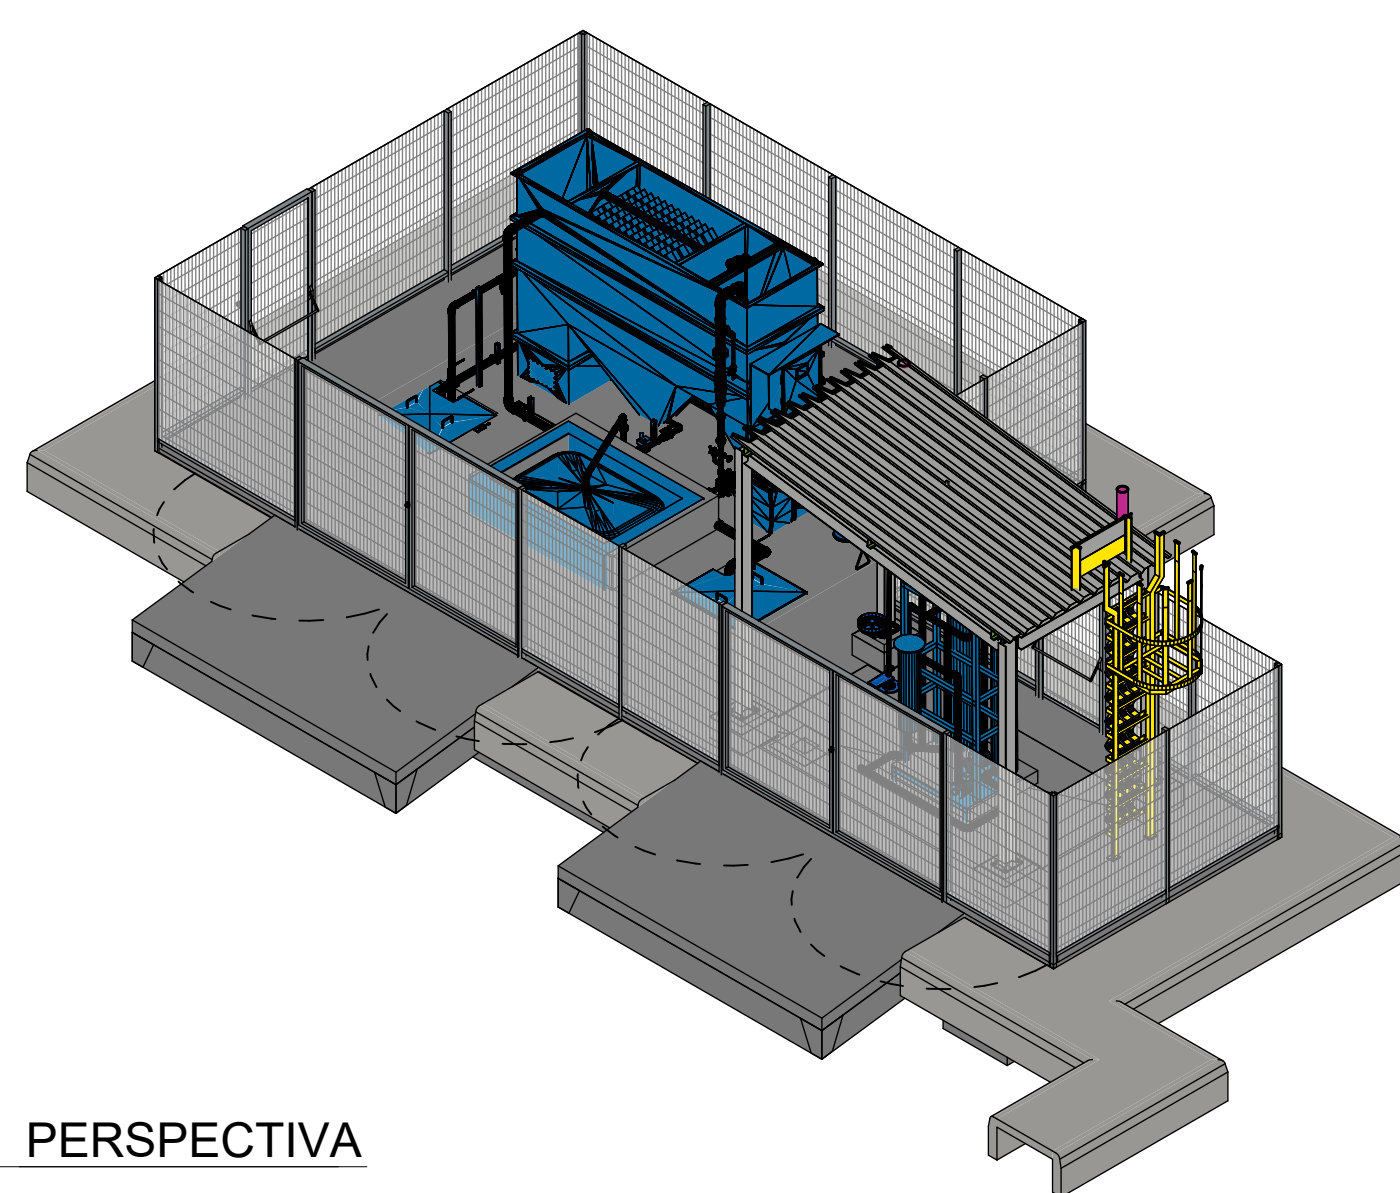


PERSPECTIVA

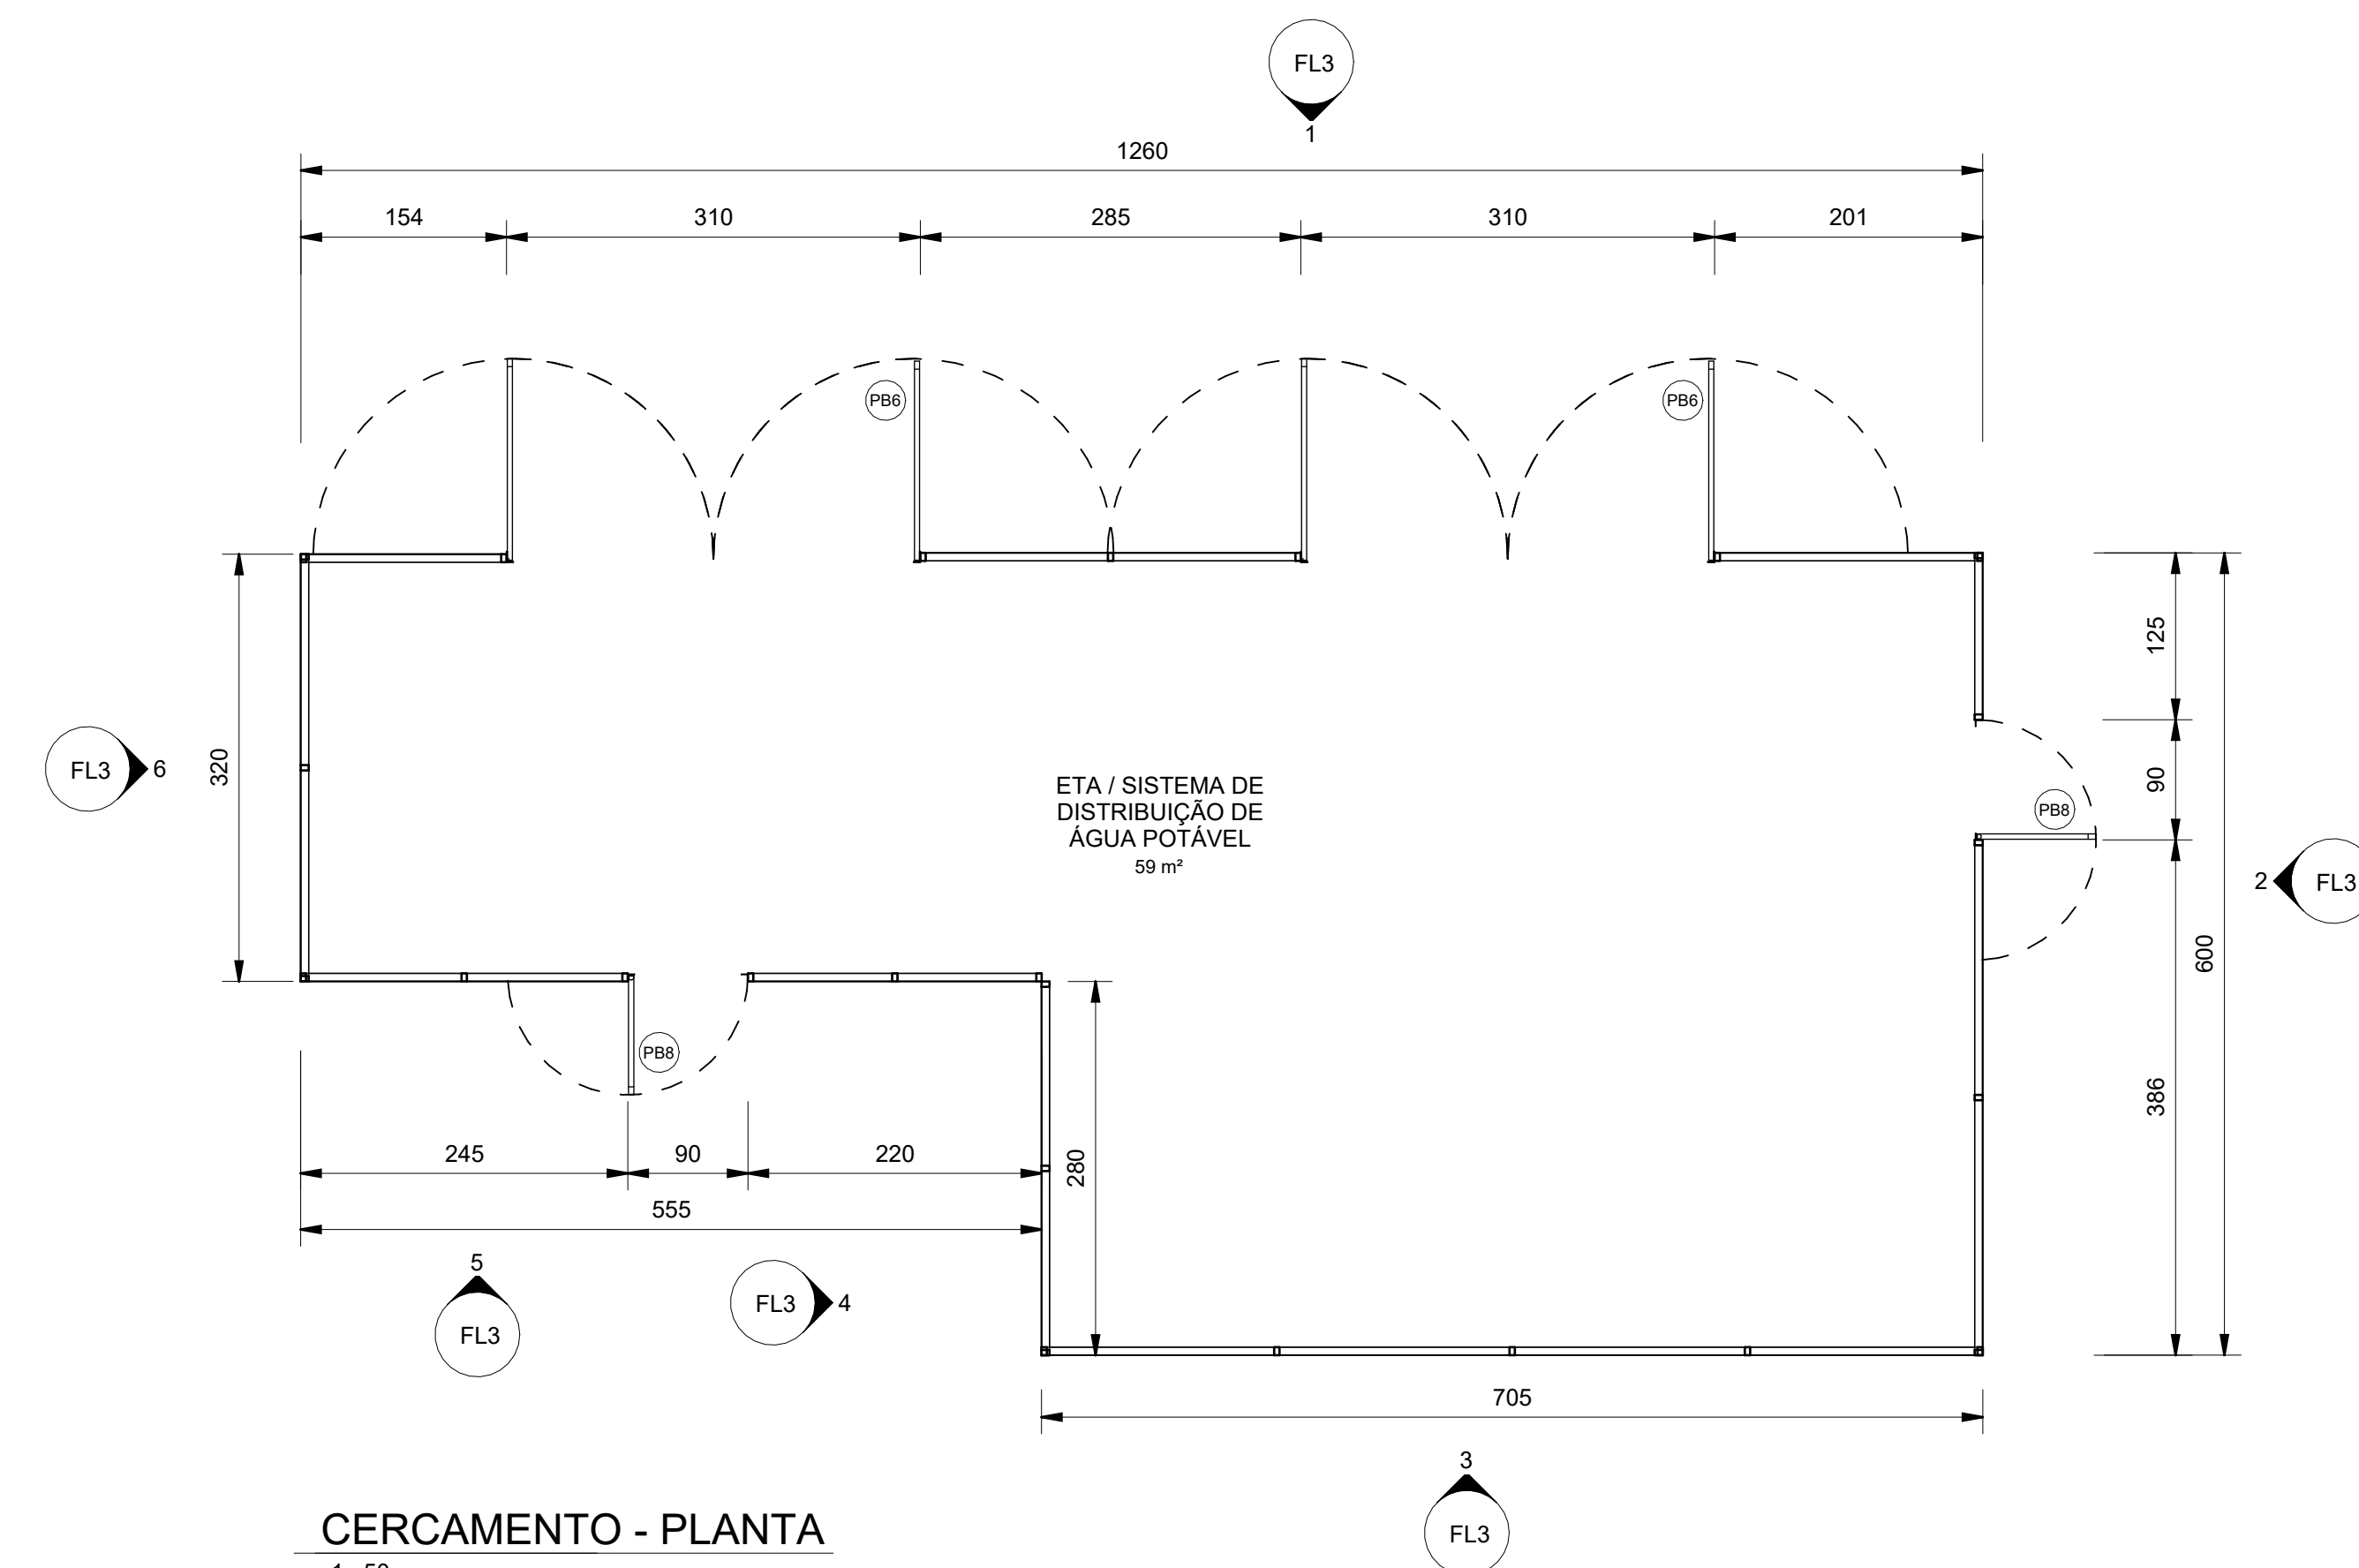

CERCAMENTO - PLANTA
1 : 50

QUADRO DE ESQUADRIAS				
CÓD.	LARGURA (cm)	ALTURA (cm)	DESCRIÇÃO	QTD.
QUADRO DE ESQUADRIAS - PORTAS				
PB6	300.00	210.00	PORTÃO DE GIRO, 2 FOLHAS, EM PAINEL PRÉ-FABRICADO DE TELA COMPOSTO POR POSTES TUBULARES DE SEÇÃO 40x60mm E TELA EM MALHA DE 50x200mm, DIÂMETRO DE 5mm, PRÉ-PINTADO EM PINTURA ELESTROSTÁTICA COR VERDE (RAL 6005), REF.: BELGO BEKAERT, LINHA NYLOFOR OU SIMILAR	2
PB8	90.00	210.00	PORTÃO DE GIRO, 1 FOLHA, EM PAINEL PRÉ-FABRICADO DE TELA COMPOSTO POR POSTES TUBULARES DE SEÇÃO 40x60mm E TELA EM MALHA DE 50x200mm, DIÂMETRO DE 5mm, PRÉ-PINTADO EM PINTURA ELESTROSTÁTICA COR VERDE (RAL 6005), REF.: BELGO BEKAERT, LINHA NYLOFOR OU SIMILAR	2
QUADRO ESPECIFICAÇÕES DE ACABAMENTOS				
CÓDIGO	DESCRIÇÃO			
○	PISOS			
A1	PISO EM CONCRETO DESEMPENADO COM JUNTA SECA A CADA 1,20cm, ACABAMENTO VASSOURADO, ESP. 10cm			
A6	PISO EM CONCRETO ARMADO, VER PROJETO DE CIVIL/CONCRETO			
□	COBERTURAS			
F3	TELHA METÁLICA EM CHAPA DE AÇO GALVALUME TRAPEZOIDAL, H=40mm, ESPESURA=65mm, ACABAMENTO EM PINTURA ESMALTE COR CINZA FACE EXTERNA, FACE INTERNA ACABAMENTO NATURAL, PARA ESPECIFICAÇÕES VER PROJETO DE ESTRUTURAS METÁLICAS			
○	CERCAMENTOS			
I4	CERCAMENTO EM PAINEL PRÉ-FABRICADO DE TELA COMPOSTO POR POSTES TUBULARES DE SEÇÃO 40x60mm E TELA EM MALHA DE 50x200mm, DIÂMETRO DE 5mm, PRÉ-PINTADO EM PINTURA ELESTROSTÁTICA COR VERDE (RAL 6005), MONTANTES APARAFUSADO AO PISO, REF.: BELGO BEKAERT, LINHA NYLOFOR OU SIMILAR			

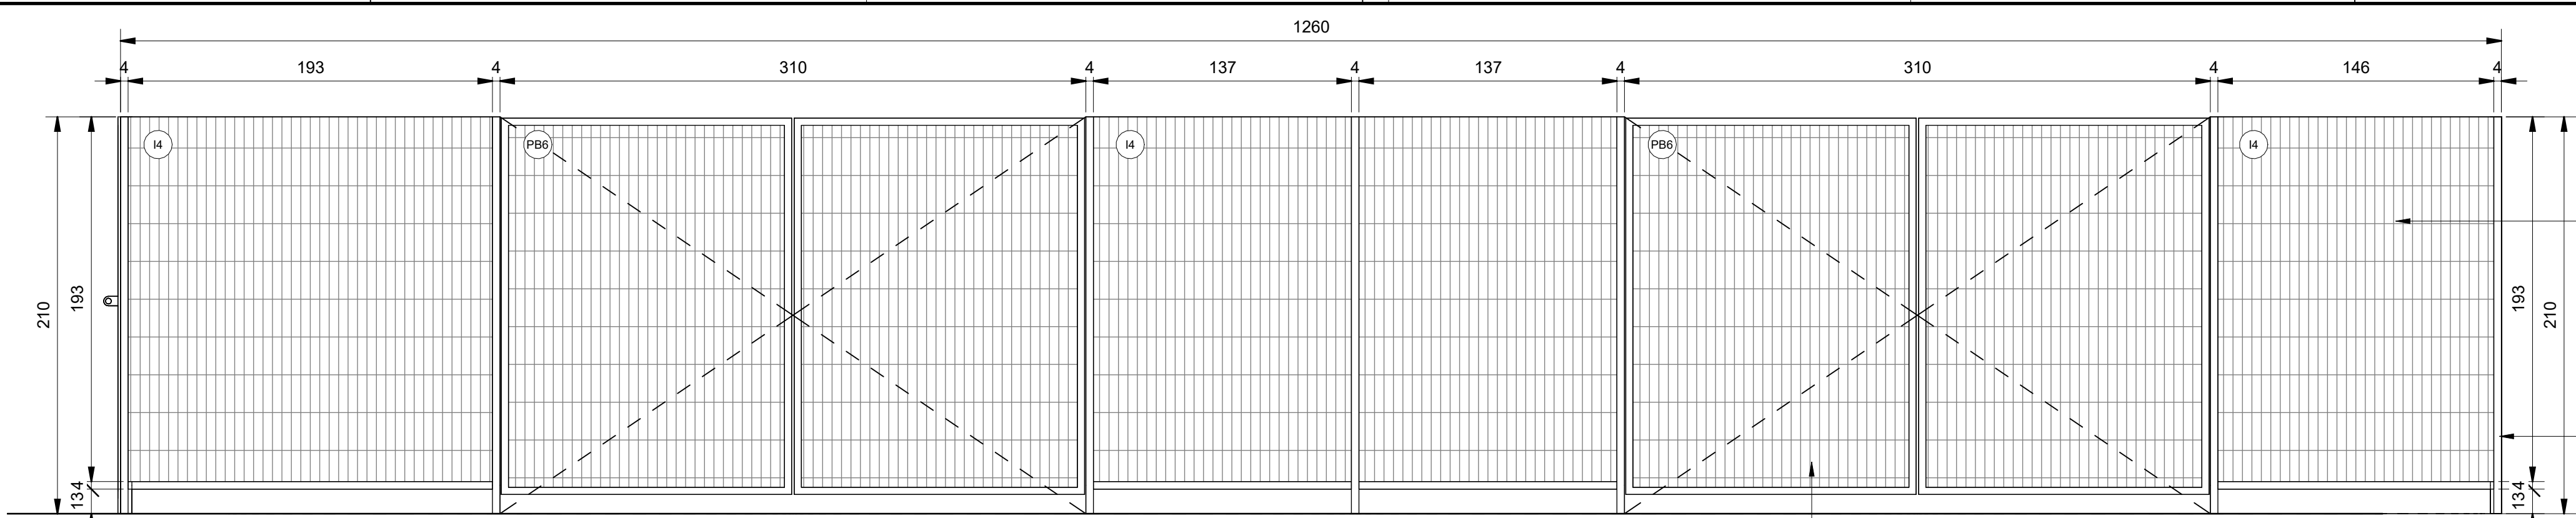


CERCAMENTO - ELEV. 1
1 : 25

PARA DETALHAMENTO DO PORTÃO VER
DETALHES GERAIS DE ESQUADRIAS

VEDAÇÃO EM TELA DE ARAME DE AÇO GALVANIZADO, COM MALHA DE 50x200 mm E FIOS DE DIÂMETRO 5 mm, COM ESTRUTURA COMPOSTA POR POSTES TUBULARES DE SEÇÃO 40 x 60 mm, APLICAÇÃO DE PINTURA ELETROSTÁTICA, COR VERDE (RAL 6005), MONTANTES APARAFUSADOS AO PISO. REF.: BELGO BEKAERT, LINHA NYLOFOR OU SIMILAR.

ESTRUTURA COMPOSTA POR POSTES TUBULARES DE SEÇÃO 40x60 mm, APLICAÇÃO DE PINTURA ELETROSTÁTICA, COR VERDE (RAL 6005), MONTANTES APARAFUSADOS AO PISO. REF.: BELGO BEKAERT, LINHA NYLOFOR OU SIMILAR.

QUADRO DE ESQUADRIAS				
CÓD.	LARGURA (cm)	ALTURA (cm)	DESCRIÇÃO	QTD.
QUADRO DE ESQUADRIAS - PORTAS				
PB6	300,00	210,00	PORTÃO DE GIRO, 2 FOLHAS, EM PAINEL PRÉ-FABRICADO DE TELA COMPOSTO POR POSTES TUBULARES DE SEÇÃO 40x60mm e TELA EM MALHA DE 50x200mm, DIÂMETRO DE 5mm, PRÉ-PINTADO EM PINTURA ELETROSTÁTICA COR VERDE (RAL 6005). REF.: BELGO BEKAERT, LINHA NYLOFOR OU SIMILAR	2
PB8	90,00	210,00	PORTÃO DE GIRO, 1 FOLHA, EM PAINEL PRÉ-FABRICADO DE TELA COMPOSTO POR POSTES TUBULARES DE SEÇÃO 40x60mm e TELA EM MALHA DE 50x200mm, DIÂMETRO DE 5mm, PRÉ-PINTADO EM PINTURA ELETROSTÁTICA COR VERDE (RAL 6005). REF.: BELGO BEKAERT, LINHA NYLOFOR OU SIMILAR	2
QUADRO ESPECIFICAÇÕES DE ACABAMENTOS				
CÓDIGO			DESCRIÇÃO	
CERCAMENTOS				
I4	CERCAMENTO EM PAINEL PRÉ-FABRICADO DE TELA COMPOSTO POR POSTES TUBULARES DE SEÇÃO 40x60mm e TELA EM MALHA DE 50x200mm, DIÂMETRO DE 5mm, PRÉ-PINTADO EM PINTURA ELETROSTÁTICA COR VERDE (RAL 6005). MONTANTES APARAFUSADO AO PISO. REF.: BELGO BEKAERT, LINHA NYLOFOR OU SIMILAR			

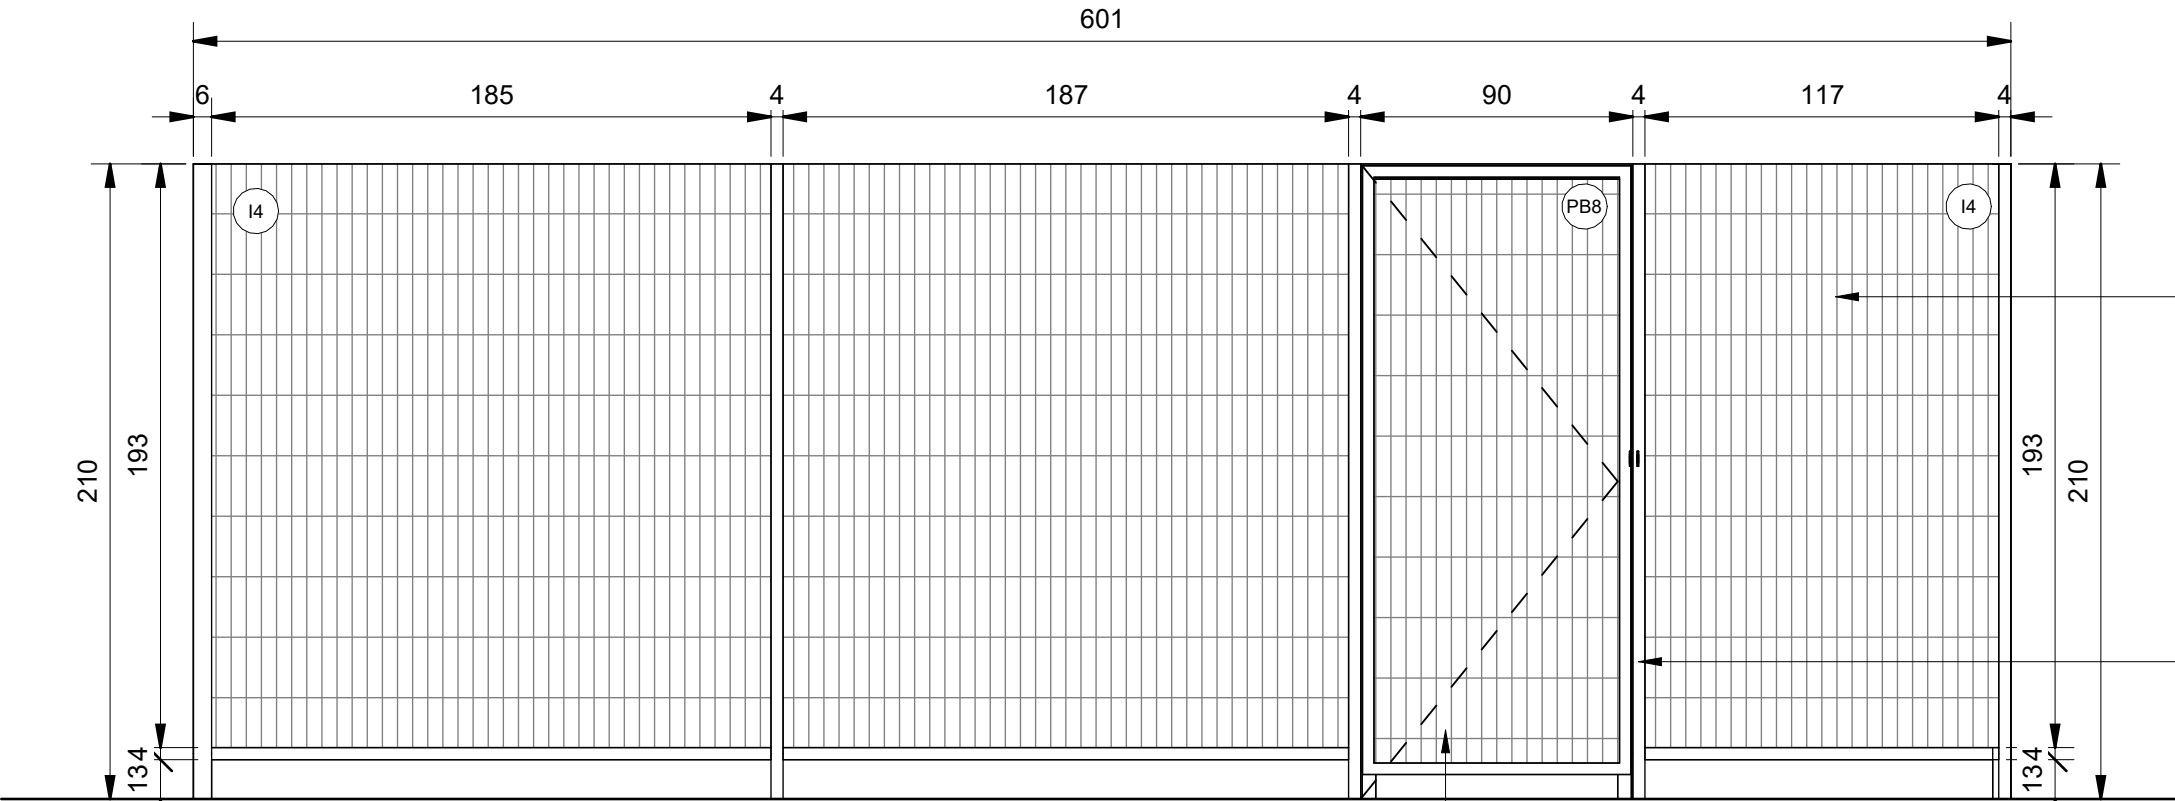


CERCAMENTO - ELEV. 2
1 : 25

VEDAÇÃO EM TELA DE ARAME DE AÇO GALVANIZADO, COM MALHA DE 50x200 mm E FIOS DE DIÂMETRO 5 mm, COM ESTRUTURA COMPOSTA POR POSTES TUBULARES DE SEÇÃO 40 x 60 mm, APLICAÇÃO DE PINTURA ELETROSTÁTICA, COR VERDE (RAL 6005), MONTANTES APARAFUSADOS AO PISO. REF.: BELGO BEKAERT, LINHA NYLOFOR OU SIMILAR.

ESTRUTURA COMPOSTA POR POSTES TUBULARES DE SEÇÃO 40x60 mm, APLICAÇÃO DE PINTURA ELETROSTÁTICA, COR VERDE (RAL 6005), MONTANTES APARAFUSADOS AO PISO. REF.: BELGO BEKAERT, LINHA NYLOFOR OU SIMILAR.


PARA DETALHAMENTO DO PORTÃO VER
DETALHES GERAIS DE ESQUADRIAS

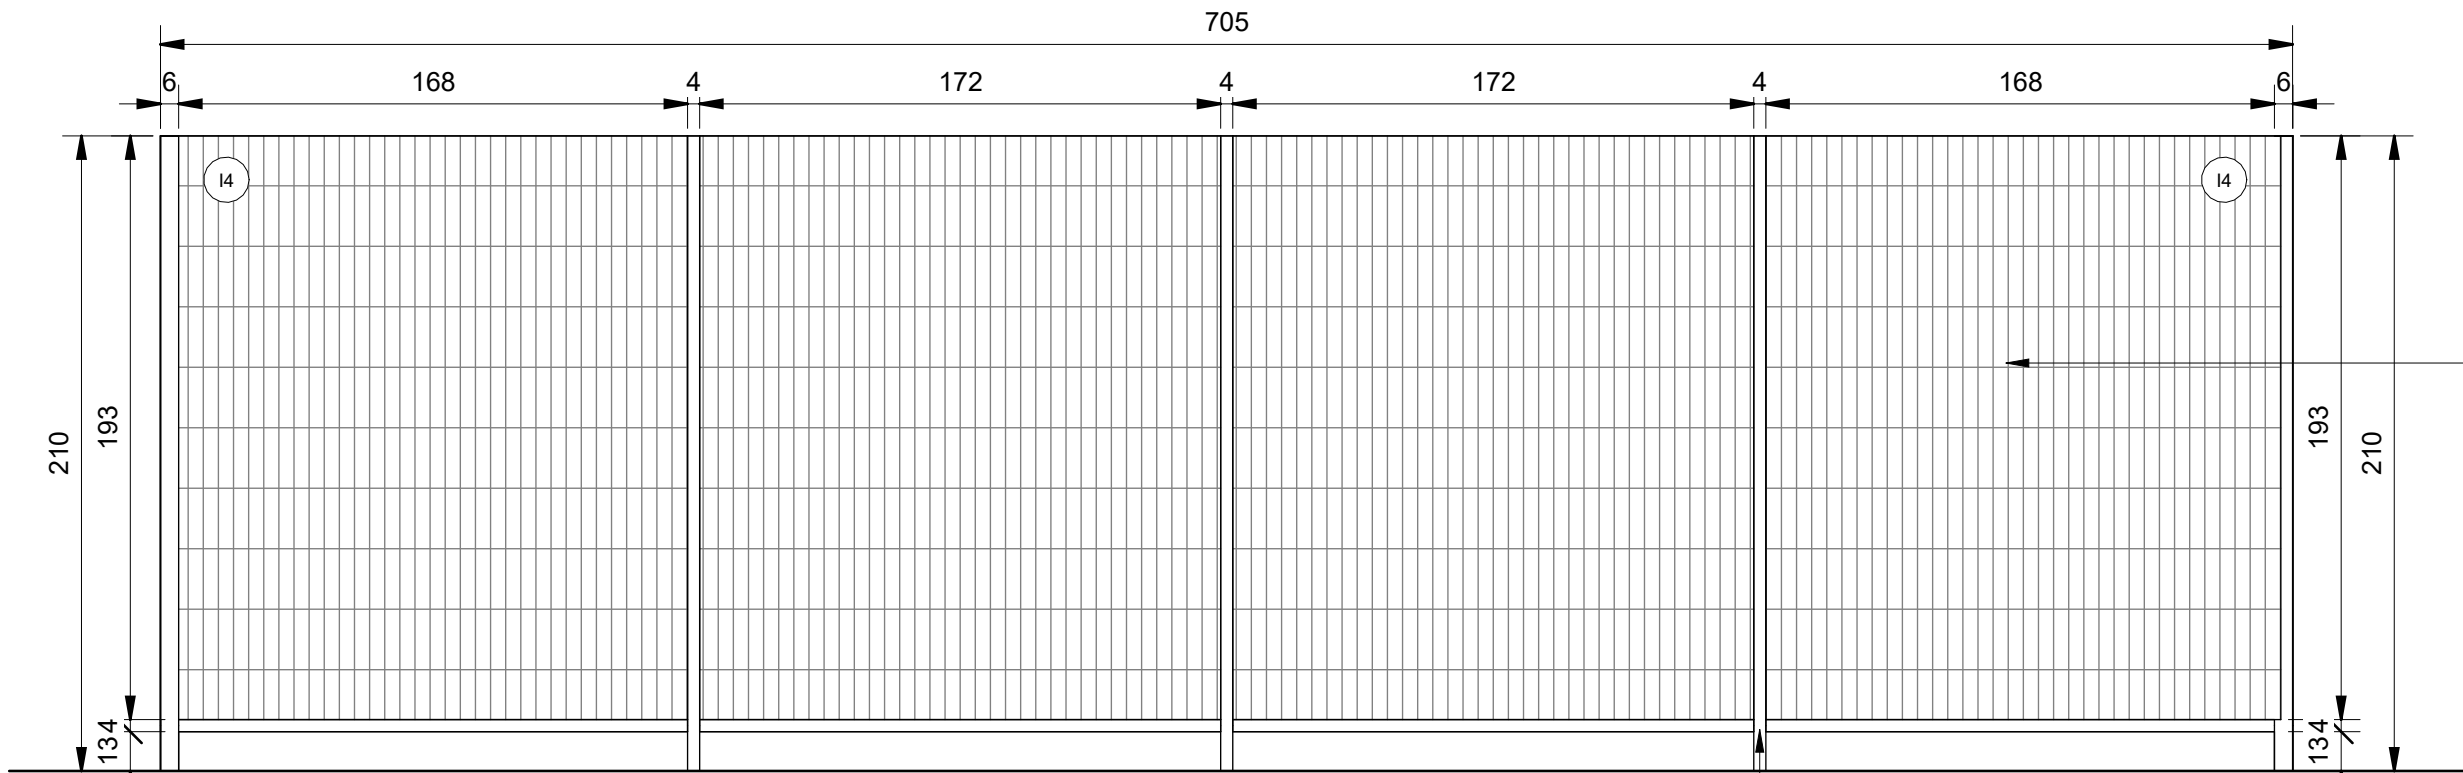

CERCAMENTO - ELEV. 3
1 : 25

VEDAÇÃO EM TELA DE ARAME DE AÇO GALVANIZADO, COM MALHA DE 50x200 mm E FIOS DE DIÂMETRO 5 mm, COM ESTRUTURA COMPOSTA POR POSTES TUBULARES DE SEÇÃO 40 x 60 mm, APLICAÇÃO DE PINTURA ELETROSTÁTICA, COR VERDE (RAL 6005), MONTANTES APARAFUSADOS AO PISO. REF.: BELGO BEKAERT, LINHA NYLOFOR OU SIMILAR.


ESTRUTURA COMPOSTA POR POSTES TUBULARES DE SEÇÃO 40x60 mm, APLICAÇÃO DE PINTURA ELETROSTÁTICA, COR VERDE (RAL 6005), MONTANTES APARAFUSADOS AO PISO. REF.: BELGO BEKAERT, LINHA NYLOFOR OU SIMILAR.

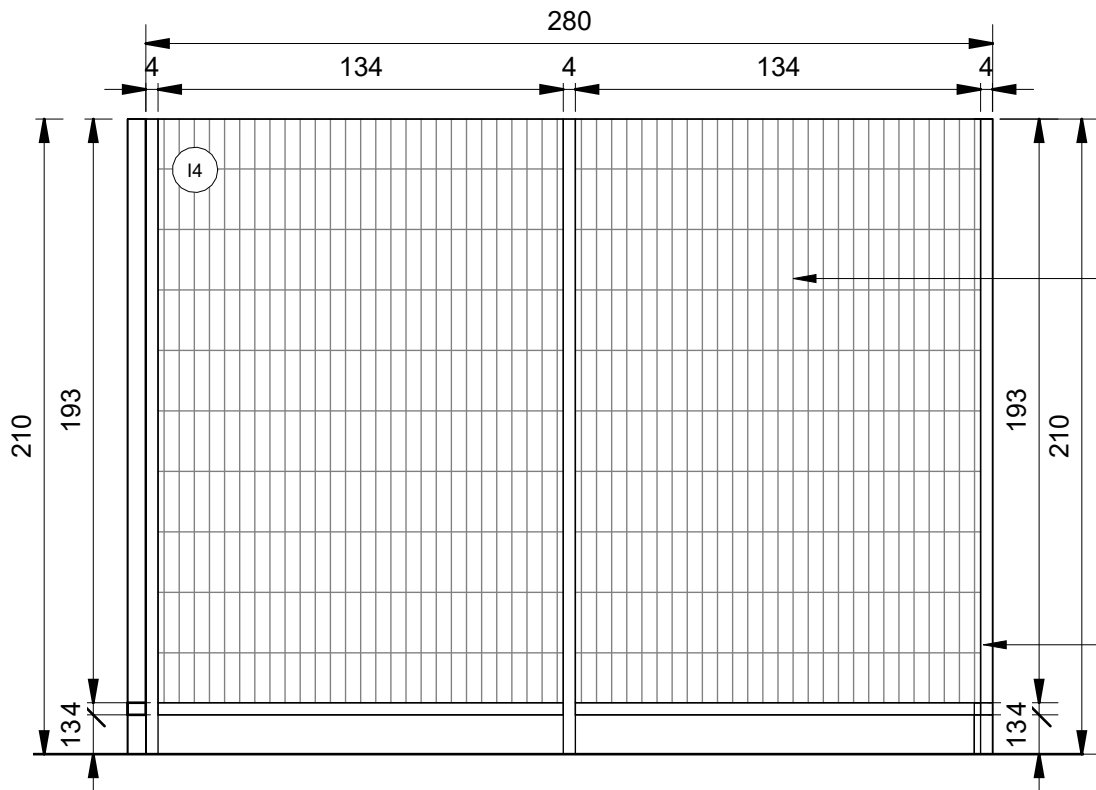

CERCAMENTO - ELEV. 4
1 : 25

VEDAÇÃO EM TELA DE ARAME DE AÇO GALVANIZADO, COM MALHA DE 50x200 mm E FIOS DE DIÂMETRO 5 mm, COM ESTRUTURA COMPOSTA POR POSTES TUBULARES DE SEÇÃO 40 x 60 mm, APLICAÇÃO DE PINTURA ELETROSTÁTICA, COR VERDE (RAL 6005), MONTANTES APARAFUSADOS AO PISO. REF.: BELGO BEKAERT, LINHA NYLOFOR OU SIMILAR.

ESTRUTURA COMPOSTA POR POSTES TUBULARES DE SEÇÃO 40x60 mm, APLICAÇÃO DE PINTURA ELETROSTÁTICA, COR VERDE (RAL 6005), MONTANTES APARAFUSADOS AO PISO. REF.: BELGO BEKAERT, LINHA NYLOFOR OU SIMILAR.

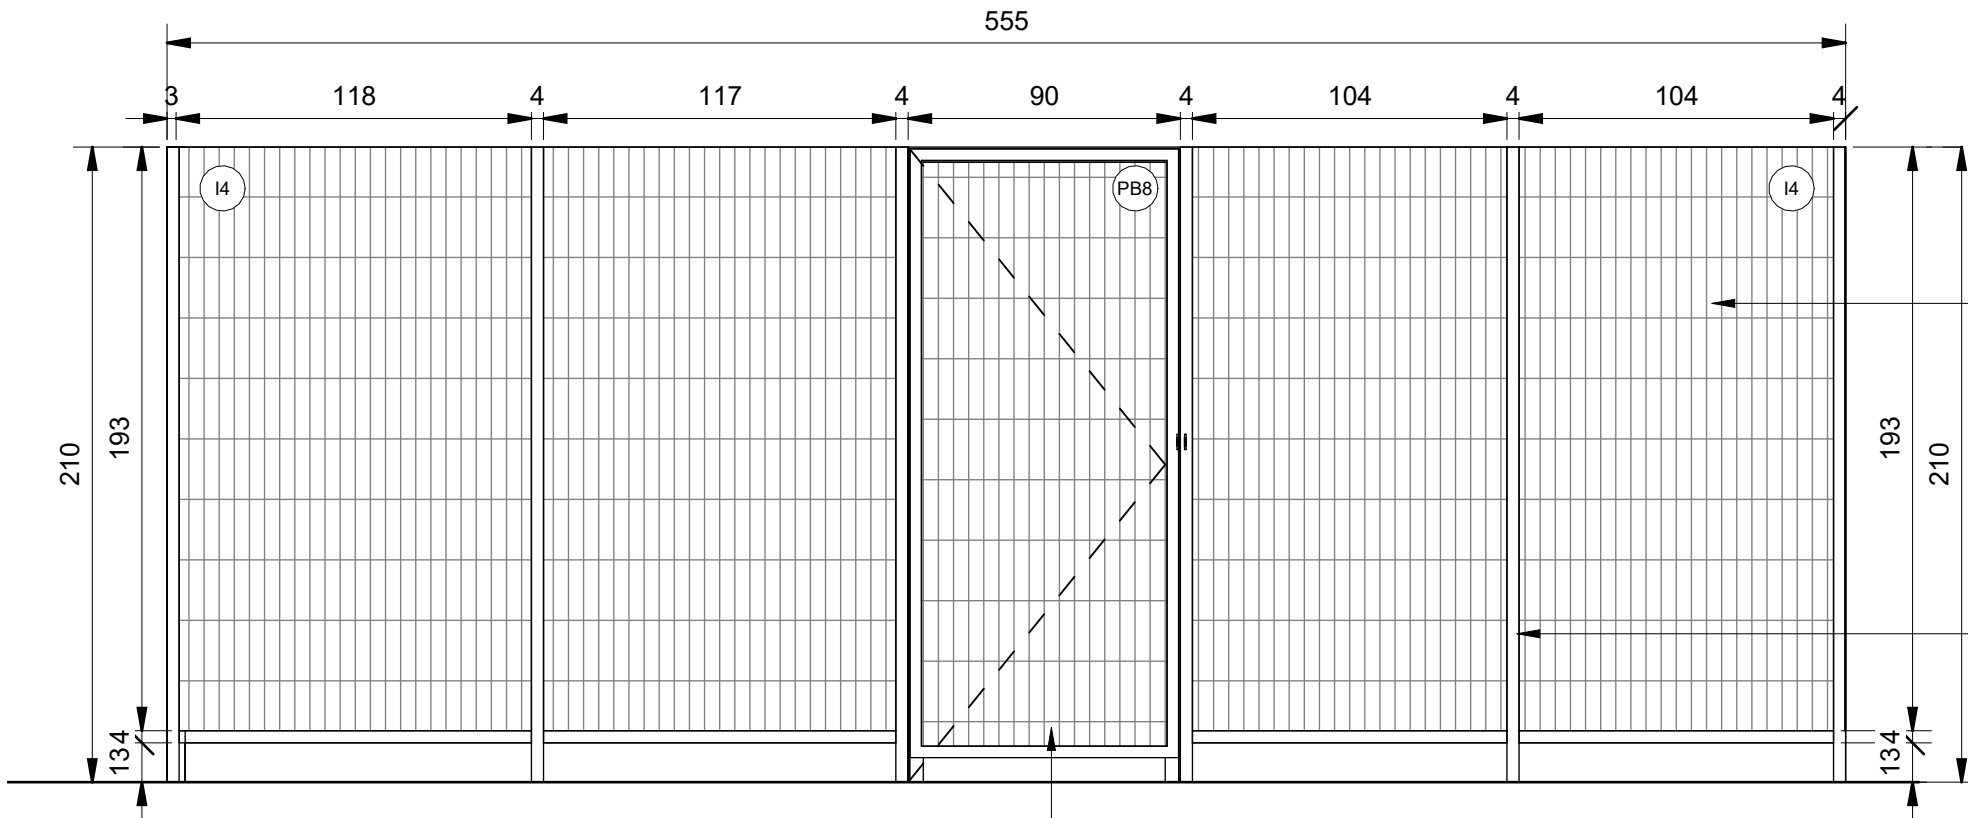


CERCAMENTO - ELEV. 5
1 : 25

VEDAÇÃO EM TELA DE ARAME DE AÇO GALVANIZADO, COM MALHA DE 50x200 mm E FIOS DE DIÂMETRO 5 mm, COM ESTRUTURA COMPOSTA POR POSTES TUBULARES DE SEÇÃO 40 x 60 mm, APLICAÇÃO DE PINTURA ELETROSTÁTICA, COR VERDE (RAL 6005), MONTANTES APARAFUSADOS AO PISO. REF.: BELGO BEKAERT, LINHA NYLOFOR OU SIMILAR.

ESTRUTURA COMPOSTA POR POSTES TUBULARES DE SEÇÃO 40x60 mm, APLICAÇÃO DE PINTURA ELETROSTÁTICA, COR VERDE (RAL 6005), MONTANTES APARAFUSADOS AO PISO. REF.: BELGO BEKAERT, LINHA NYLOFOR OU SIMILAR.

PARA DETALHAMENTO DO PORTÃO VER
DETALHES GERAIS DE ESQUADRIAS

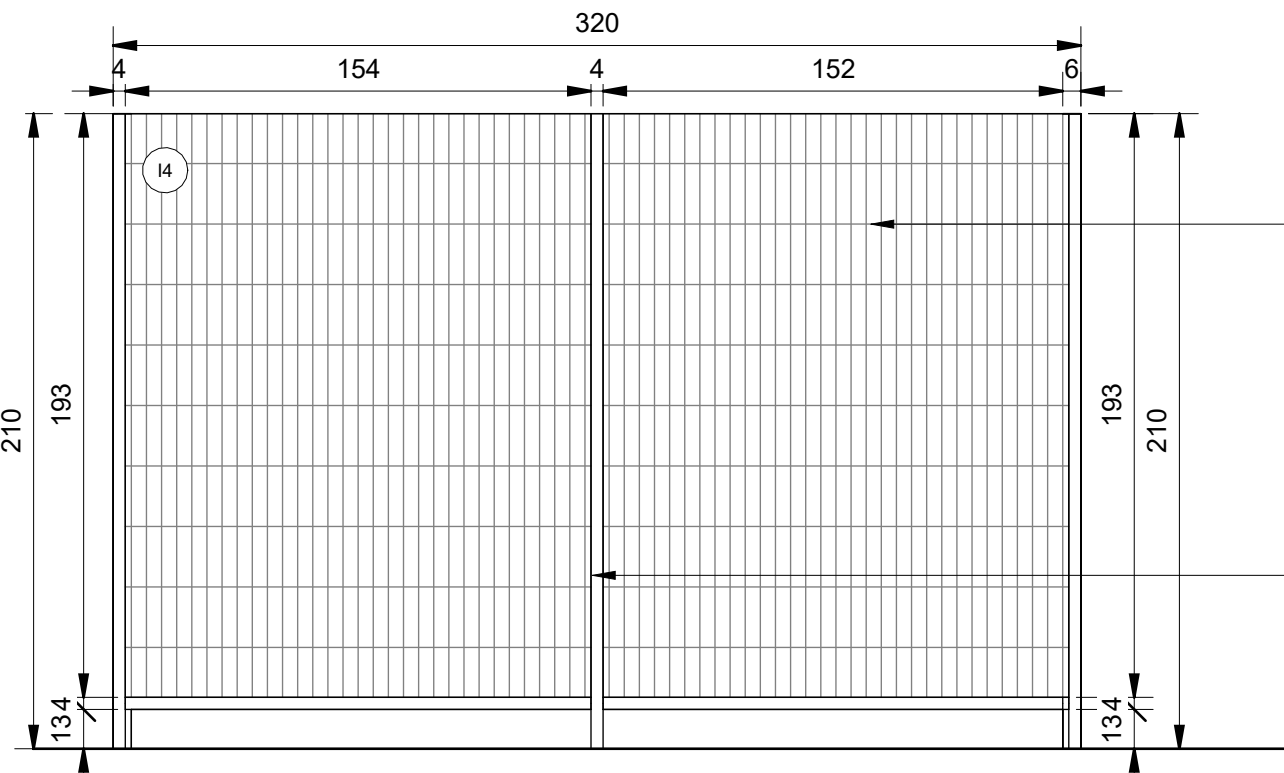

CERCAMENTO - ELEV. 6
1 : 25

VEDAÇÃO EM TELA DE ARAME DE AÇO GALVANIZADO, COM MALHA DE 50x200 mm E FIOS DE DIÂMETRO 5 mm, COM ESTRUTURA COMPOSTA POR POSTES TUBULARES DE SEÇÃO 40 x 60 mm, APLICAÇÃO DE PINTURA ELETROSTÁTICA, COR VERDE (RAL 6005), MONTANTES APARAFUSADOS AO PISO. REF.: BELGO BEKAERT, LINHA NYLOFOR OU SIMILAR.

ESTRUTURA COMPOSTA POR POSTES TUBULARES DE SEÇÃO 40x60 mm, APLICAÇÃO DE PINTURA ELETROSTÁTICA, COR VERDE (RAL 6005), MONTANTES APARAFUSADOS AO PISO. REF.: BELGO BEKAERT, LINHA NYLOFOR OU SIMILAR.