




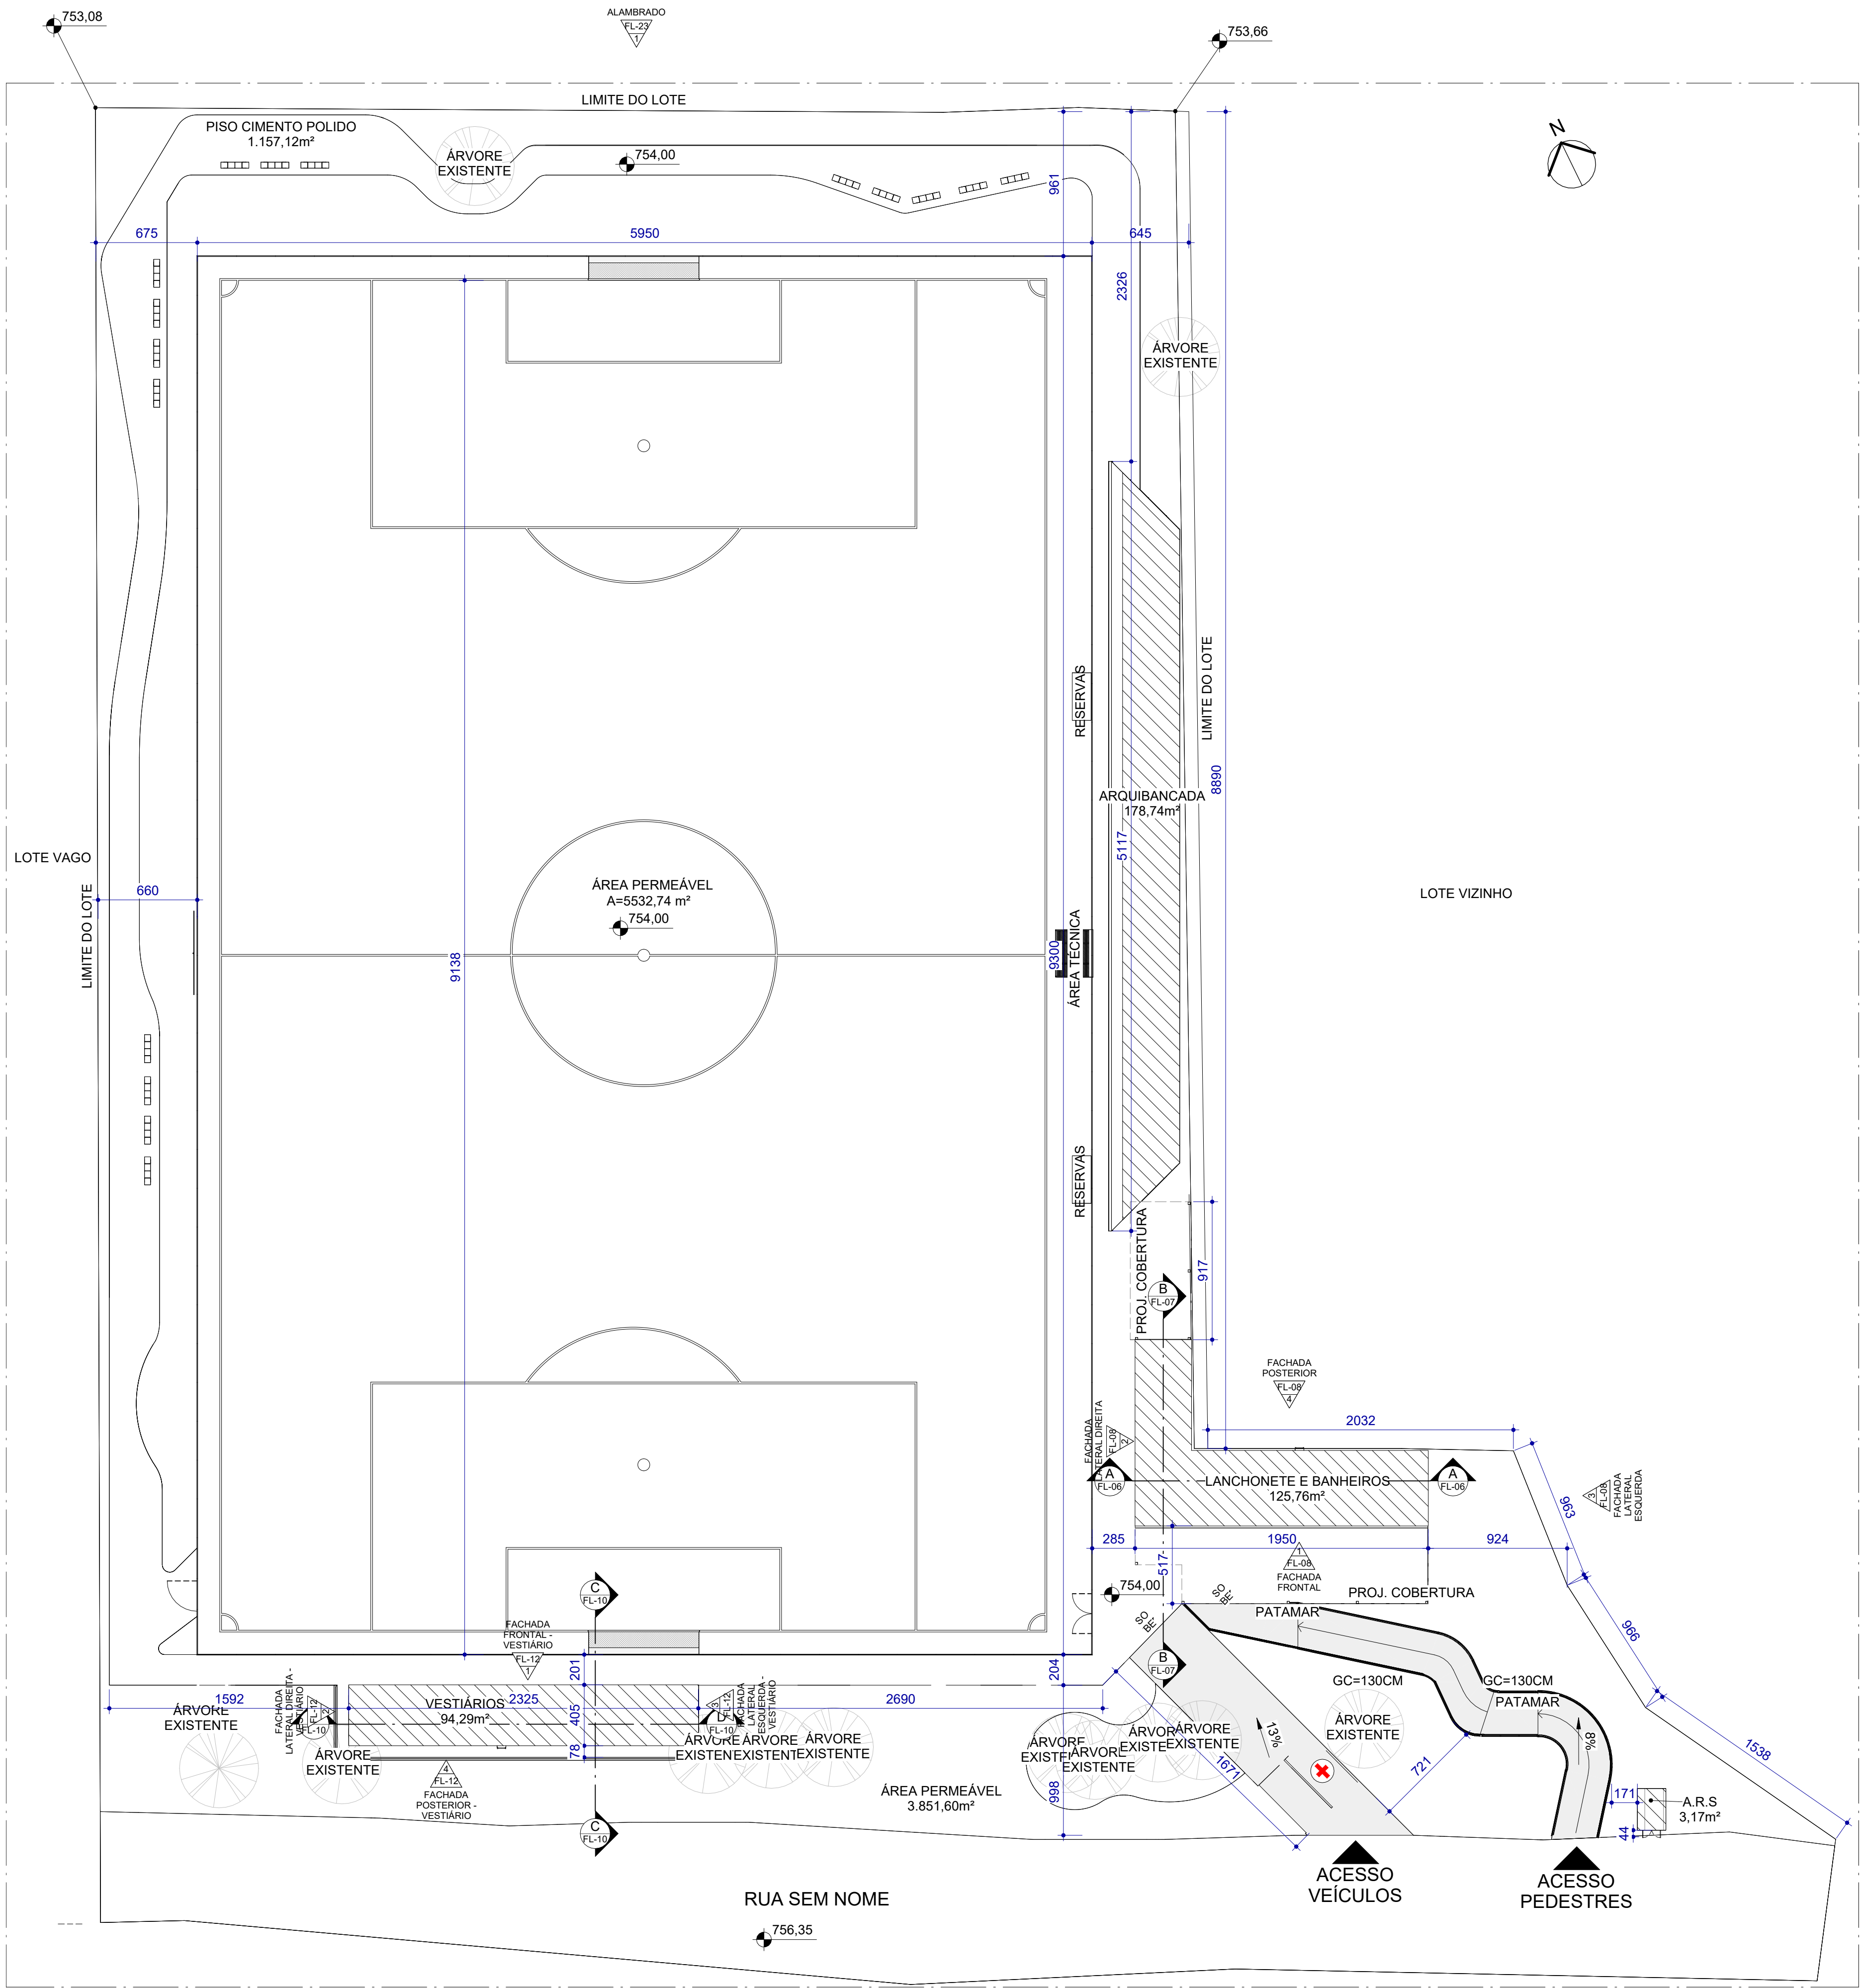

1 PLANTA DE IMPLANTAÇÃO
ESCALA: 1 : 250

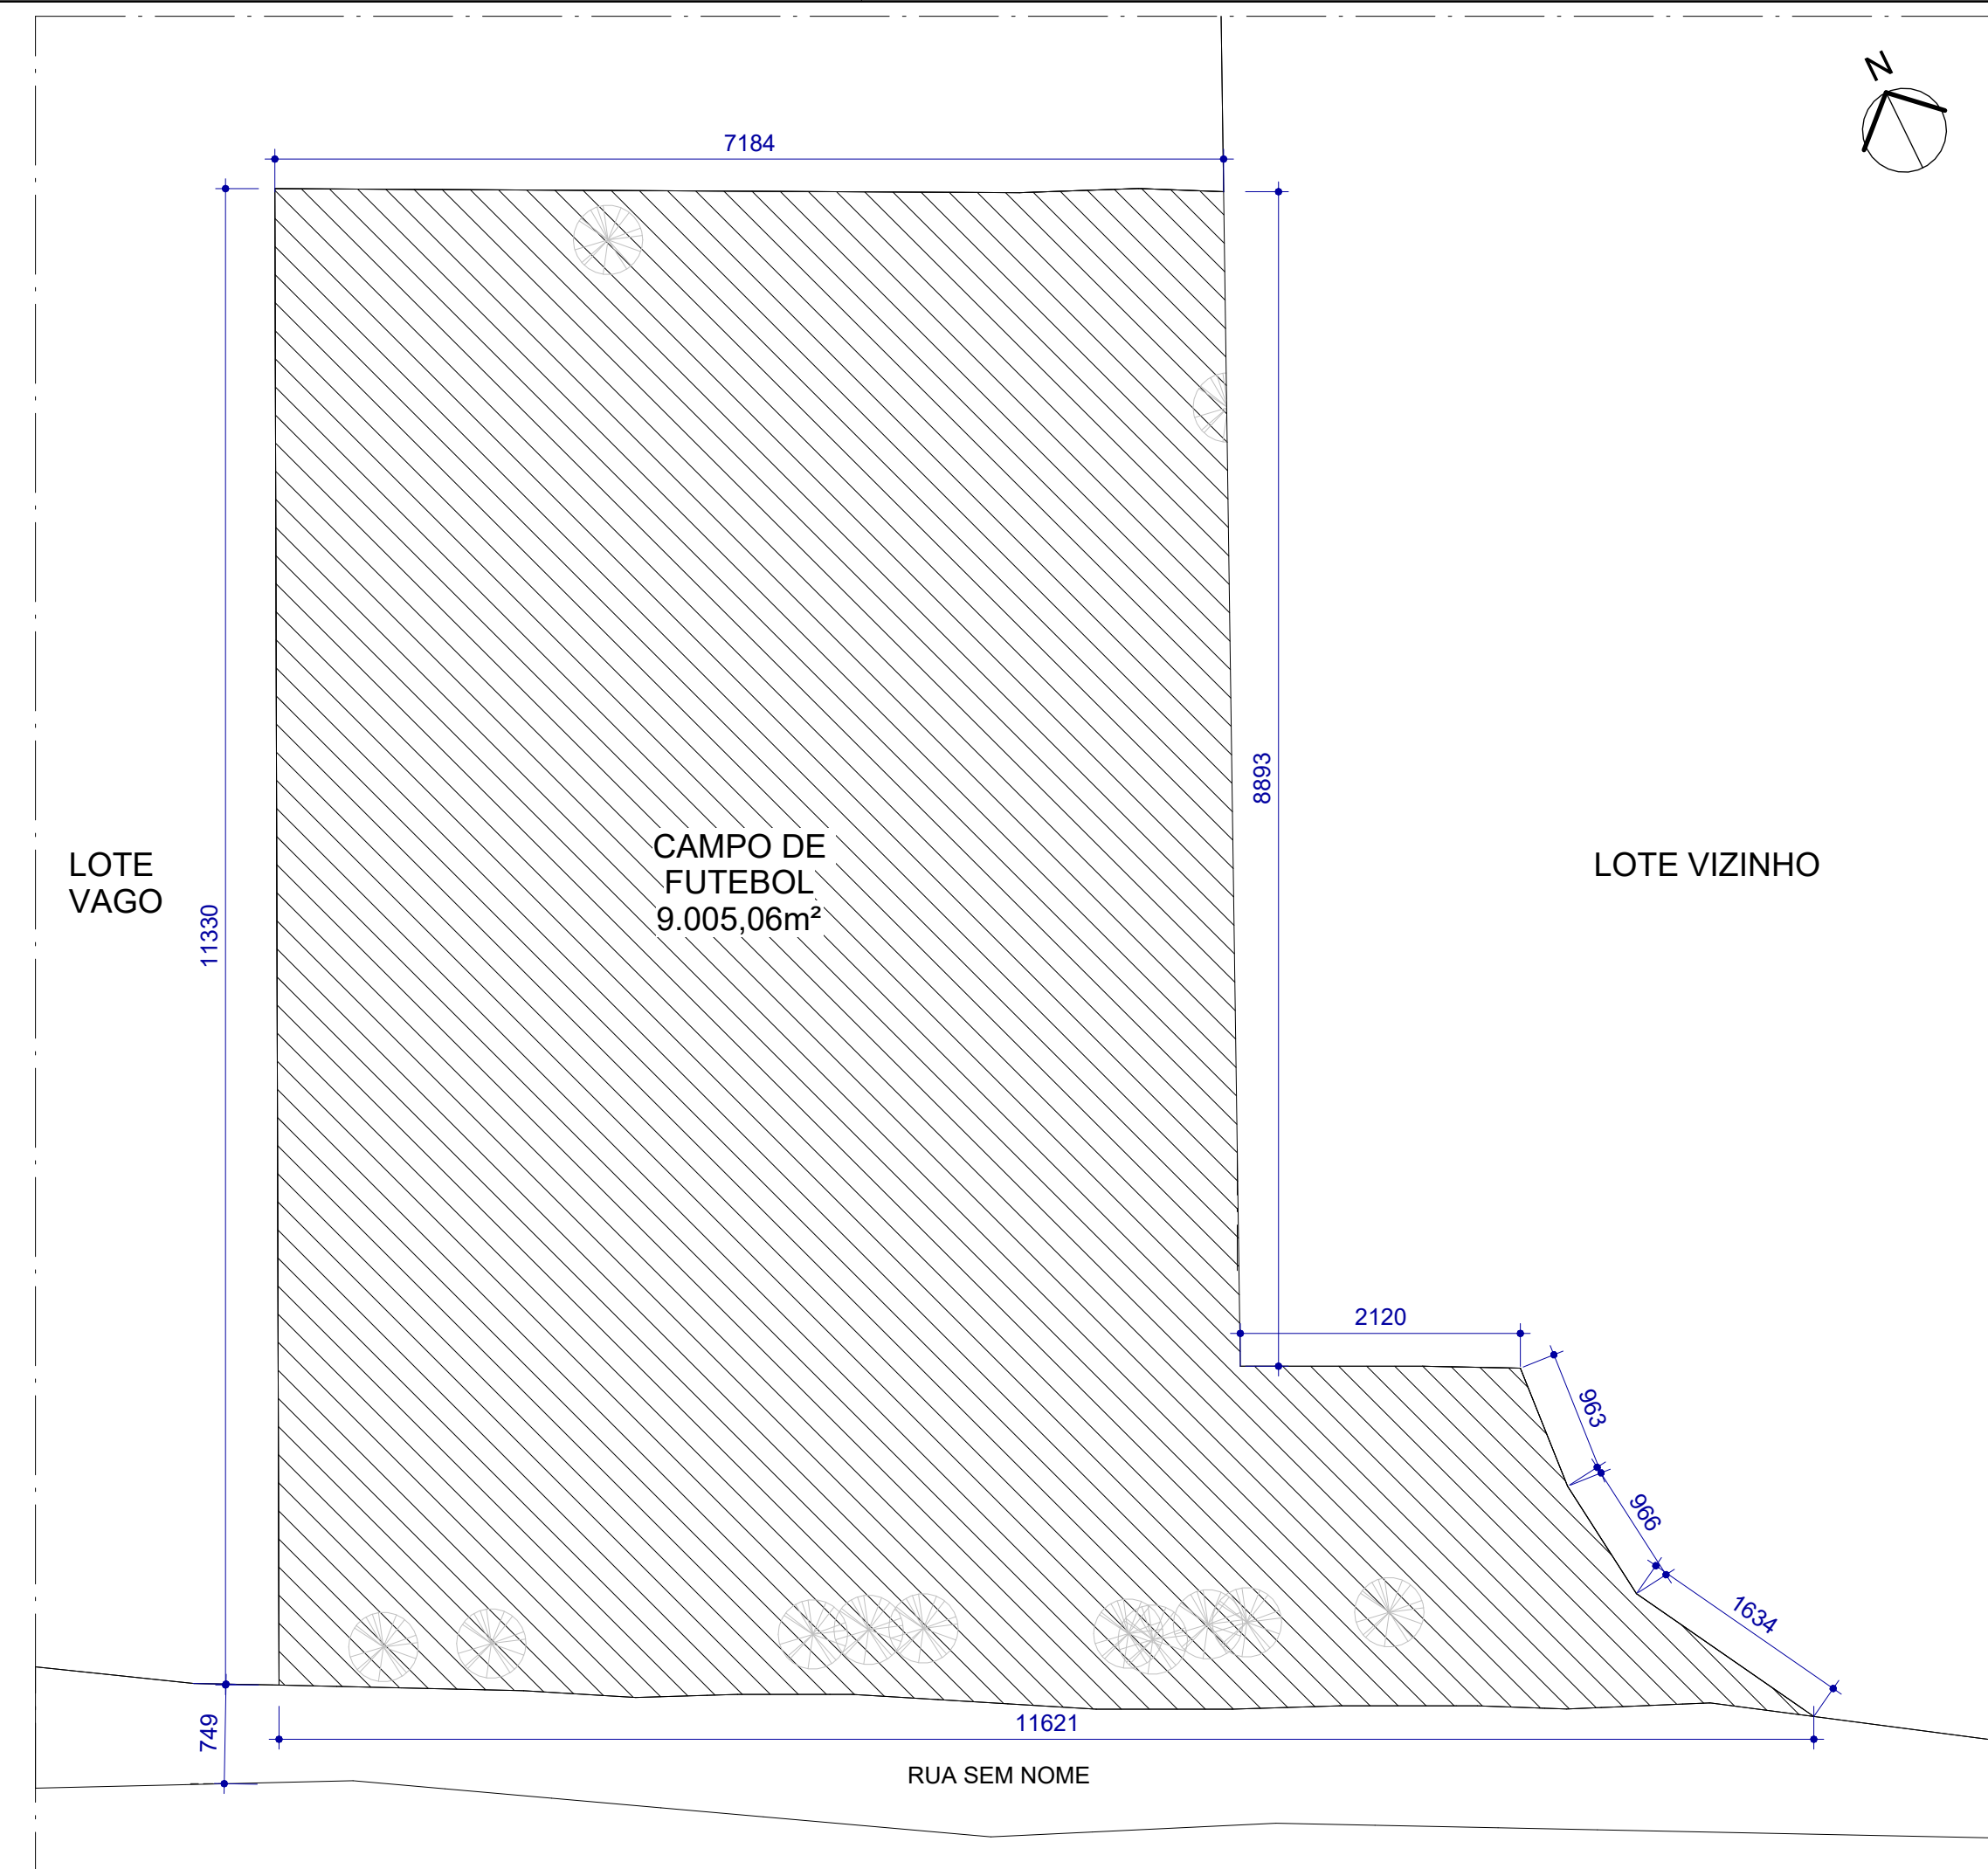


2 PLANTA DE SITUAÇÃO
ESCALA: 1 : 500

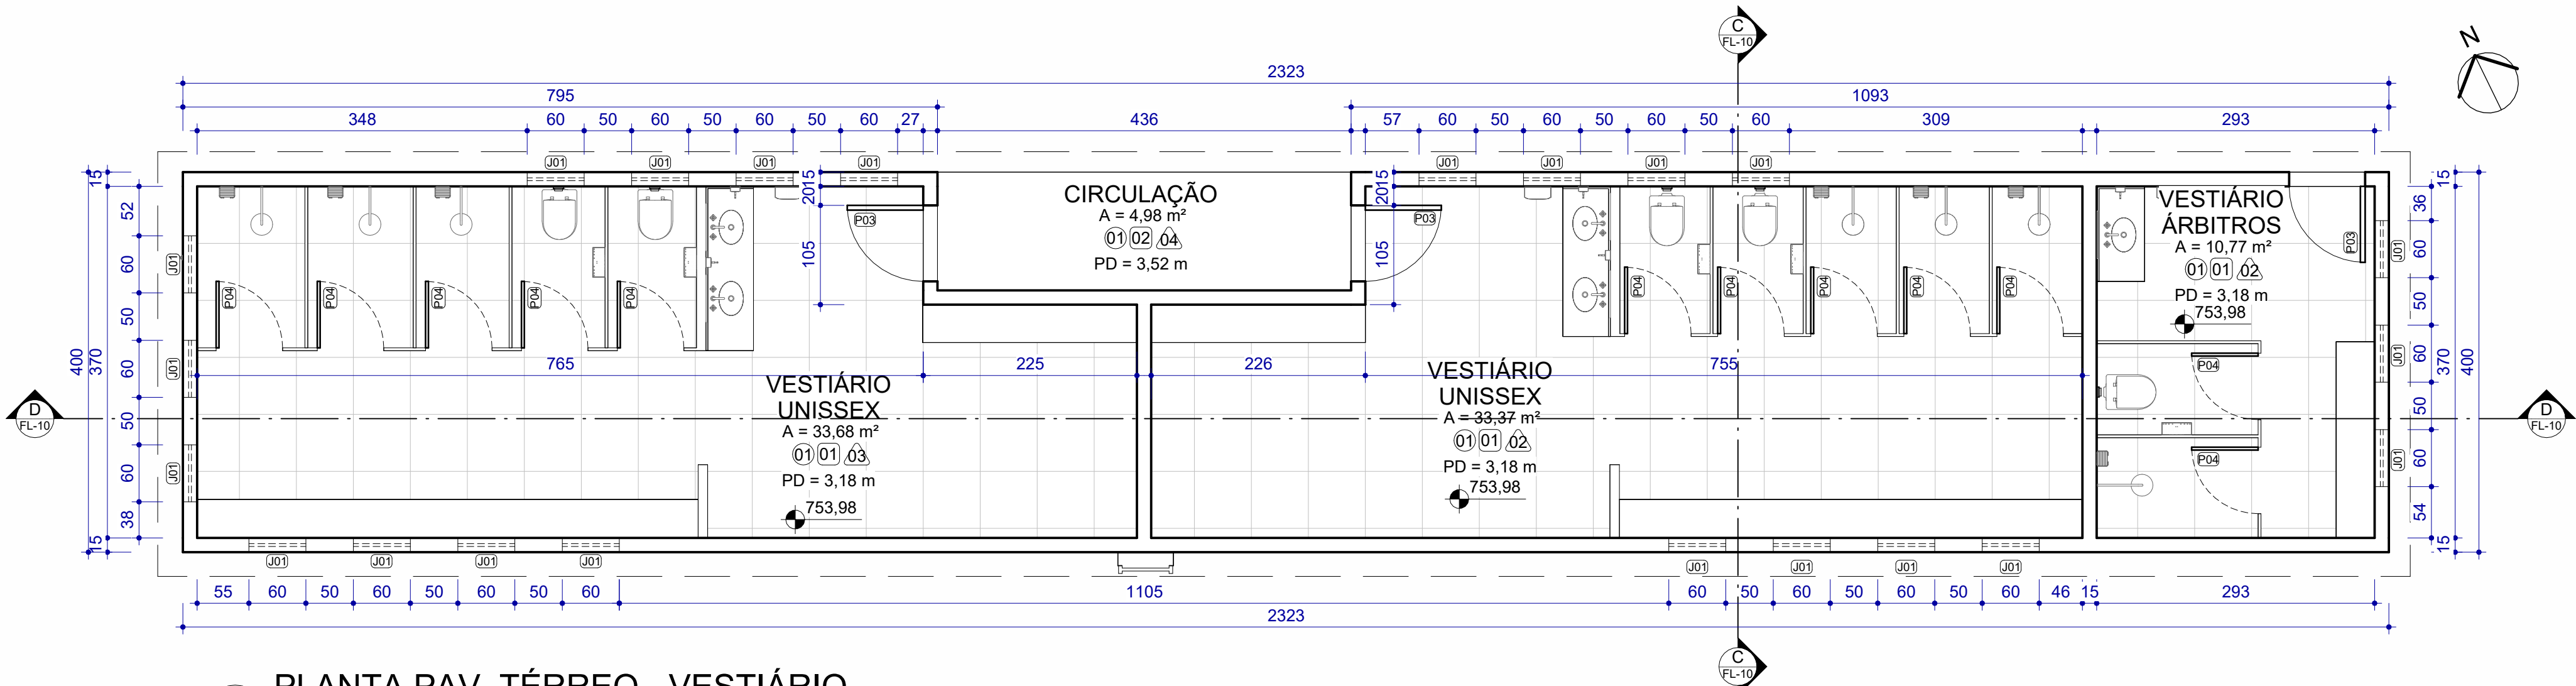


5 PLANTA PAV. TÉRREO - VESTIÁRIO

ESCALA: 1 : 50

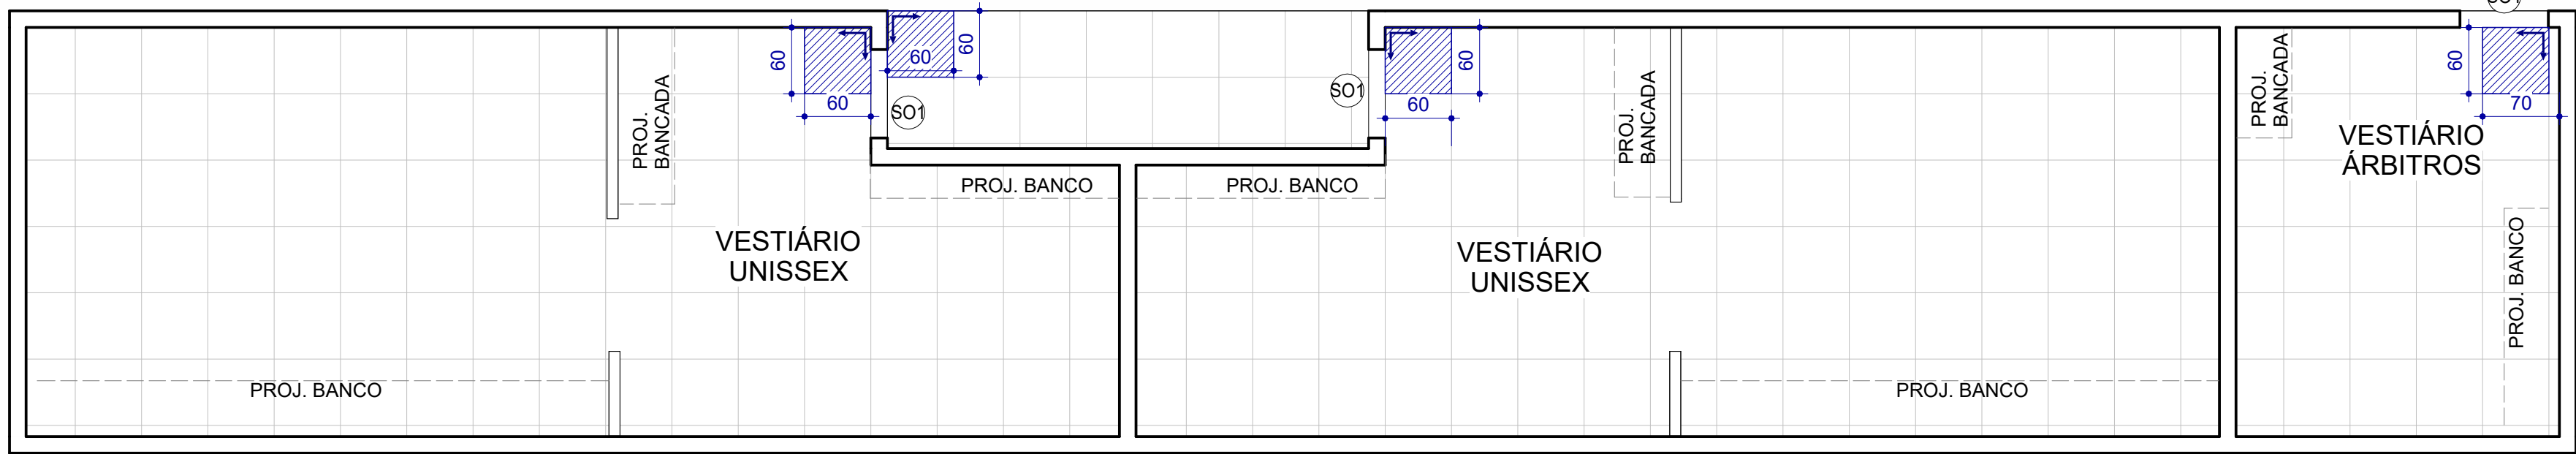

6 PLANTA PAGINAÇÃO DE PISO - VESTIÁRIO


ESCALA: 1 : 50

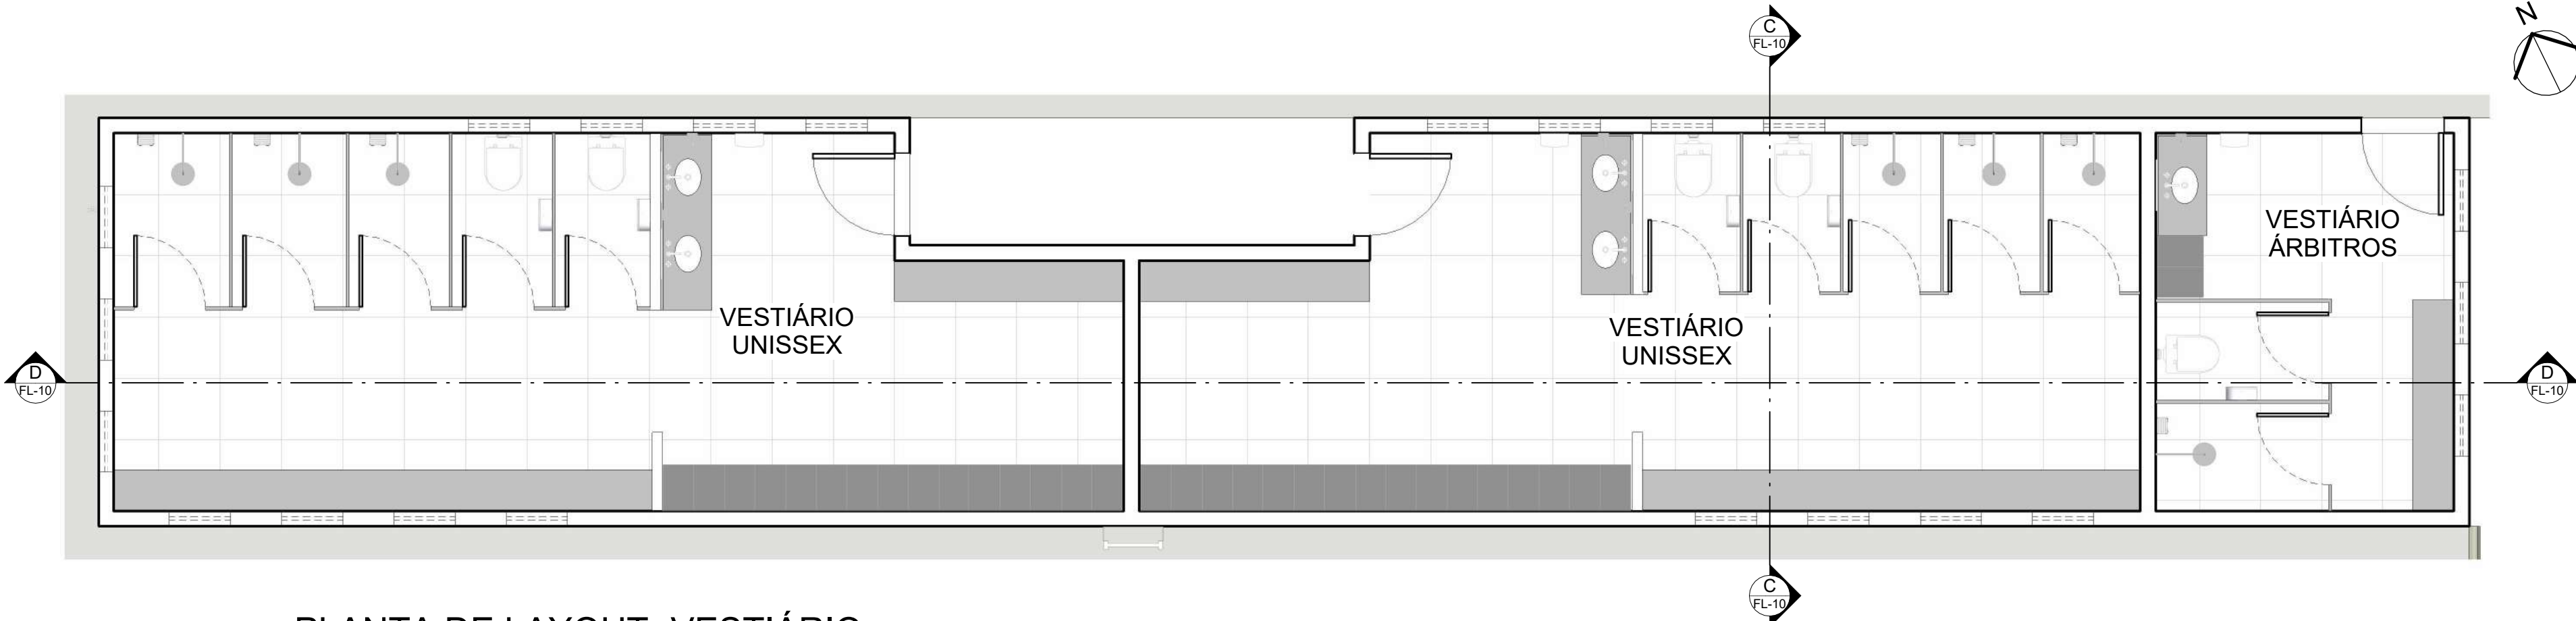

7 PLANTA DE LAYOUT- VESTIÁRIO


ESCALA: 1 : 50

LEGENDA ESPECIFICAÇÕES					
	PISO		TETO		PAREDE
	DIVERSOS				
LEGENDA PAGINAÇÃO DE PISO					
ÍCIO E SENTIDO DA PAGINAÇÃO DE PISO E REVESTIMENTOS					
QUADRO GERAL DE ESPECIFICAÇÕES - ACABAMENTOS					
PISO / SUPERFÍCIES HORIZONTAIS					
PISO EM CERÂMICA 60X60CM NA COR BRANCO					
SOLEIRA EM GRANITO CINZA ANDORINHA ACABAMENTO POLIDO					
QUADRO GERAL DE ESPECIFICAÇÕES - TETO					
TETOS					
FORRO EM GESSO COM PINTURA EM TINTA ACRÍLICA NA COR BRANCO NEVE					
PINTURA EM TETO COM TINTA ACRÍLICA NA COR BRANCO NEVE					
QUADRO GERAL DE ESPECIFICAÇÕES - PAREDE					
VEDAÇÕES / REVESTIMENTOS / ELEMENTOS VERTICAIS					
REVESTIMENTO EM CERÂMICA 60X60CM NA COR BRANCO ATÉ 150CM DE ALTURA DO PISO;					
SEGUIDA DE PINTURA ACRÍLICA NA COR BRANCO NEVE ATÉ O FORRO					
REVESTIMENTO EM CERÂMICA 60X60CM NA COR BRANCO ATÉ O TETO;					
REVESTIMENTO EM PINTURA ACRÍLICA, COR AZUL CÉU NUBLADO					
REVESTIMENTO EM PINTURA ACRÍLICA, COR BRANCO					
QUADRO GERAL DE ESQUADRIAS - JANELAS					
LARGURA	ALTURA	ALTURA PEITORIL	ABERTURA E NÚM. FOLHAS	MATERIAL/ACABAMENTO	QNTD.
60	80	180	ABRIR, 1 FOLHA	JANELA EM VIDRO LISO, COMUM, INCOLOR, E=6MM, PERFIS DE ALUMÍNIO COR NATURAL	22
QUADRO GERAL DE ESQUADRIAS - PORTAS					
LARGURA	ALTURA	ABERTURA E NÚM. FOLHAS	MATERIAL/ACABAMENTO		QNTD.
80	210	ABRIR, 1 FOLHA	PORTA VENEZIANA COM PERFIL EM ALUMÍNIO ANODIZADO NA COR NATURAL		3
70	180	ABRIR, 1 FOLHA	PORTA VENEZIANA DE ALUMÍNIO		12
DIVERSOS					
MOBILIÁRIOS / PEÇAS HIDROSSANITÁRIAS / ACESSÓRIOS / DIVERSOS					QNTD.
Bacia sanitária convencional					5
CUBA DE EMBUTIR OVAL EM LOUÇA BRANCA, 35 X 50CM OU EQUIVALENTE					5
VÁLVULA DE DESCARGA					5
SABONETEIRA					7
SABONETEIRA PLÁSTICA TIPO DISPENSER PARA SABONETE LÍQUIDO COM RESERVATÓRIO DE 800ML					5
PAPELEIRA PLÁSTICA TIPO DISPENSER PARA PAPEL HIGIÊNICO ROLÃO					5
TORNEIRA CROMADA DE MESA, COM MISTURADOR, 1/2 OU 3/4, PARA LAVATÓRIO					5
CHUVEIRO					7
DISPENSER EM PLÁSTICO PARA PAPEL TOALHA 2 OU 3 FOLHAS					3
TORNEIRA CROMADA 1/2 OU 3/4 PARA TANQUE					1
TABELA DE GUARDA CORPO					
DESCRIÇÃO					QNTD.
GUARDA-CORPO EM (AÇO GALVANIZADO/AÇO INOX) H=130 CM, COM CORRIMÃO DUPLO, FIXADO SOBRE DE GUIA DE BALIZAMENTO EM CONCRETO					8
GUARDA-CORPO EM (AÇO GALVANIZADO/AÇO INOX) H=110 CM, COM CORRIMÃO DUPLO, FIXADO SOBRE DE GUIA DE BALIZAMENTO EM CONCRETO					2

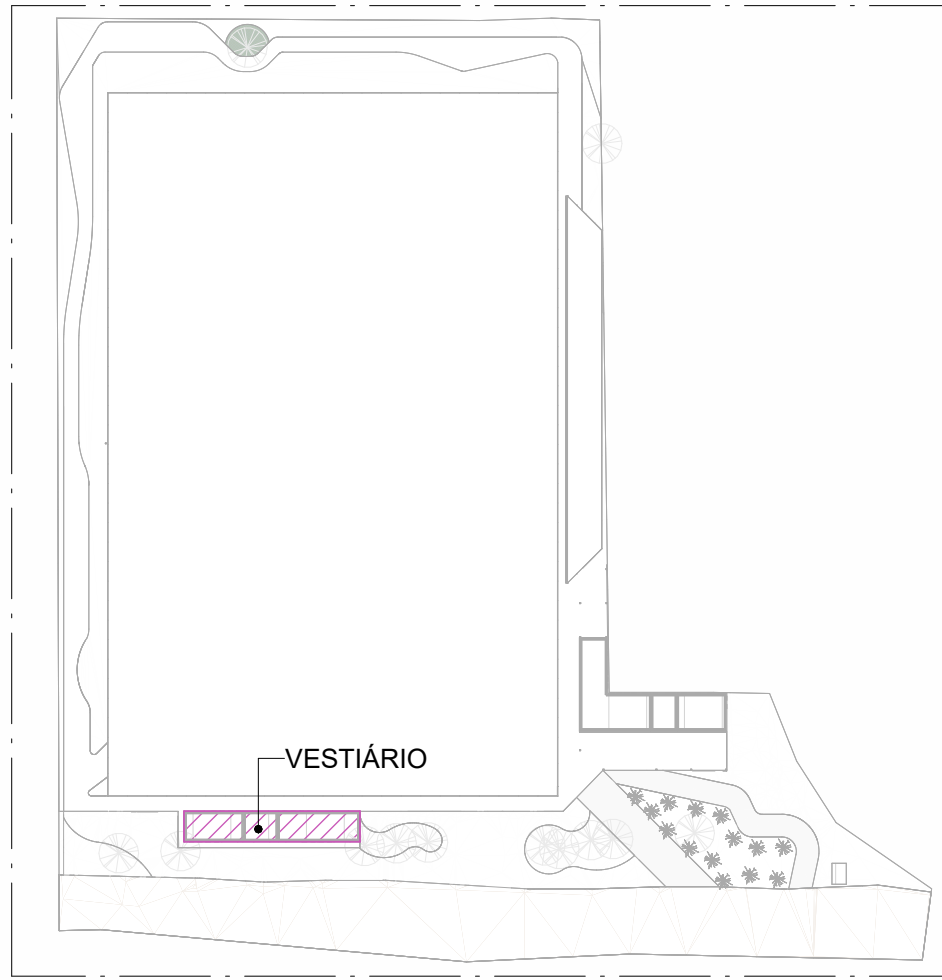


8 MAPA CHAVE - VESTIÁRIO

ESCALA: 1 : 1000

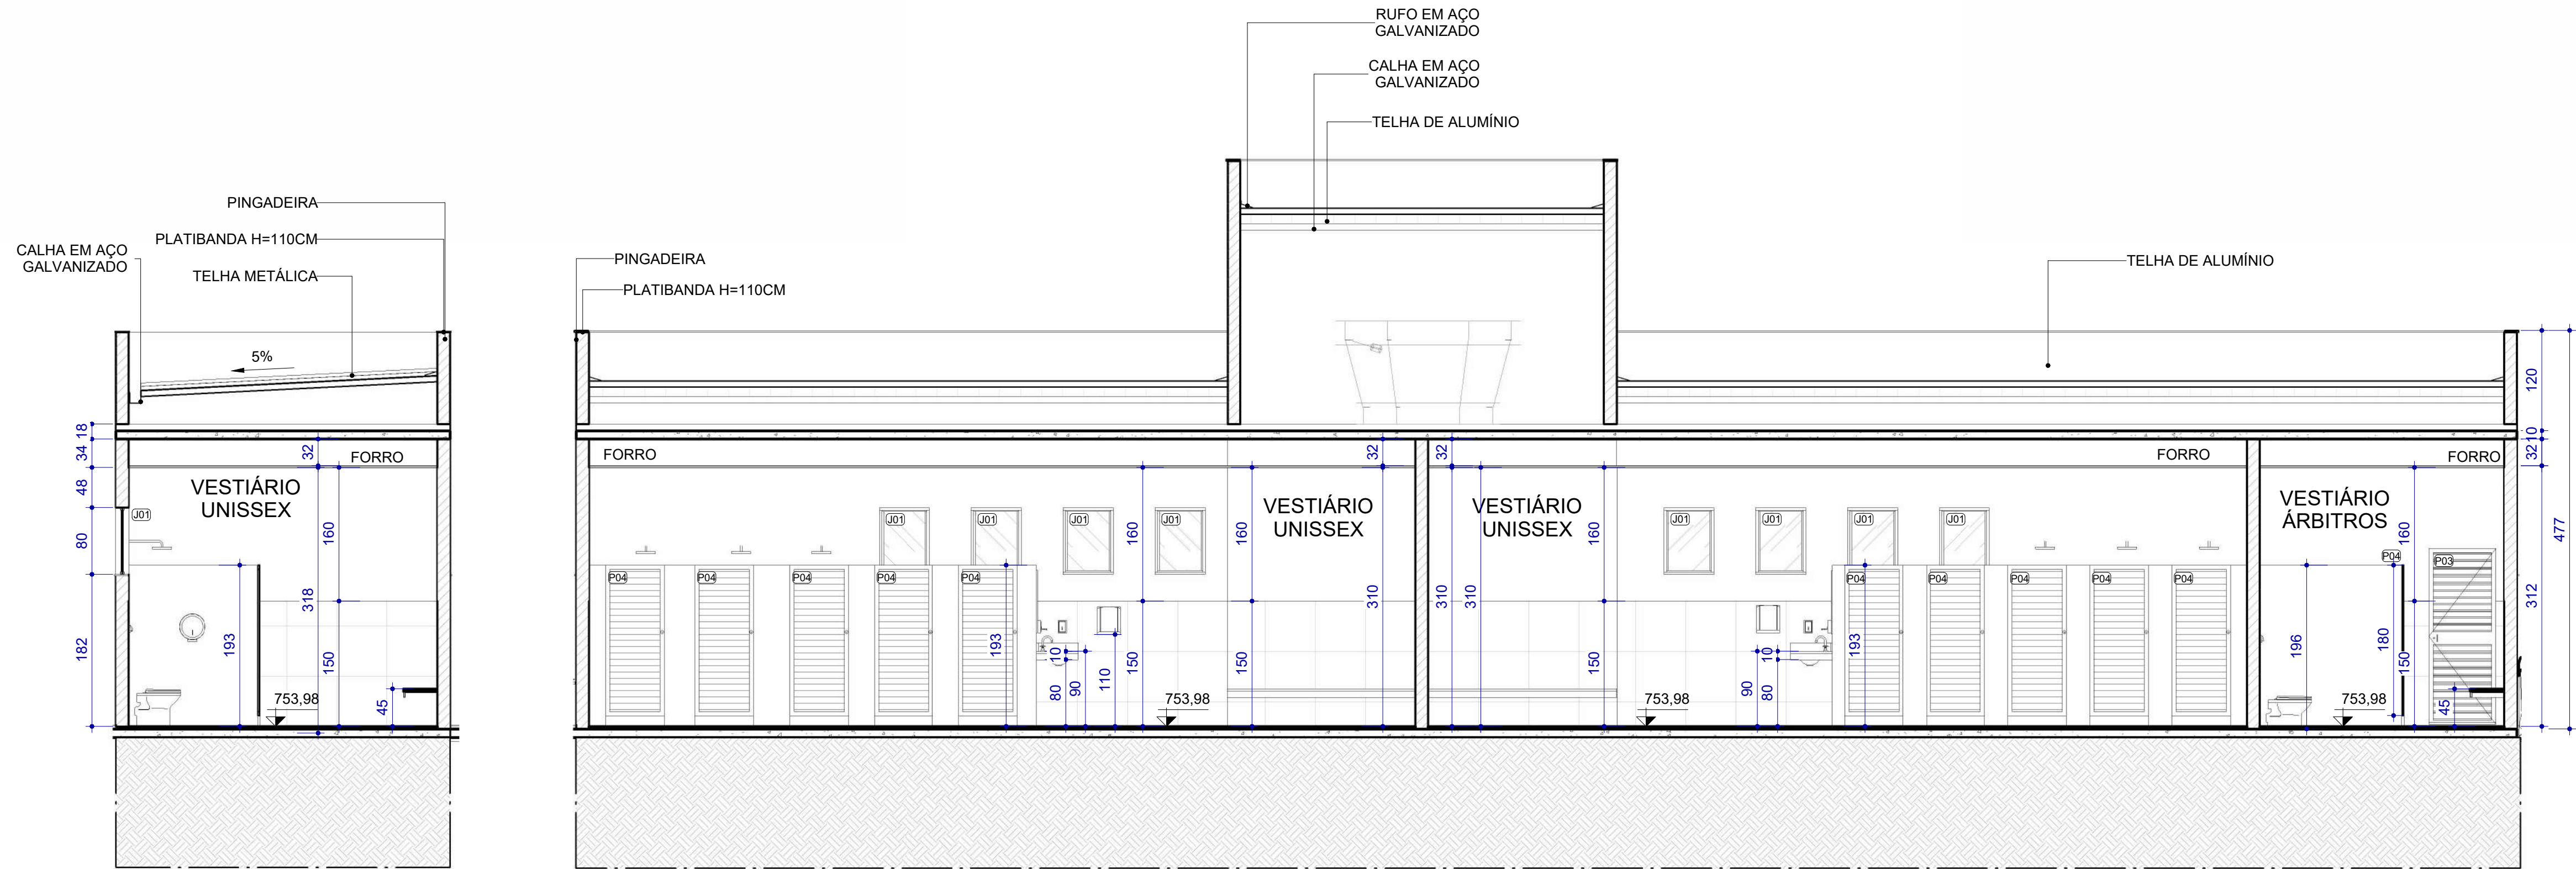


LEGENDA ESPECIFICAÇÕES						
						
	PISO					
	TETO					
	PAREDE					
	DIVERSOS					
QUADRO GERAL DE ESPECIFICAÇÕES - TETO						
CÓD.	TETOS					
01	FORRO EM GESSO COM PINTURA EM TINTA ACRÍLICA NA COR BRANCO NEVE					
02	PINTURA EM TETO COM TINTA ACRÍLICA NA COR BRANCO NEVE					
QUADRO GERAL DE ESQUADRIAS - PORTAS						
CÓD.	LARGURA	ALTURA	ABERTURA E NÚM. FOLHAS	MATERIAL/ACABAMENTO	QNTD.	
P03	80	210	ABRIR, 1 FOLHA	PORTA VENEZIANA COM PERFIL EM ALUMÍNIO ANODIZADO NA COR NATURAL	3	
P04	70	180	ABRIR, 1 FOLHA	PORTA VENEZIANA DE ALUMÍNIO	12	
QUADRO GERAL DE ESQUADRIAS - JANELAS						
CÓD.	LARGURA	ALTURA	ALTURA PEITORIL	ABERTURA E NÚM. FOLHAS	MATERIAL/ACABAMENTO	QNTD.
J01	60	80	180	ABRIR, 1 FOLHA	JANELA EM VIDRO LISO, COMUM, INCOLOR, E=6MM, PERFIS DE ALUMÍNIO COR NATURAL	16

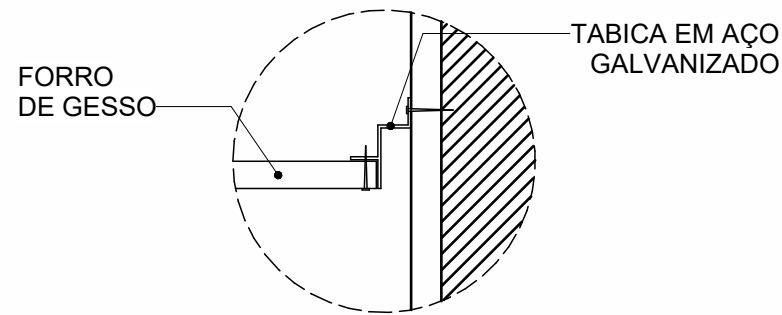


5 DET. TABICA FORRO DE GESSO
ESCALA: 1 : 5

C NOVA CONSTRUÇÃO VESTIÁRIO - CORTE CC
ESCALA: 1 : 50

D NOVA CONSTRUÇÃO VESTIÁRIO - CORTE DD
ESCALA: 1 : 50

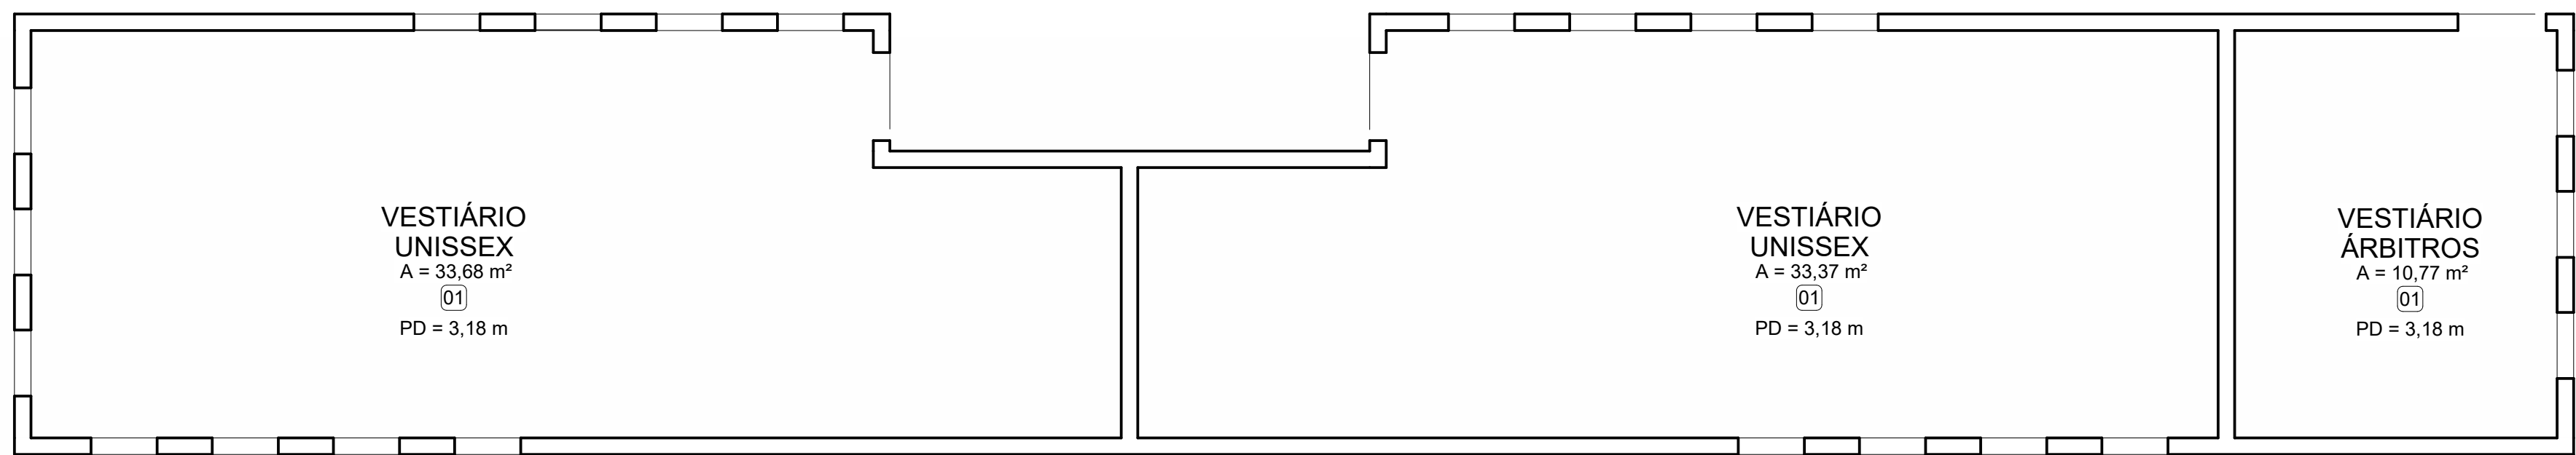


3 PLANTA DE FORRO - VESTIÁRIO
ESCALA: 1 : 50

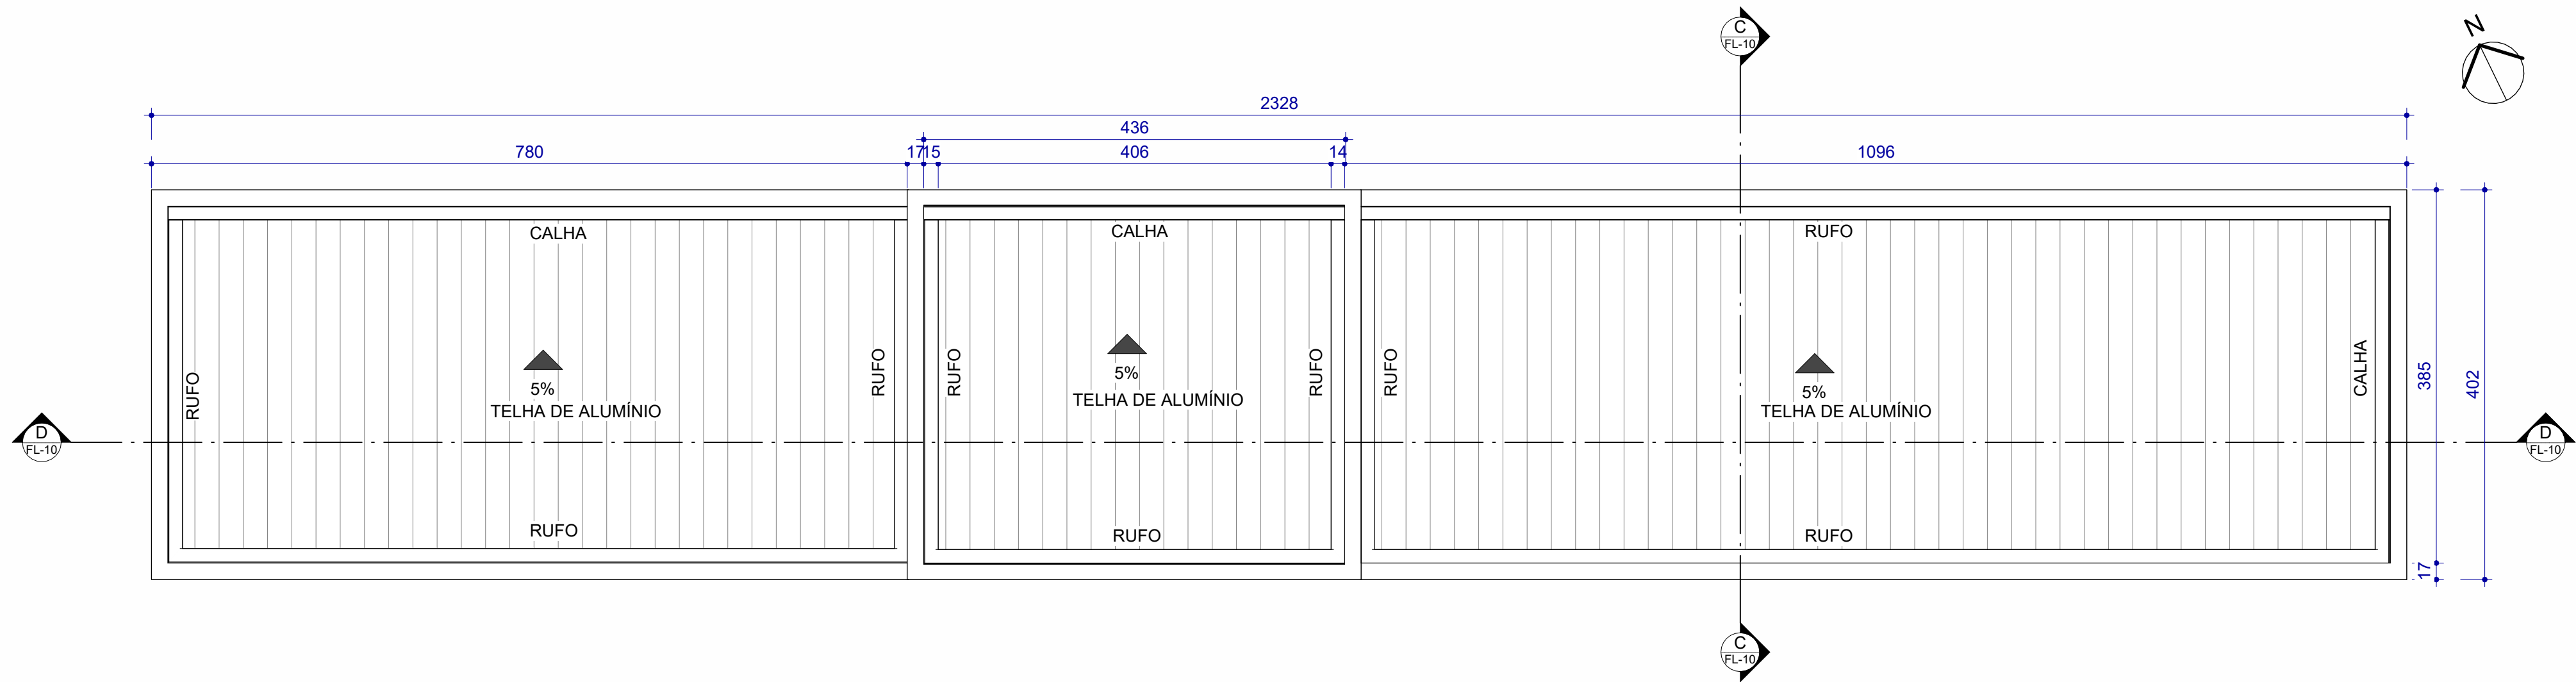


4 PLANTA DE COBERTURA - VESTIÁRIO
ESCALA: 1 : 50

QUADRO GERAL DE ESQUADRIAS - JANELAS						
CÓD.	LARGURA	ALTURA	ALTURA PEITORIL	ABERTURA E NÚM. FOLHAS	MATERIAL/ACABAMENTO	QNTD.
J01	60	80	180	ABRIR, 1 FOLHA	JANELA EM VIDRO LISO, COMUM, INCOLOR, E=6MM, PERFIS DE ALUMÍNIO COR NATURAL	22
J02	60	80		ABRIR, 1 FOLHA	PORTINHOLA DE ALUMÍNIO/ALÇAPÃO	1
QUADRO GERAL DE ESQUADRIAS - PORTAS						
CÓD.	LARGURA	ALTURA	ABERTURA E NÚM. FOLHAS	MATERIAL/ACABAMENTO	QNTD.	
P03	80	210	ABRIR, 1 FOLHA	PORTA VENEZIANA COM PERFIL EM ALUMÍNIO ANODIZADO NA COR NATURAL	3	
P04	70	180	ABRIR, 1 FOLHA	PORTA VENEZIANA DE ALUMÍNIO	12	

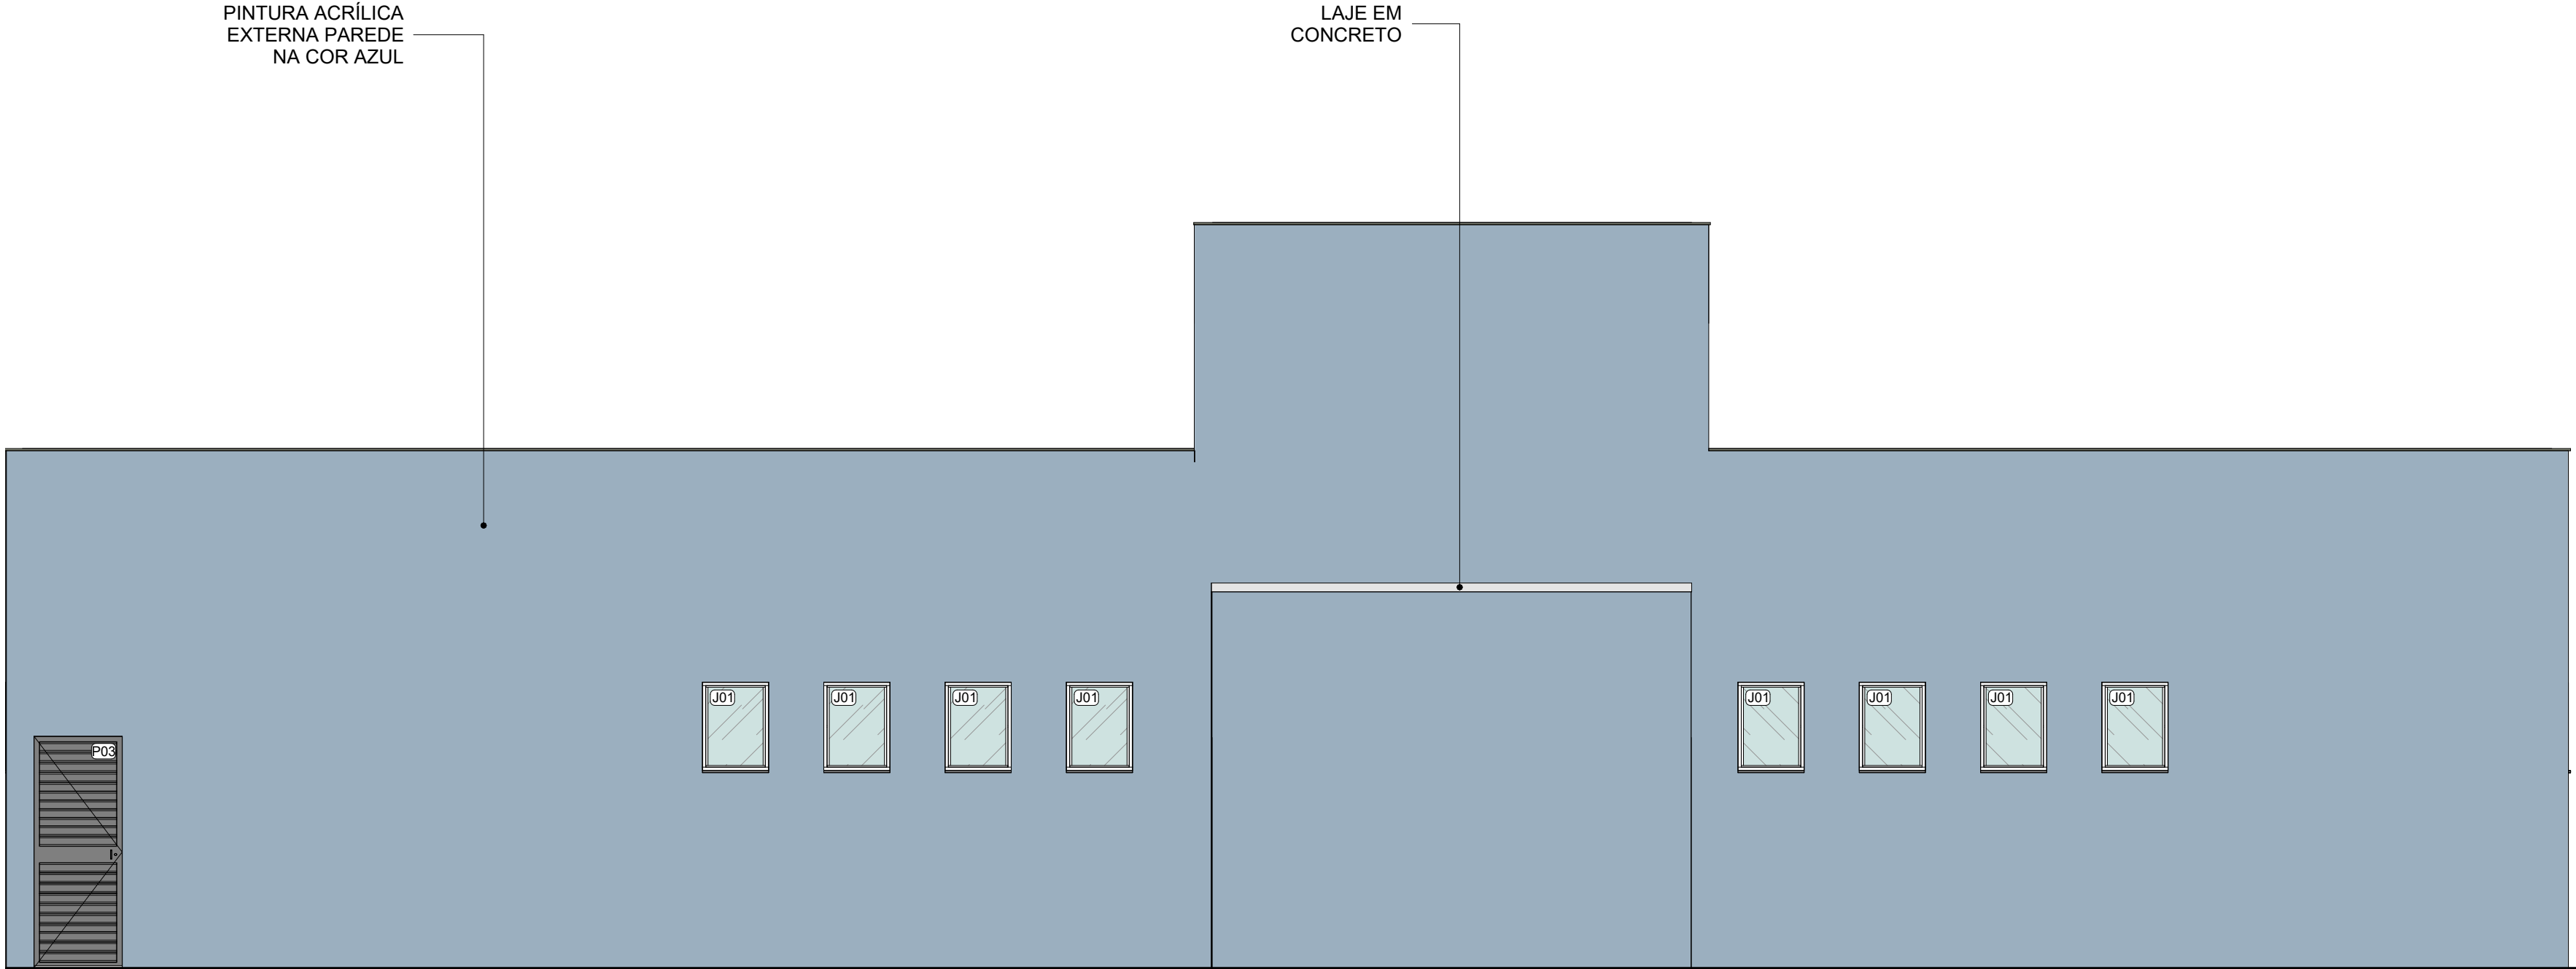


1 FACHADA FRONTAL - VESTIÁRIO

ESCALA: 1 : 50

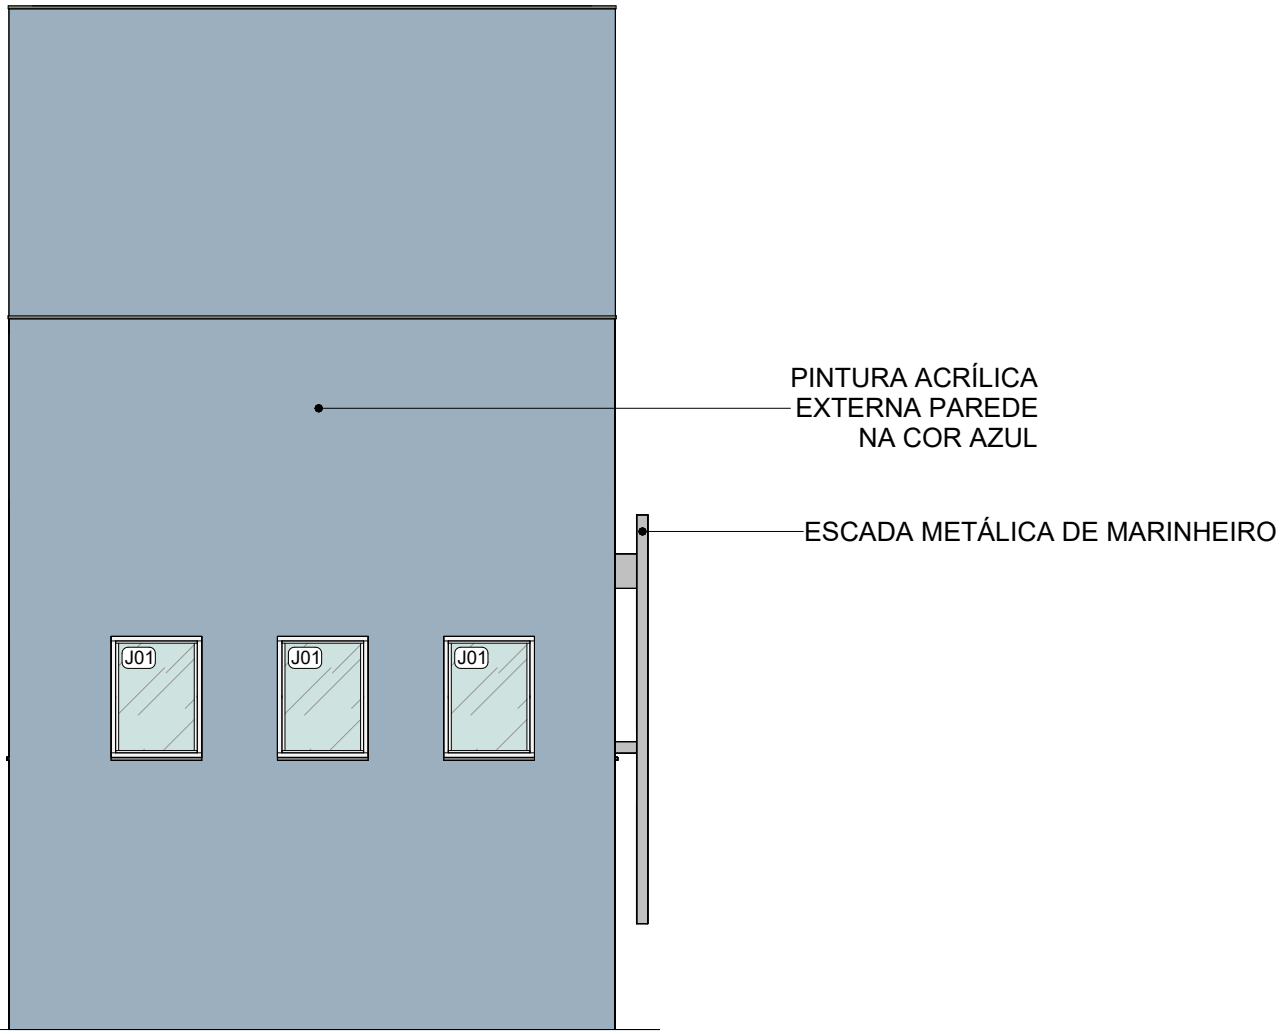


2 FACHADA LATERAL DIREITA - VESTIÁRIO

ESCALA: 1 : 50

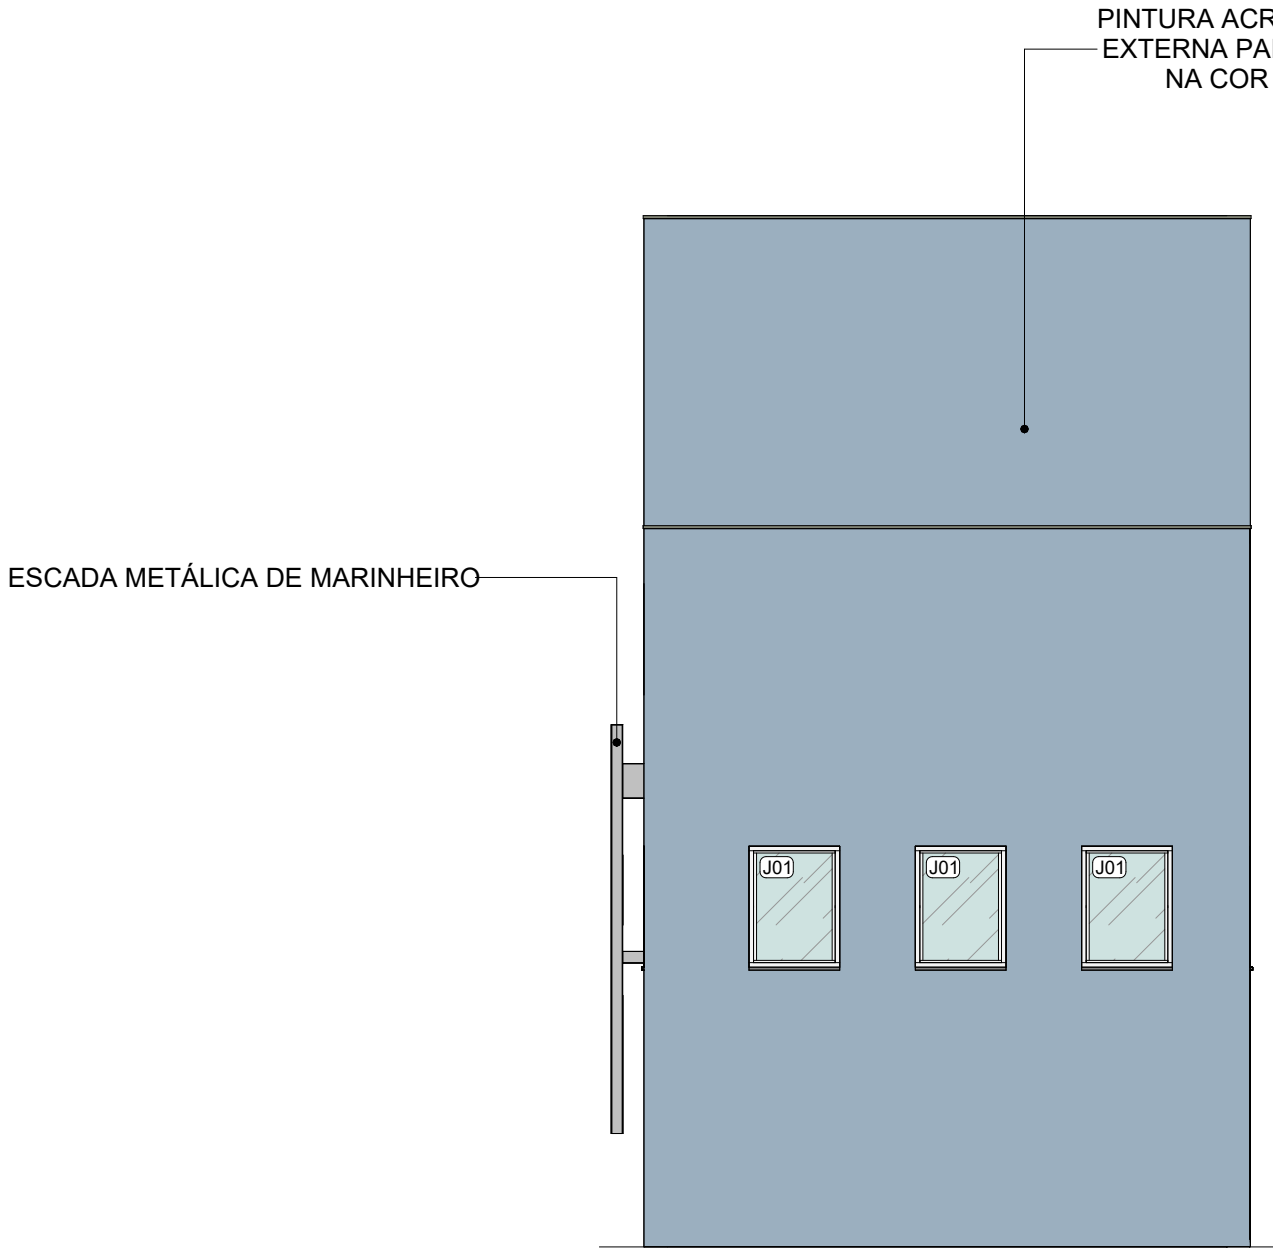


3 FACHADA LATERAL ESQUERDA - VESTIÁRIO

ESCALA: 1 : 50

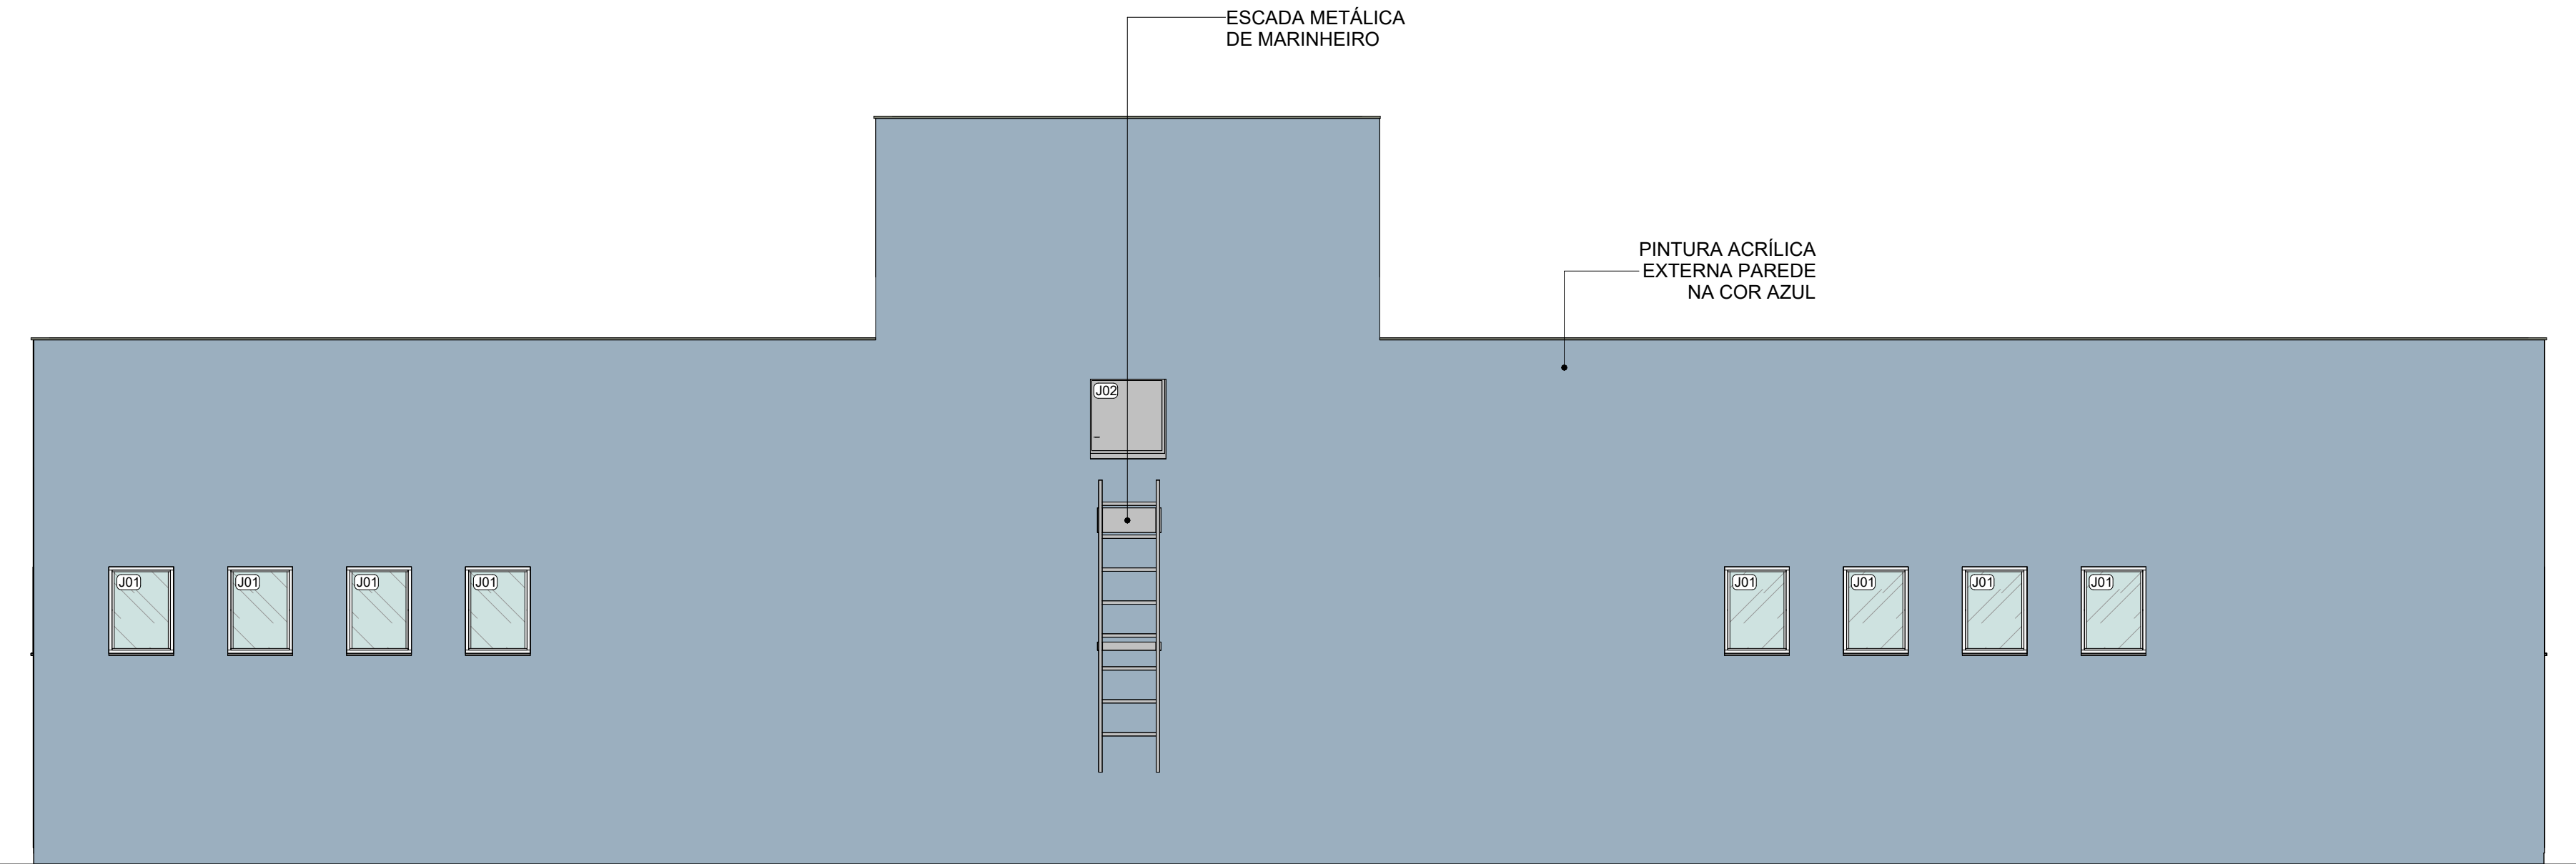


4 FACHADA POSTERIOR - VESTIÁRIO

ESCALA: 1 : 50

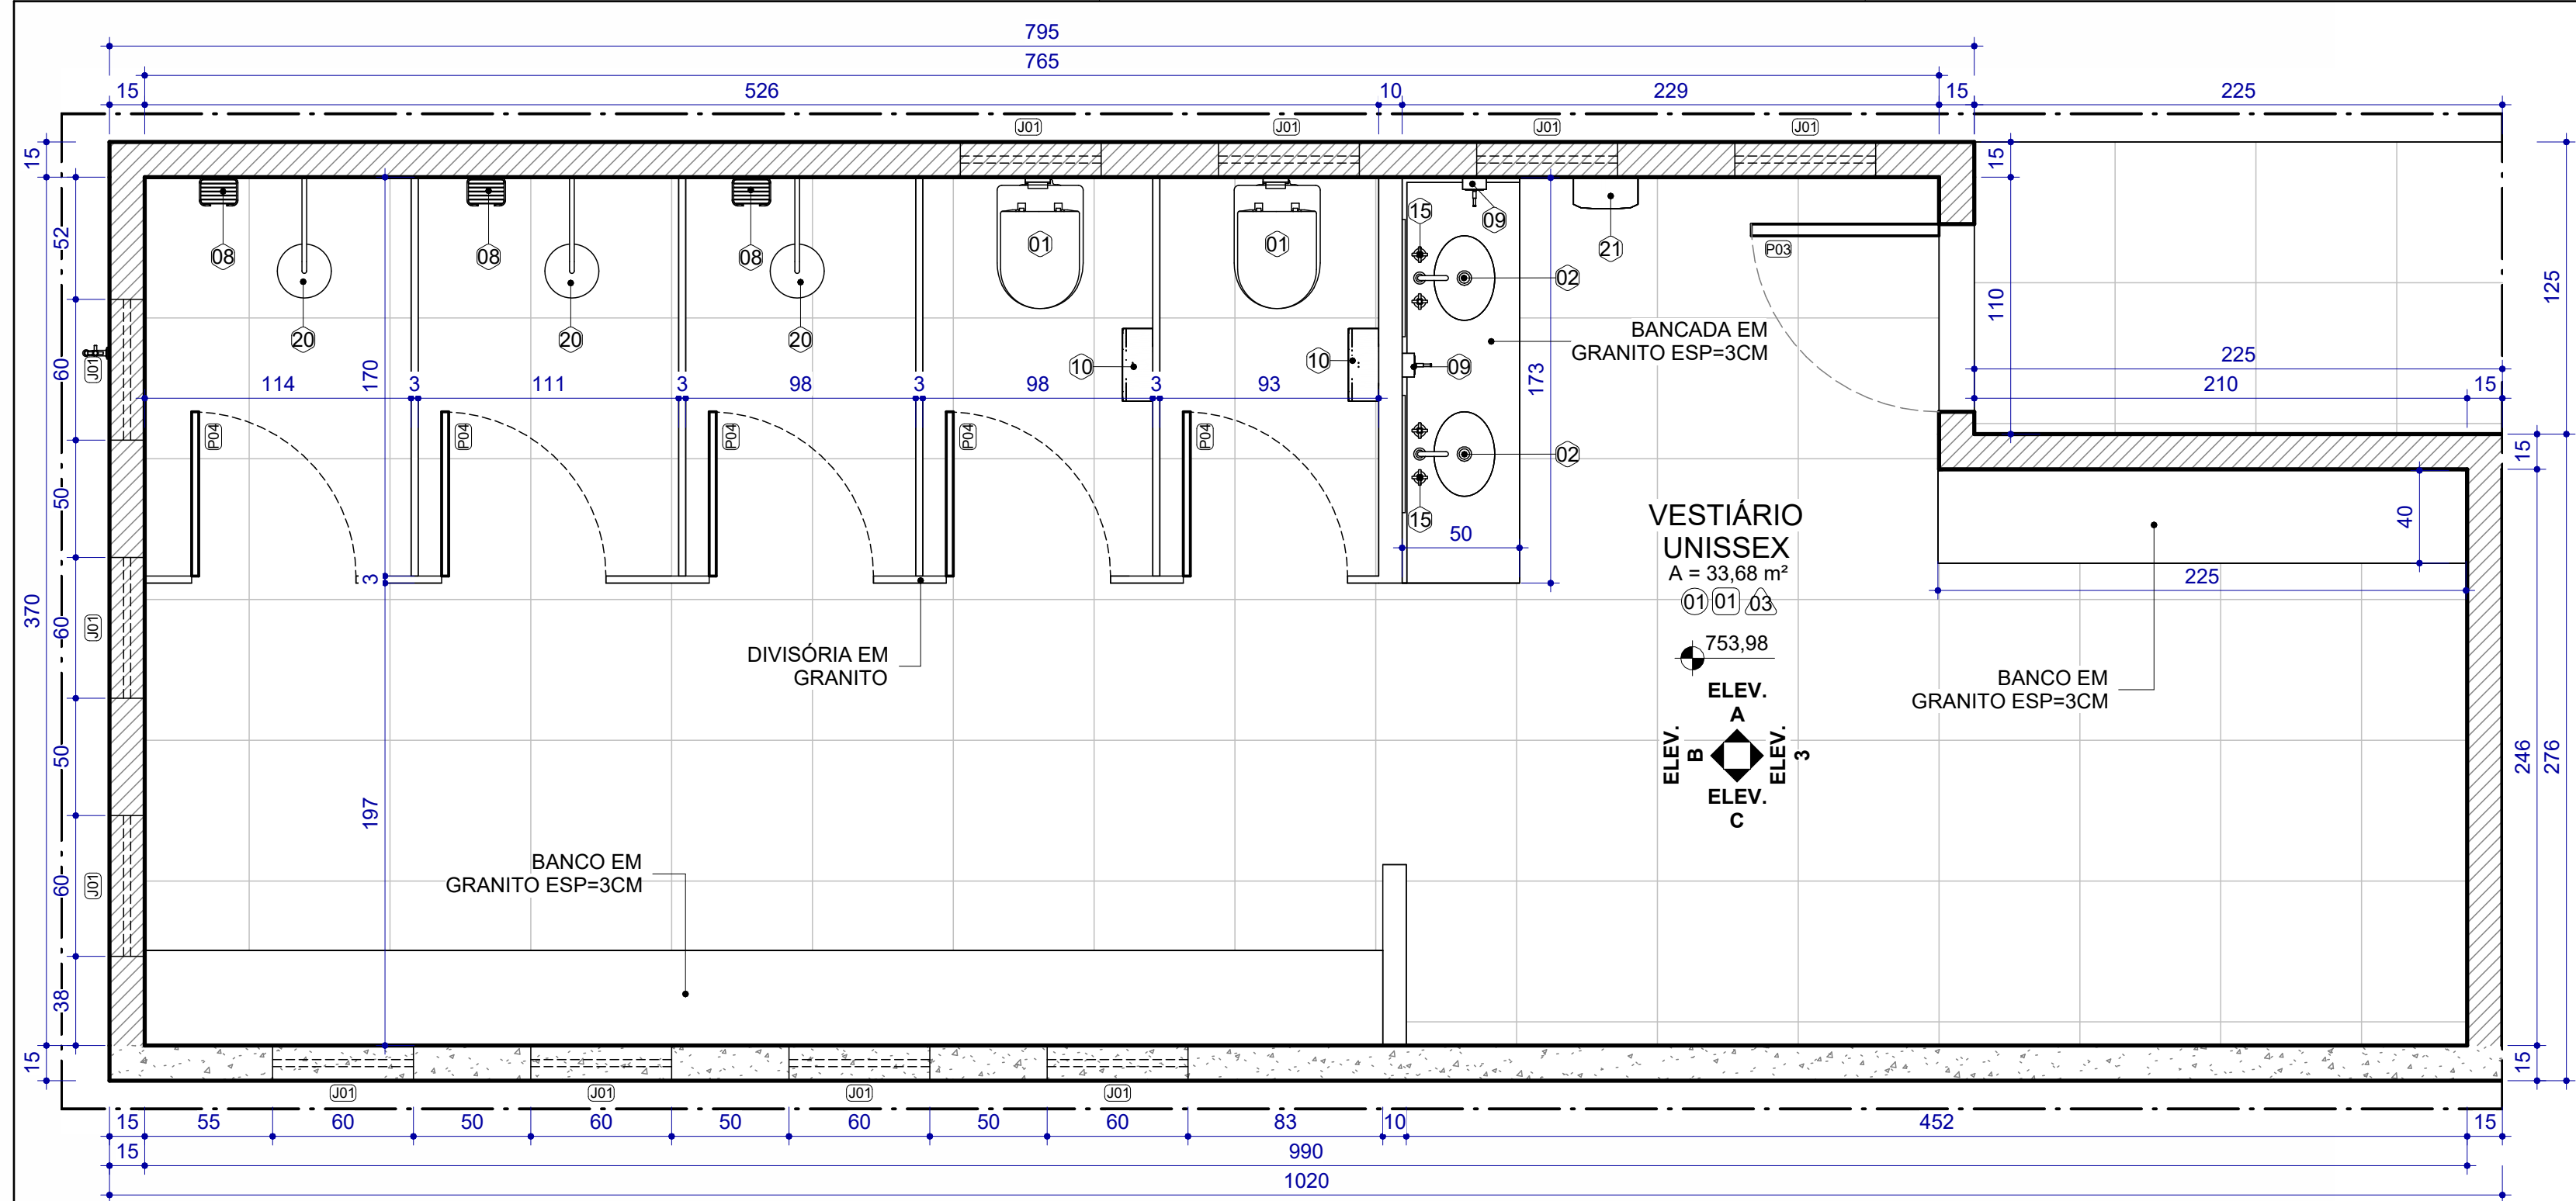


REFORMA - PLANTA - VESTIÁRIO UNISSEX

ESCALA: 1 : 25

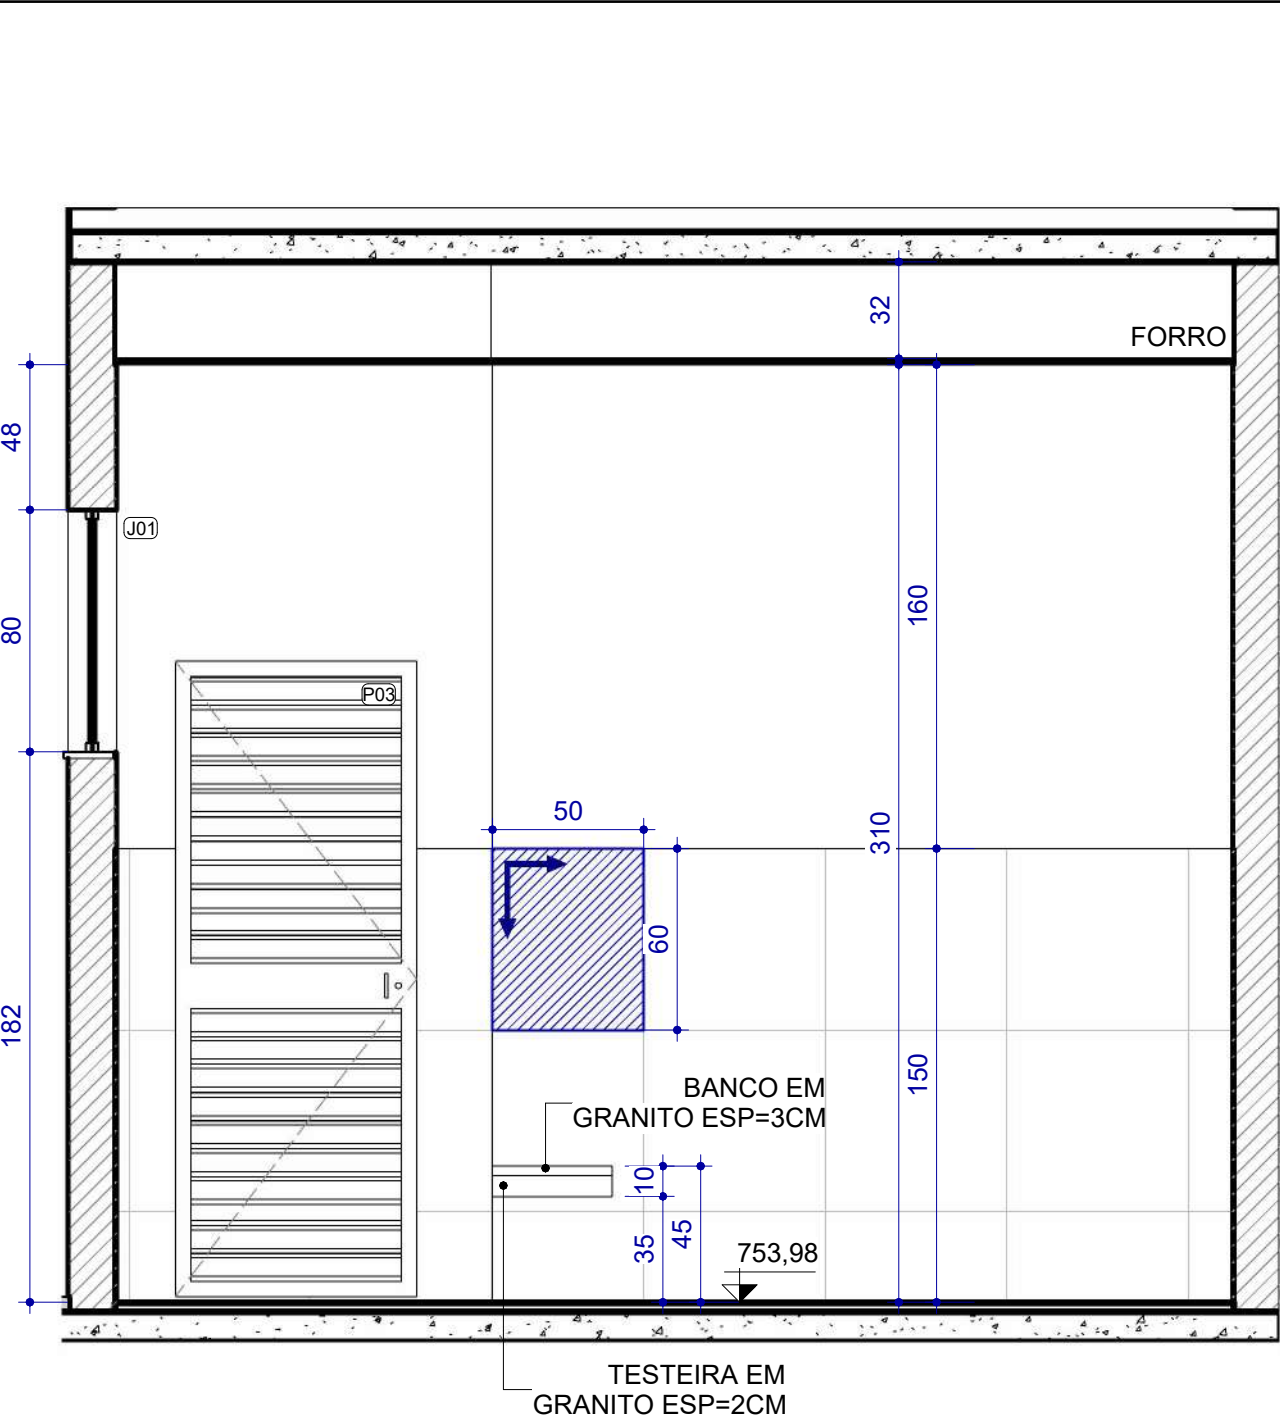


REFORMA - ELEVÇÃO B - VESTIÁRIO UNISSEX

ESCALA: 1 : 25

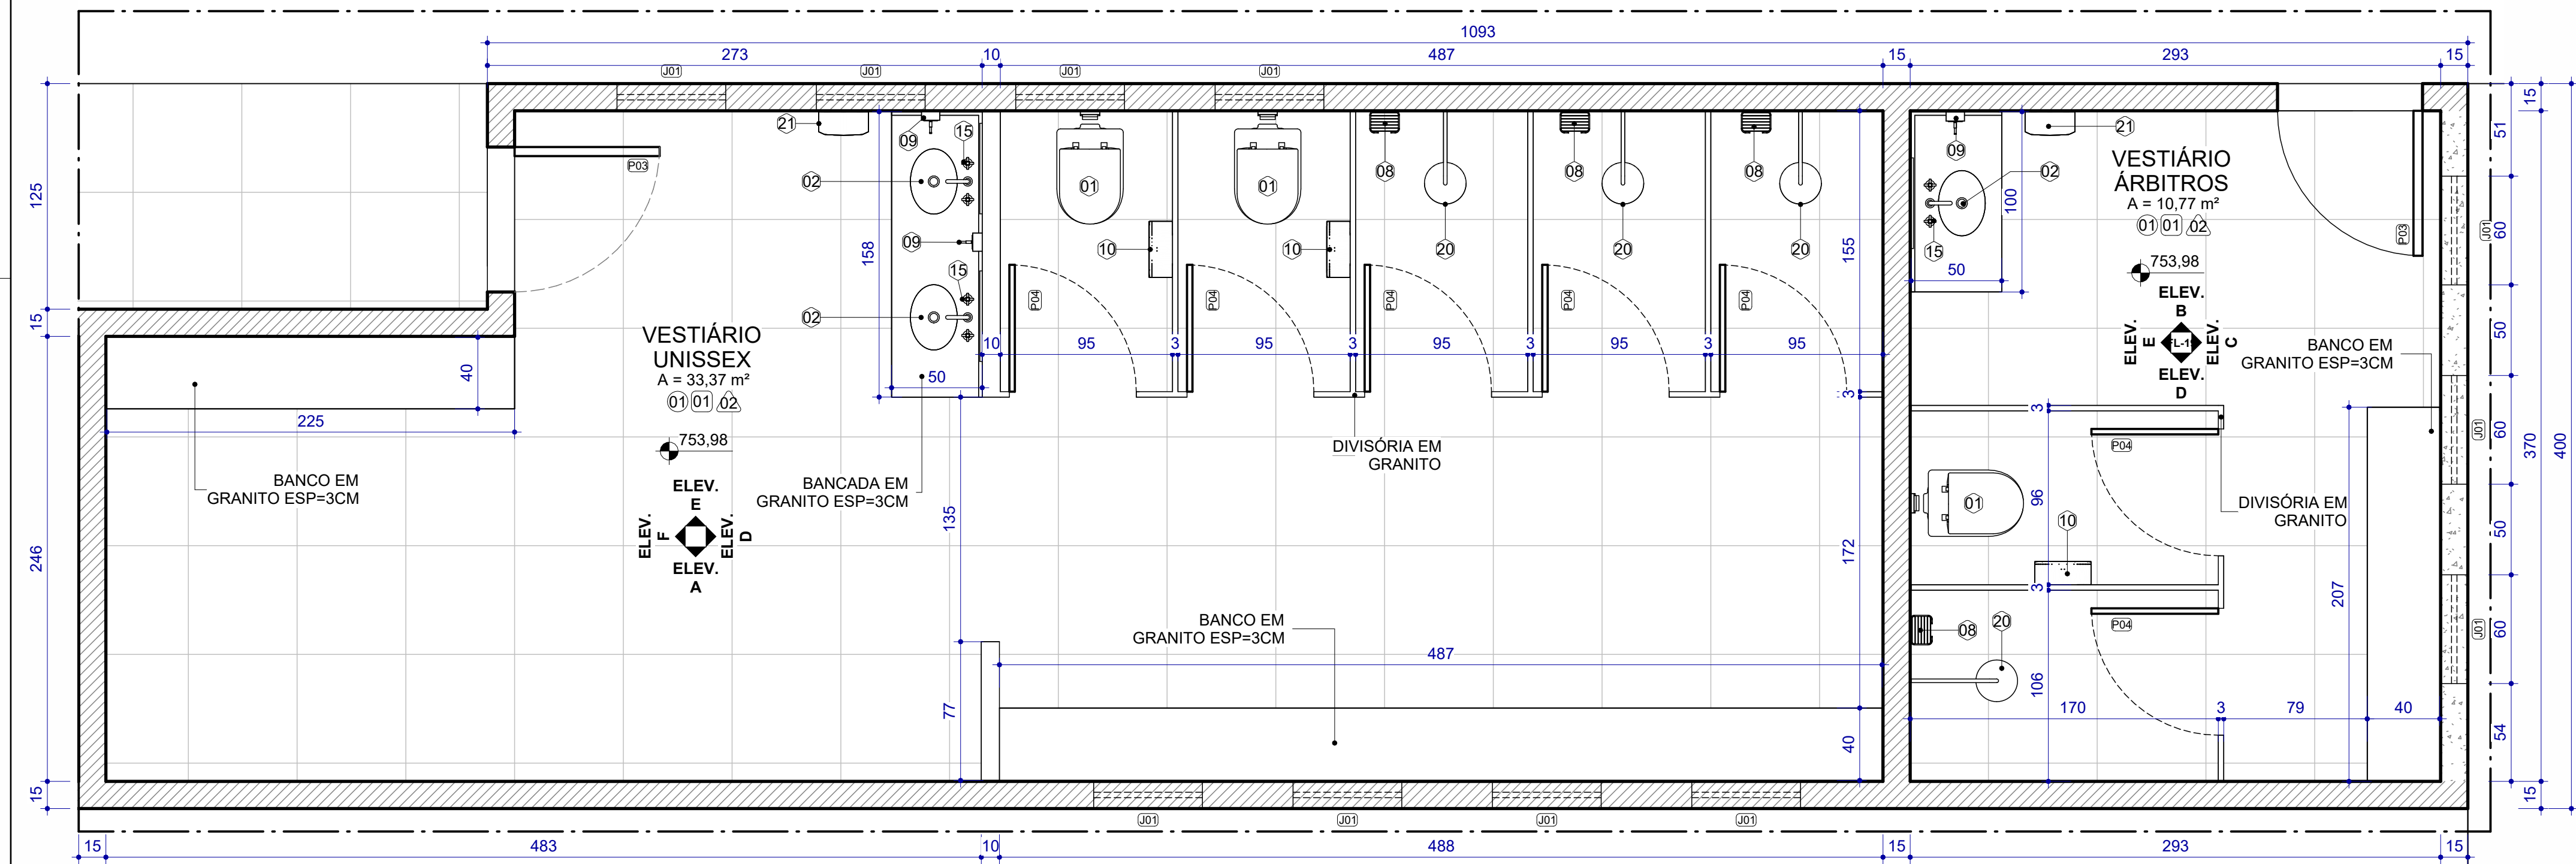


REFORMA - PLANTA - VESTIÁRIO E VESTIÁRIO ÁRBITROS

ESCALA: 1 : 25

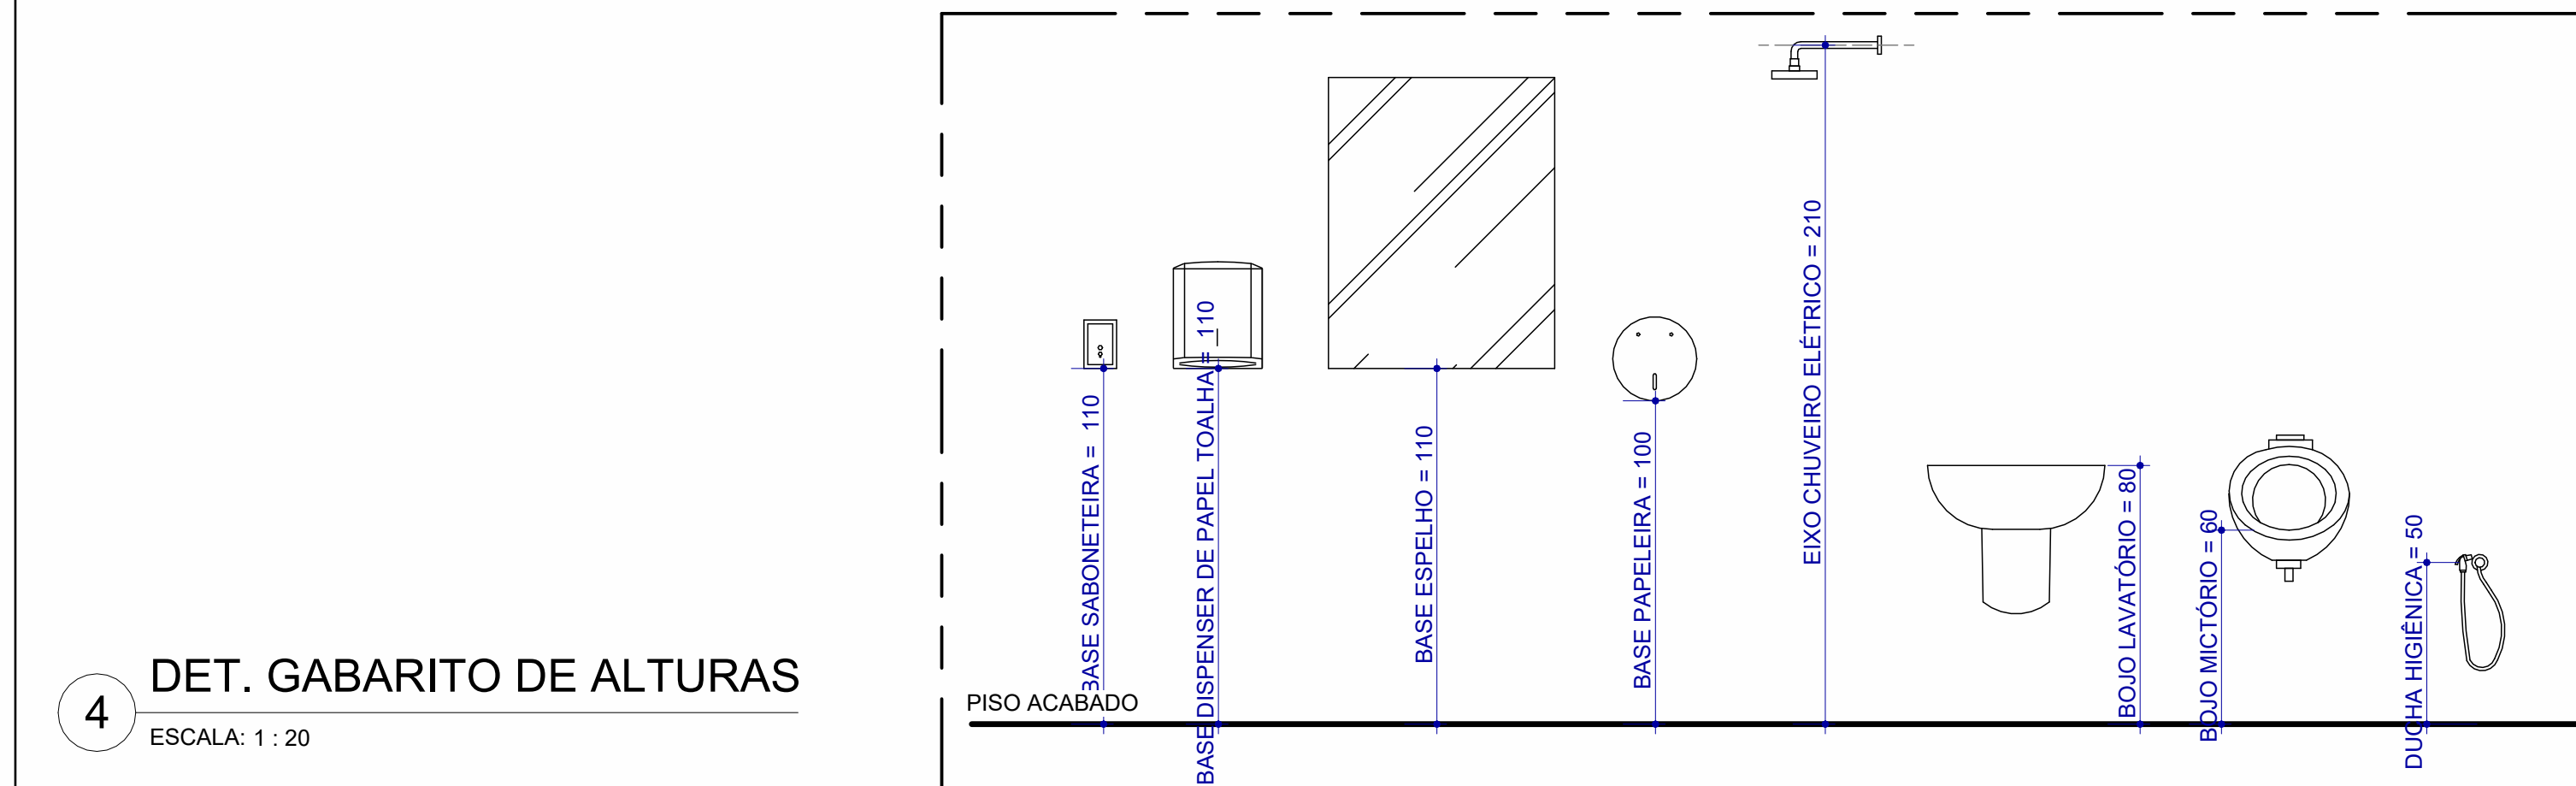


DET. GABARITO DE ALTURAS

ESCALA: 1 : 20

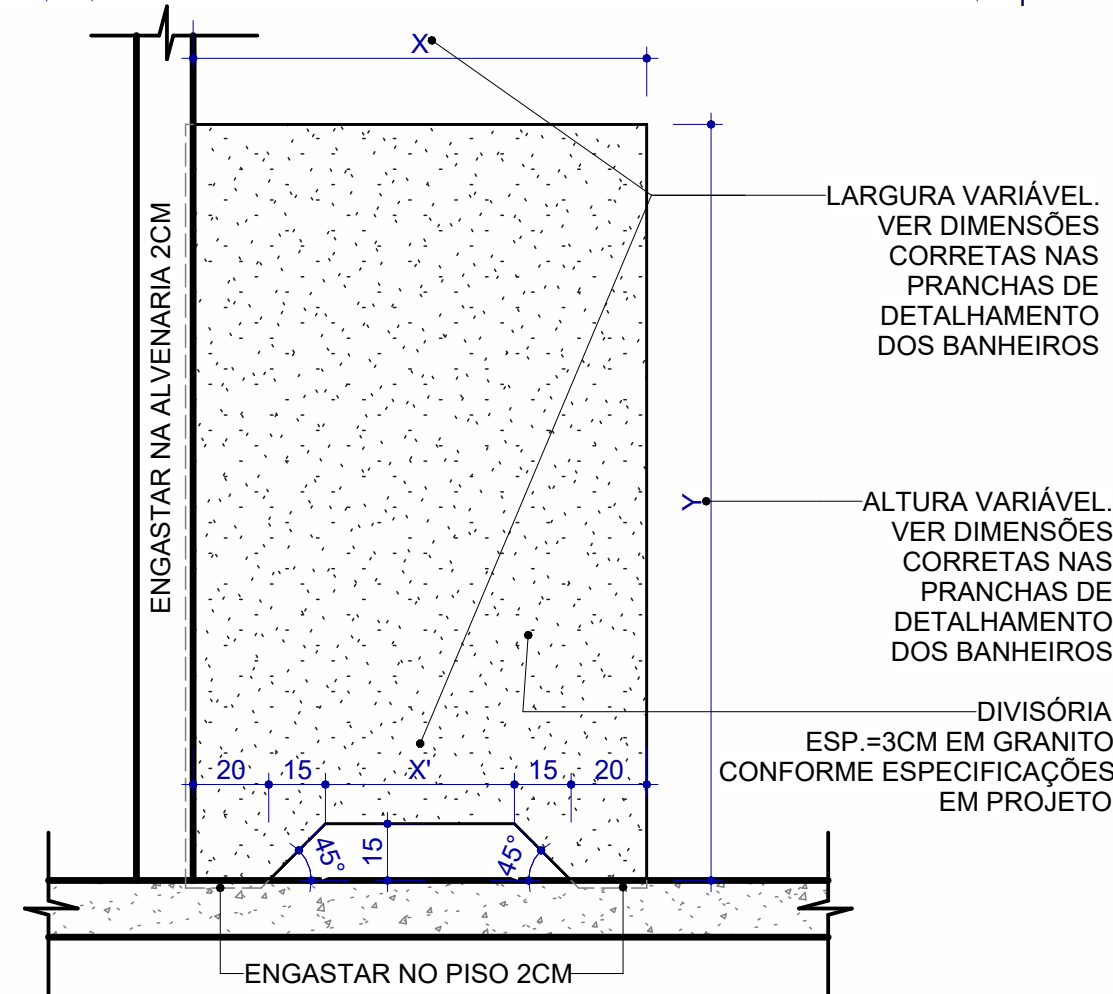

DET. DIVISÓRIA SANITÁRIA LATERAL


ESCALA: 1 : 20

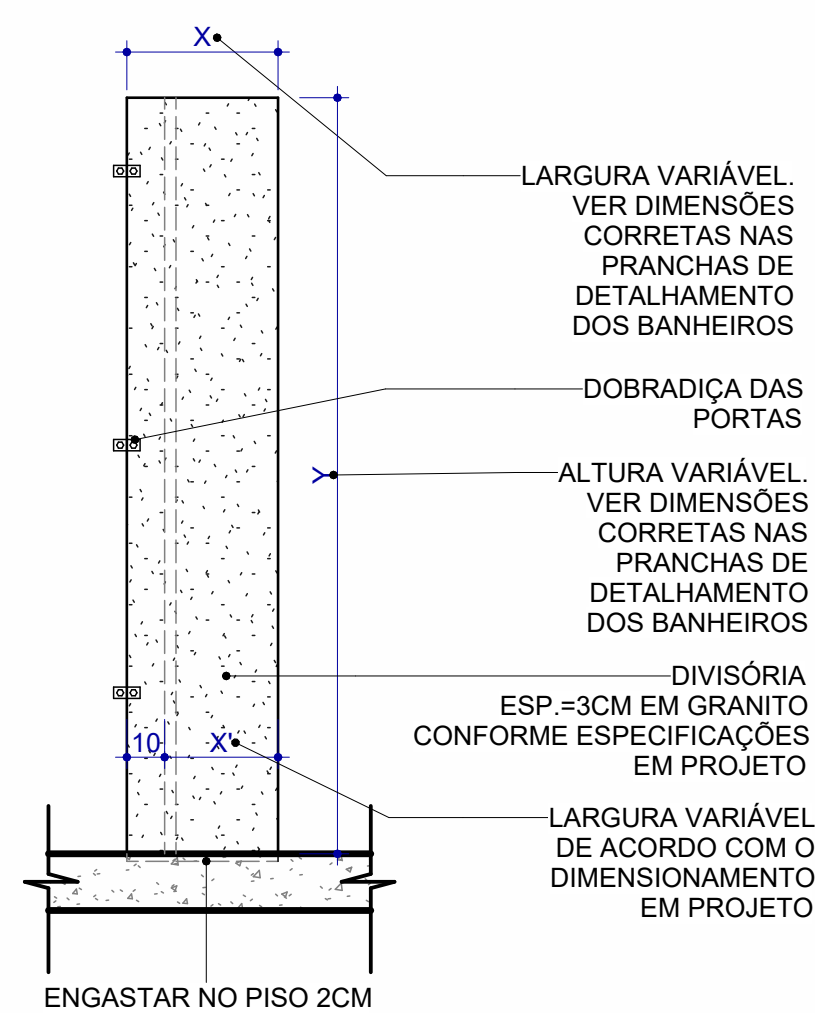


DET. DIVISÓRIA SANITÁRIA FRONTAL

ESCALA: 1 : 20


LEGENDA PAGINAÇÃO DE PISO											
	INÍCIO E SENTIDO DA PAGINAÇÃO DE PISO E REVESTIMENTOS										
LEGENDA ESPECIFICAÇÕES											
	PISO			TETO			PAREDE			DIVERSOS	
QUADRO GERAL DE ESPECIFICAÇÕES - ACABAMENTOS											
CÓD.	PISO / SUPERFÍCIES HORIZONTAIS										
01	PISO EM CERÂMICA 60X60CM NA COR BRANCO										
QUADRO GERAL DE ESPECIFICAÇÕES - PAREDE											
CÓD.	VEDAÇÕES / REVESTIMENTOS / ELEMENTOS VERTICAIS										
02	REVESTIMENTO EM CERÂMICA 60X60CM NA COR BRANCO ATÉ 150CM DE ALTURA DO PISO, SEGUIDA DE PINTURA ACRILICA NA COR BRANCO NEVE ATÉ O FORRO										
03	REVESTIMENTO EM CERÂMICA 60X60CM NA COR BRANCO ATÉ O TETO;										
04	REVESTIMENTO EM PINTURA ACRILICA, COR AZUL CÉU NUBLADO										
05	REVESTIMENTO EM PINTURA ACRILICA, COR BRANCO										
QUADRO GERAL DE ESPECIFICAÇÕES - TETO											
CÓD.	TETOS										
01	FORRO EM GESSO COM PINTURA EM TINTA ACRILICA NA COR BRANCO NEVE										
02	PINTURA EM TETO COM TINTA ACRILICA NA COR BRANCO NEVE										
QUADRO GERAL DE ESQUADRIAS - JANELAS											
CÓD.	LARGURA	ALTURA	ALTURA PEITORIL	ABERTURA E NÚM. FOLHAS	MATERIAL/ACABAMENTO				QNTD.		
J01	60	80	180	ABRIR, 1 FOLHA	JANELA EM VIDRO LISO, COMUM, INCOLOR, E=6MM, PERFIS DE ALUMÍNIO COR NATURAL				22		
QUADRO GERAL DE ESQUADRIAS - PORTAS											
CÓD.	LARGURA	ALTURA	ABERTURA E NÚM. FOLHAS	MATERIAL/ACABAMENTO				QNTD.			
P03	80	210	ABRIR, 1 FOLHA	PORTA VENEZIANA COM PERFIL EM ALUMÍNIO ANODIZADO NA COR NATURAL				3			
P04	70	180	ABRIR, 1 FOLHA	PORTA VENEZIANA DE ALUMÍNIO				12			
DIVERSOS											
CÓD.	MOBILIÁRIOS / PEÇAS HIDROSSANITÁRIAS / ACESSÓRIOS / DIVERSOS									QNTD.	
01	Bacia sanitária convencional									5	
02	CUBA DE EMBUTIR OVAL EM LOUÇA BRANCA, 35 X 50CM OU EQUIVALENTE									5	
07	VÁLVULA DE DESCARGA									5	
08	SABONETEIRA									7	
09	SABONETEIRA PLÁSTICA TIPO DISPENSER PARA SABONETE LÍQUIDO COM RESERVATÓRIO DE 800ML									5	
10	PAPELEIRA PLÁSTICA TIPO DISPENSER PARA PAPEL HIGIÊNICO ROLÃO									5	
15	TORNEIRA CROMADA DE MESA, COM MISTURADOR, 1/2 OU 3/4, PARA LAVATÓRIO									5	
20	CHUVEIRO									7	
21	DISPENSER EM PLÁSTICO PARA PAPEL TOALHA 2 OU 3 FOLHAS									3	
22	TORNEIRA CROMADA 1/2 OU 3/4 PARA TANQUE									1	
23	CAIXA D'ÁGUA DE POLIETILENO, 3000 L									1	

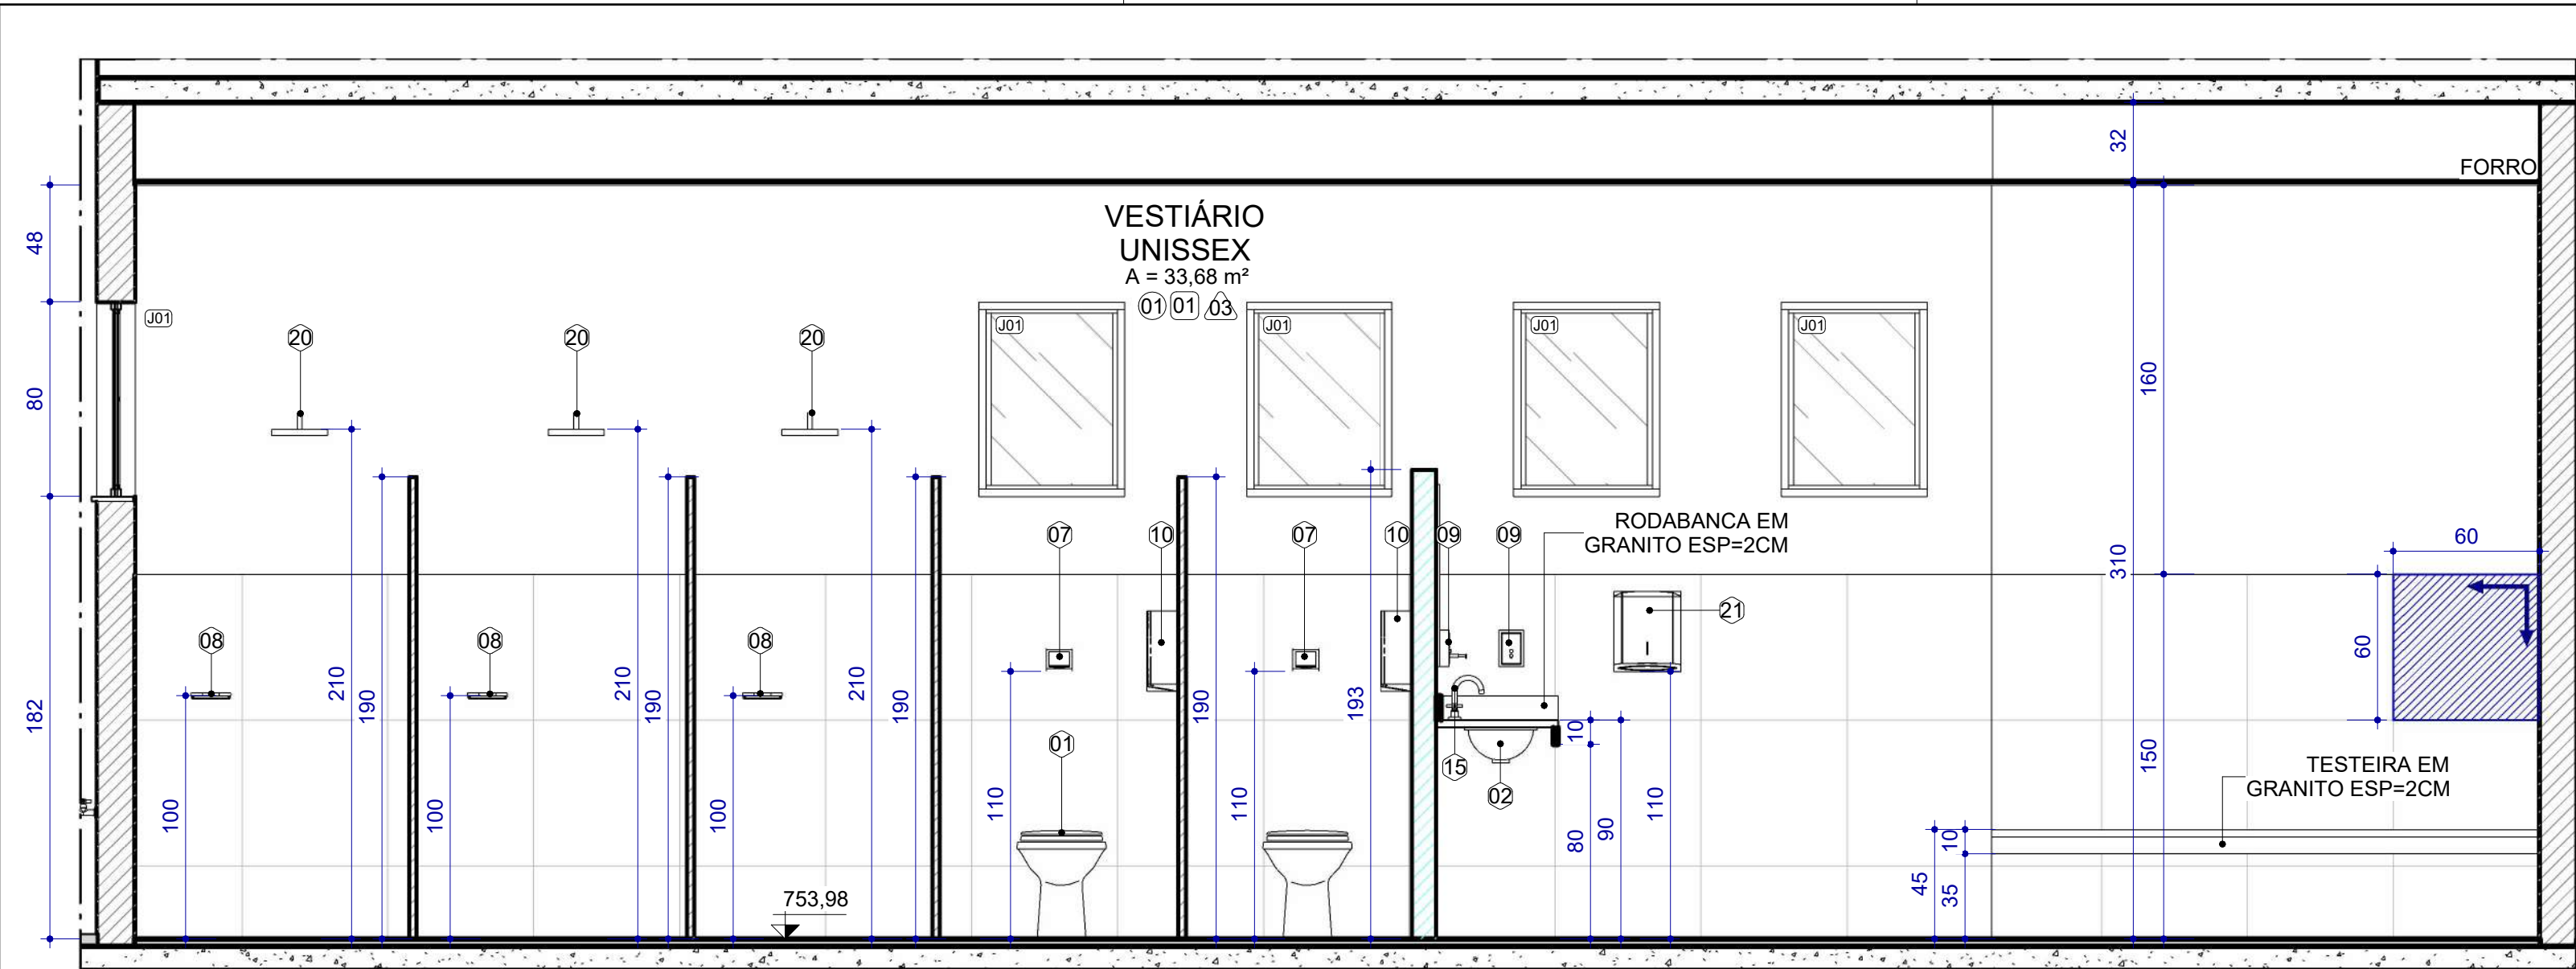


A REFORMA - ELEVAÇÃO A - VESTIÁRIO UNISSEX
ESCALA: 1 : 25

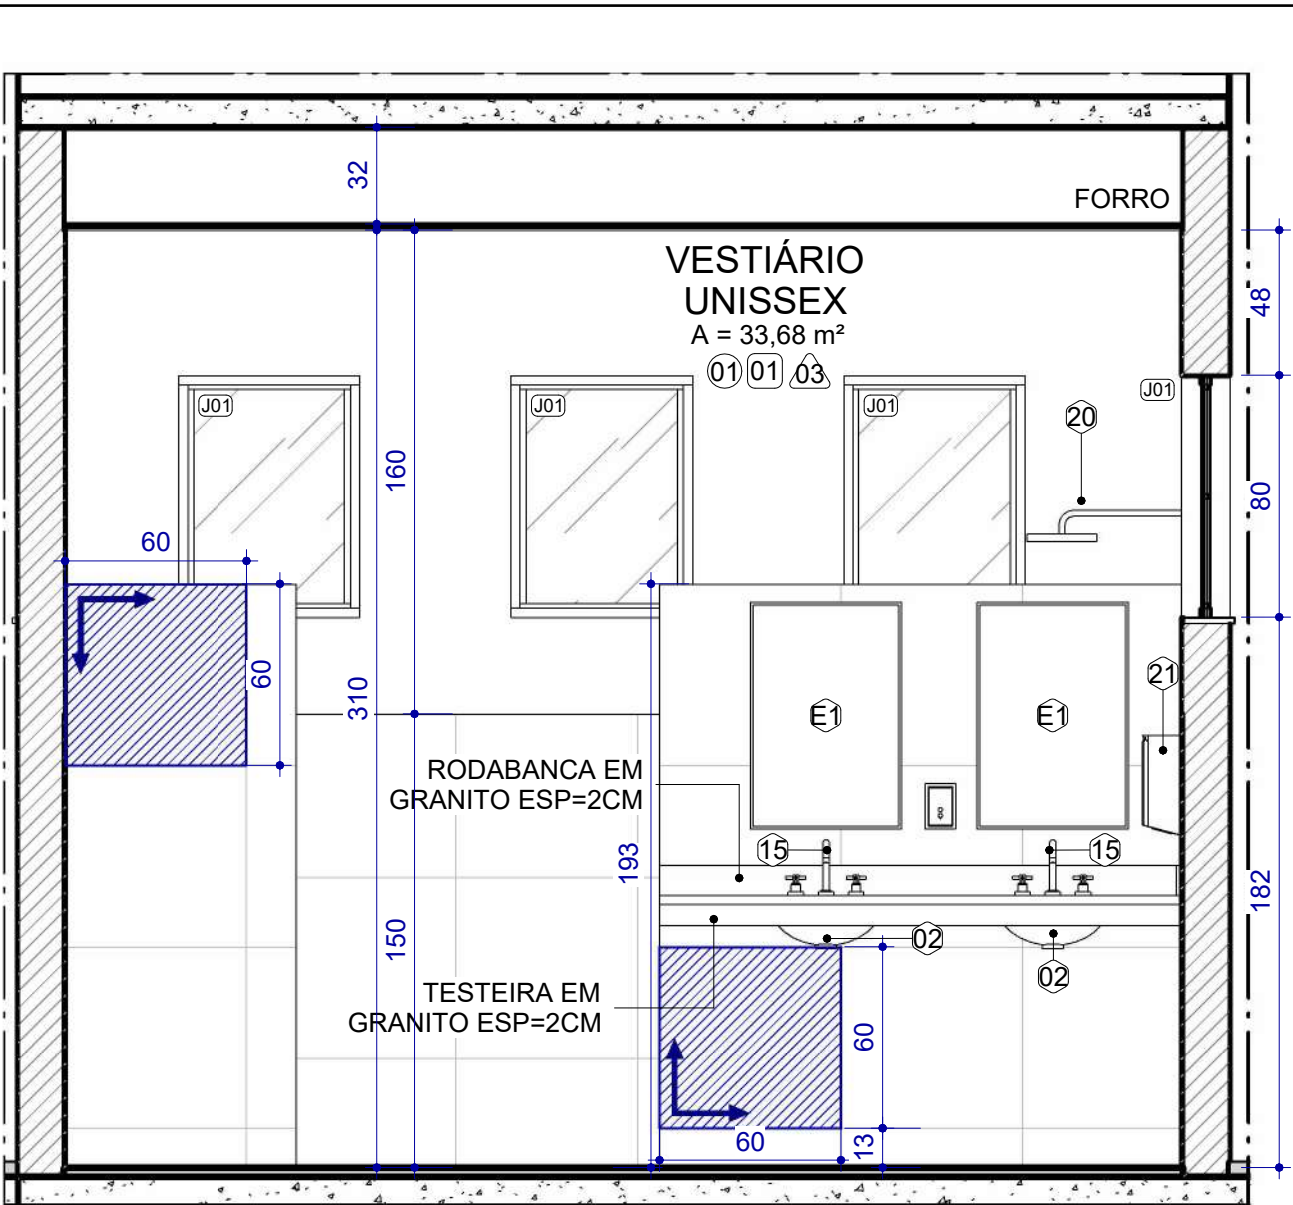


B REFORMA - ELEVAÇÃO D - VESTIÁRIO UNISSEX
ESCALA: 1 : 25

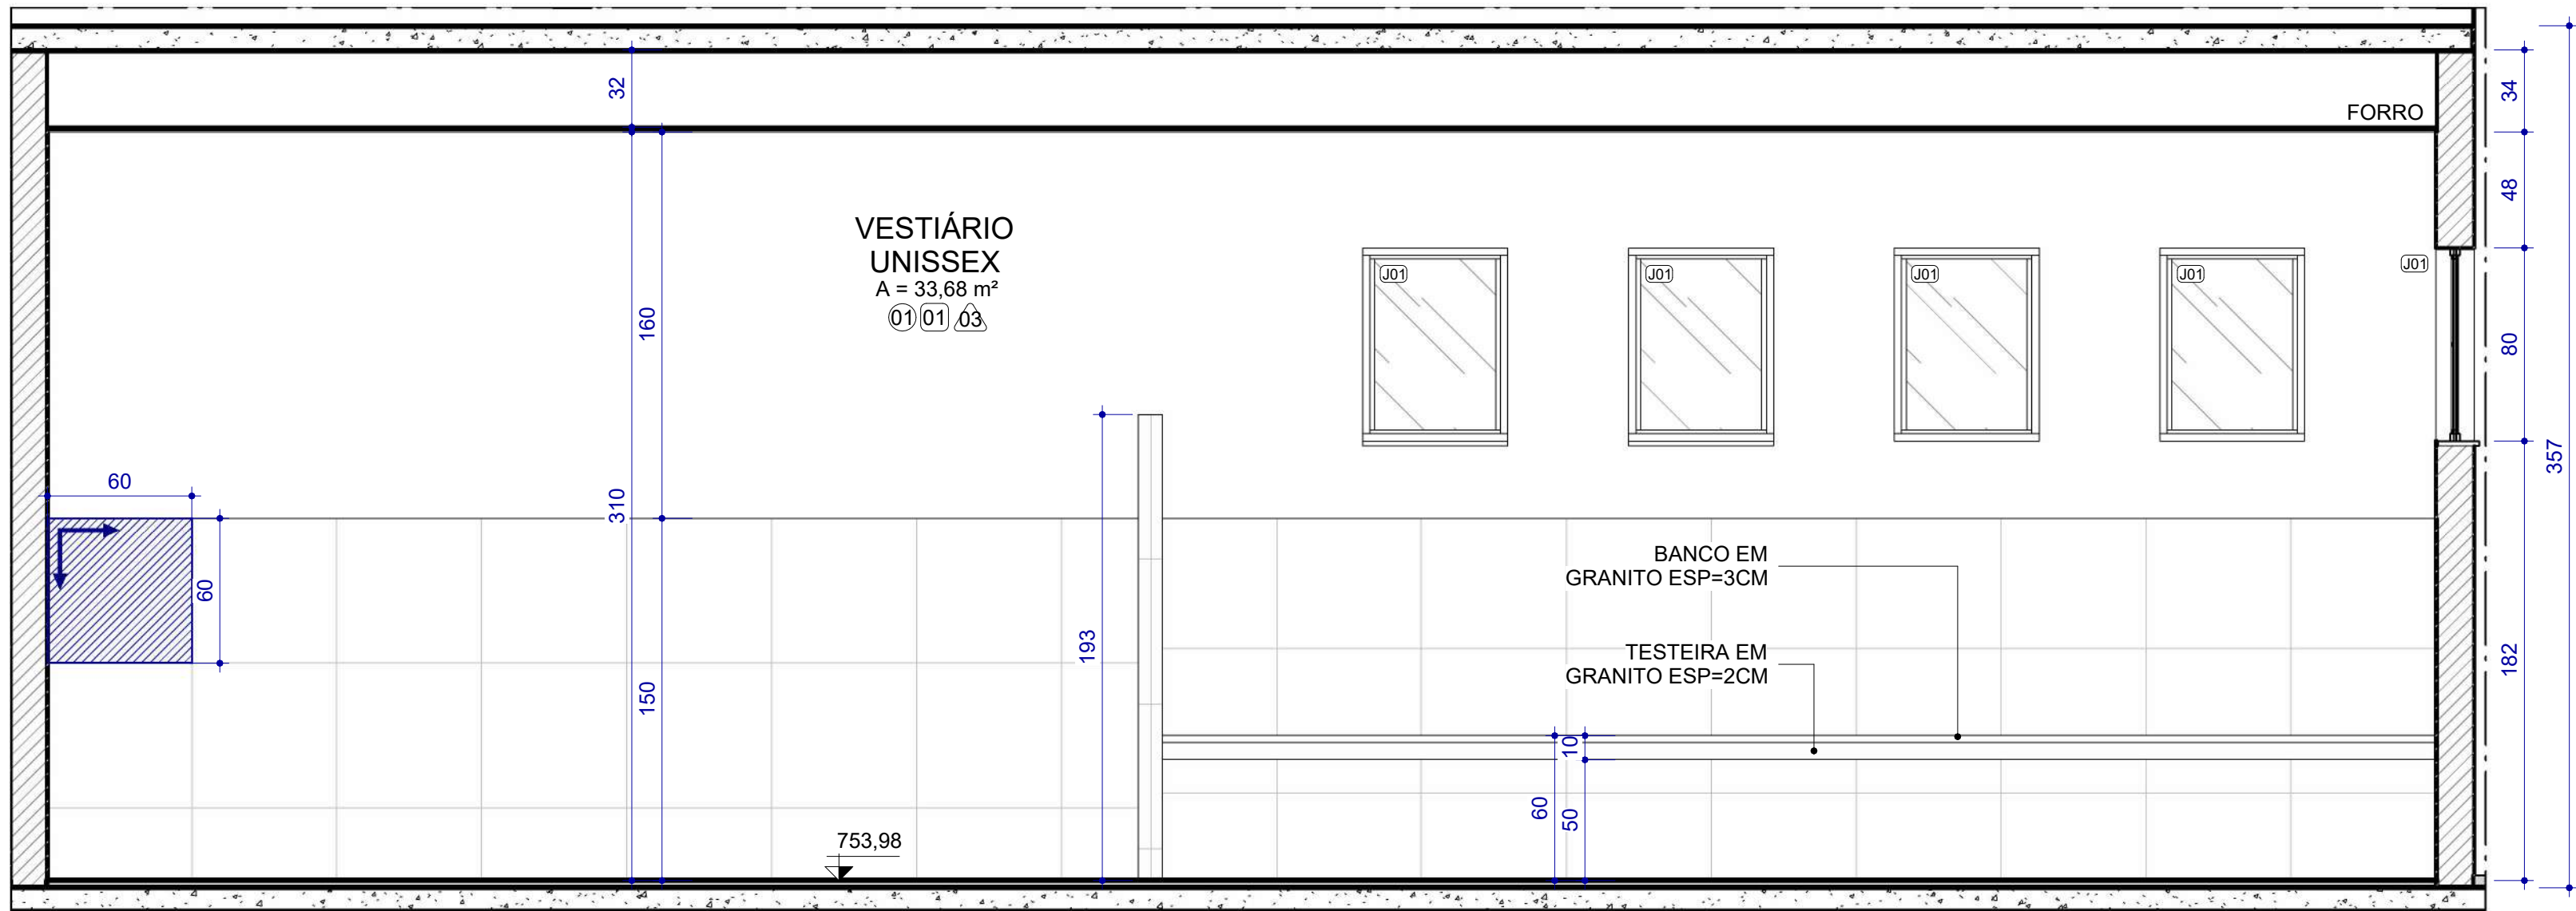


C REFORMA - ELEVAÇÃO C - VESTIÁRIO UNISSEX
ESCALA: 1 : 25

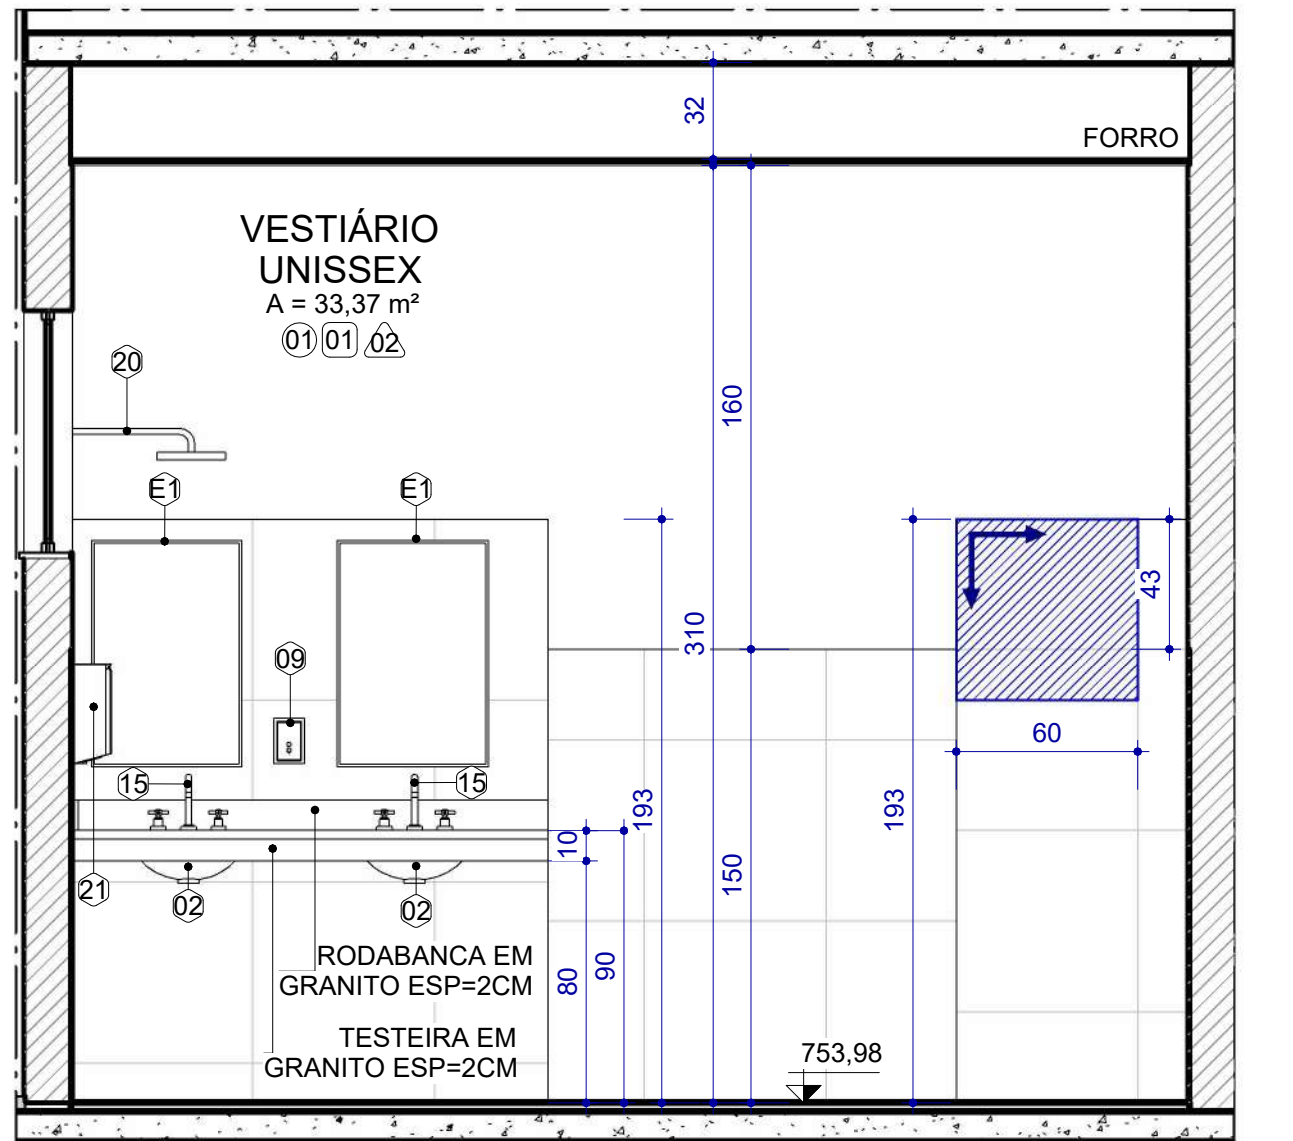

D REFORMA - ELEVAÇÃO B - VESTIÁRIO
ESCALA: 1 : 25

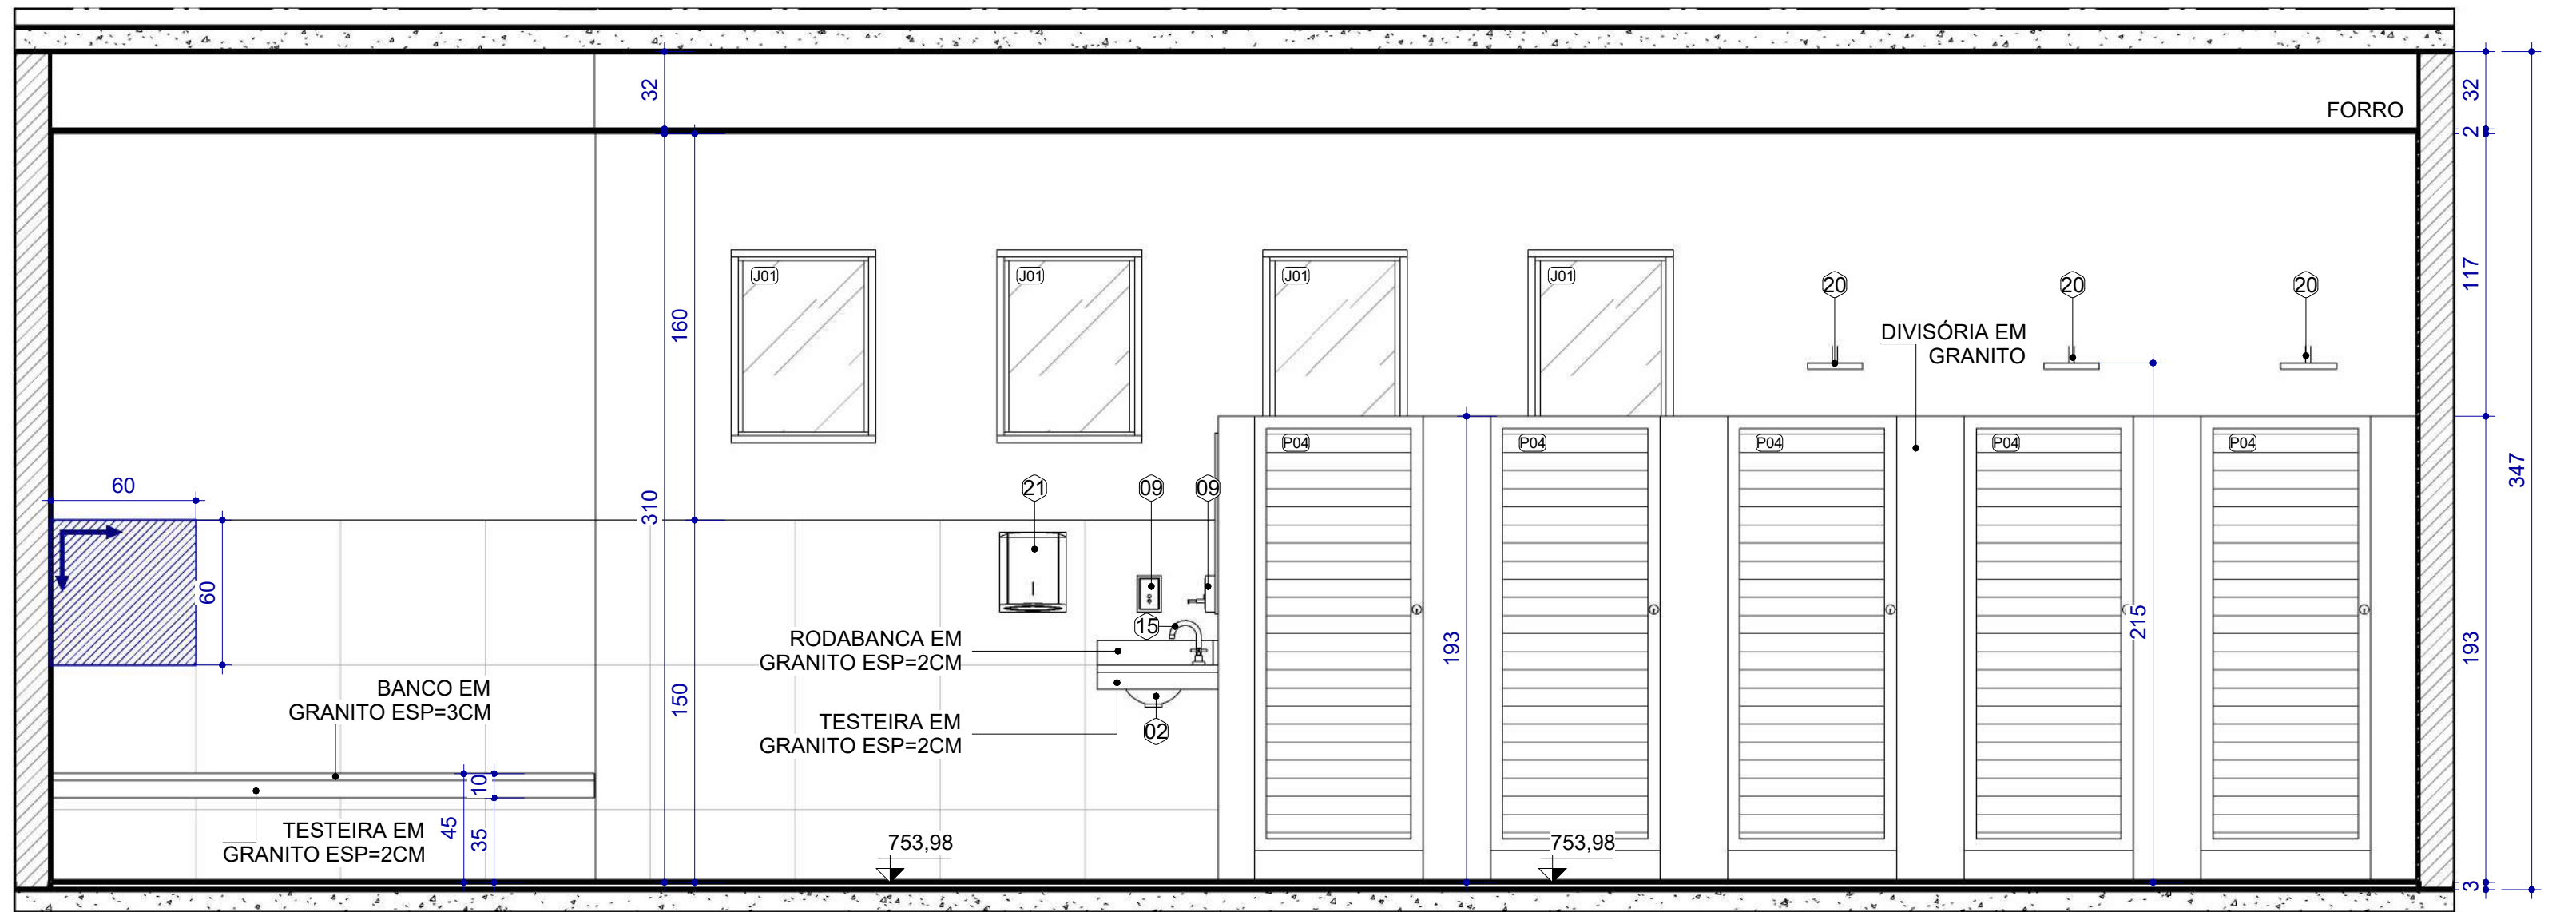


E REFORMA - ELEVAÇÃO A - VESTIÁRIO
ESCALA: 1 : 25

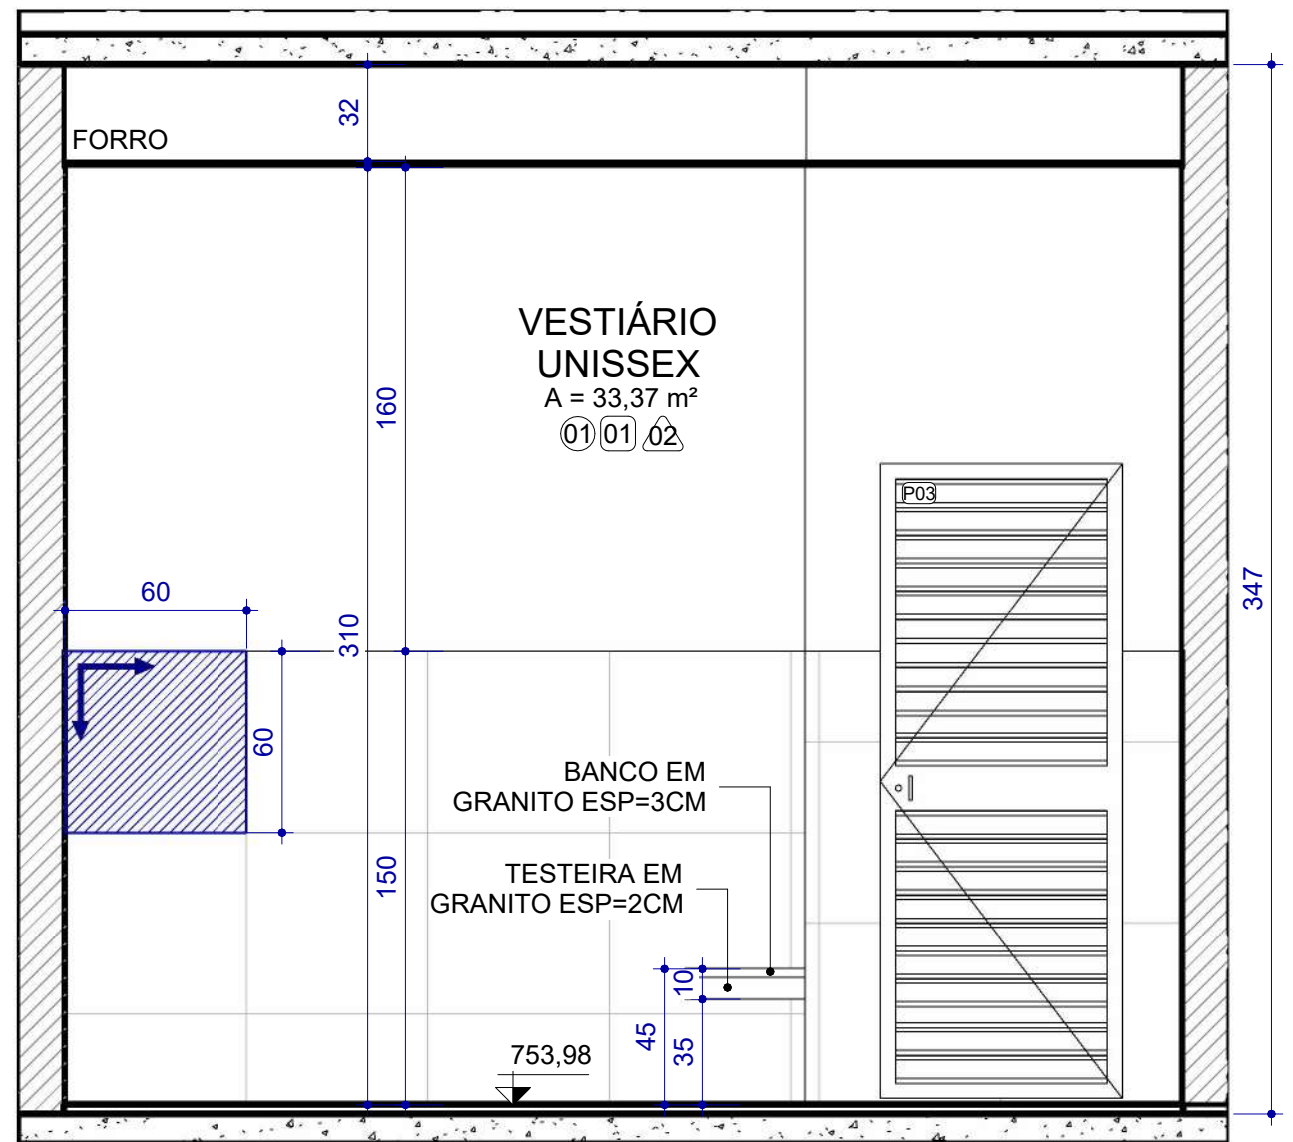


F REFORMA - ELEVAÇÃO D - VESTIÁRIO
ESCALA: 1 : 25

LEGENDA ESPECIFICAÇÕES							
LEGENDA PAGINAÇÃO DE PISO							
	INÍCIO E SENTIDO DA PAGINAÇÃO DE PISO E REVESTIMENTOS						
QUADRO GERAL DE ESPECIFICAÇÕES - ACABAMENTOS							
CÓD.	PISO / SUPERFÍCIES HORIZONTAIS						
01	PISO EM CERÂMICA 60X60CM NA COR BRANCO						
QUADRO GERAL DE ESPECIFICAÇÕES - PAREDE							
CÓD.	VEDAÇÕES / REVESTIMENTOS / ELEMENTOS VERTICAIS						
02	REVESTIMENTO EM CERÂMICA 60X60CM NA COR BRANCO ATÉ 150CM DE ALTURA DO PISO; SEGUIDA DE PINTURA ACRÍLICA NA COR BRANCO NEVE ATÉ O FORRO;						
03	REVESTIMENTO EM CERÂMICA 60X60CM NA COR BRANCO ATÉ O TETO;						
05	REVESTIMENTO EM PINTURA ACRÍLICA, COR BRANCO						
QUADRO GERAL DE ESPECIFICAÇÕES - TETO							
CÓD.	TETOS						
01	FORRO EM GESSO COM PINTURA EM TINTA ACRÍLICA NA COR BRANCO NEVE						
02	PINTURA EM TETO COM TINTA ACRÍLICA NA COR BRANCO NEVE						
QUADRO GERAL DE ESQUADRIAS - JANELAS							
CÓD.	LARGURA	ALTURA	ALTURA PEITORIL	ABERTURA E NÚM. FOLHAS	MATERIAL/ACABAMENTO	QNTD.	
J01	60	80	180	ABRIR, 1 FOLHA	JANELA EM VIDRO LISO, COMUM, INCOLOR, E=6MM, PERFIS DE ALUMÍNIO COR NATURAL	19	
QUADRO GERAL DE ESQUADRIAS - PORTAS							
CÓD.	LARGURA	ALTURA	ABERTURA E NÚM. FOLHAS	MATERIAL/ACABAMENTO		QNTD.	
P03	80	210	ABRIR, 1 FOLHA	PORTA VENEZIANA COM PERFIL EM ALUMÍNIO ANODIZADO NA COR NATURAL		2	
P04	70	180	ABRIR, 1 FOLHA	PORTA VENEZIANA DE ALUMÍNIO		10	
DIVERSOS							
CÓD.	MOBILIÁRIOS / PEÇAS HIDROSSANITÁRIAS / ACESSÓRIOS / DIVERSOS						QNTD.
01	Bacia sanitária convencional						5
02	CUBA DE EMBUTIR OVAL EM LOUÇA BRANCA, 35 X 50CM OU EQUIVALENTE						5
07	VÁLVULA DE DESCARGA						5
08	SABONETEIRA						6
09	SABONETEIRA PLÁSTICA TIPO DISPENSER PARA SABONETE LÍQUIDO COM RESERVATÓRIO DE 800ML						4
10	PAPELEIRA PLÁSTICA TIPO DISPENSER PARA PAPEL HIGIÊNICO ROLÃO						4
15	TORNEIRA CROMADA DE MESA, COM MISTURADOR, 1/2 OU 3/4, PARA LAVATÓRIO						5
20	CHUVEIRO						6
21	DISPENSER EM PLÁSTICO PARA PAPEL TOALHA 2 OU 3 FOLHAS						2
22	TORNEIRA CROMADA 1/2 OU 3/4 PARA TANQUE						1
23	CAIXA D'ÁGUA DE POLIETILENO, 3000 L						1

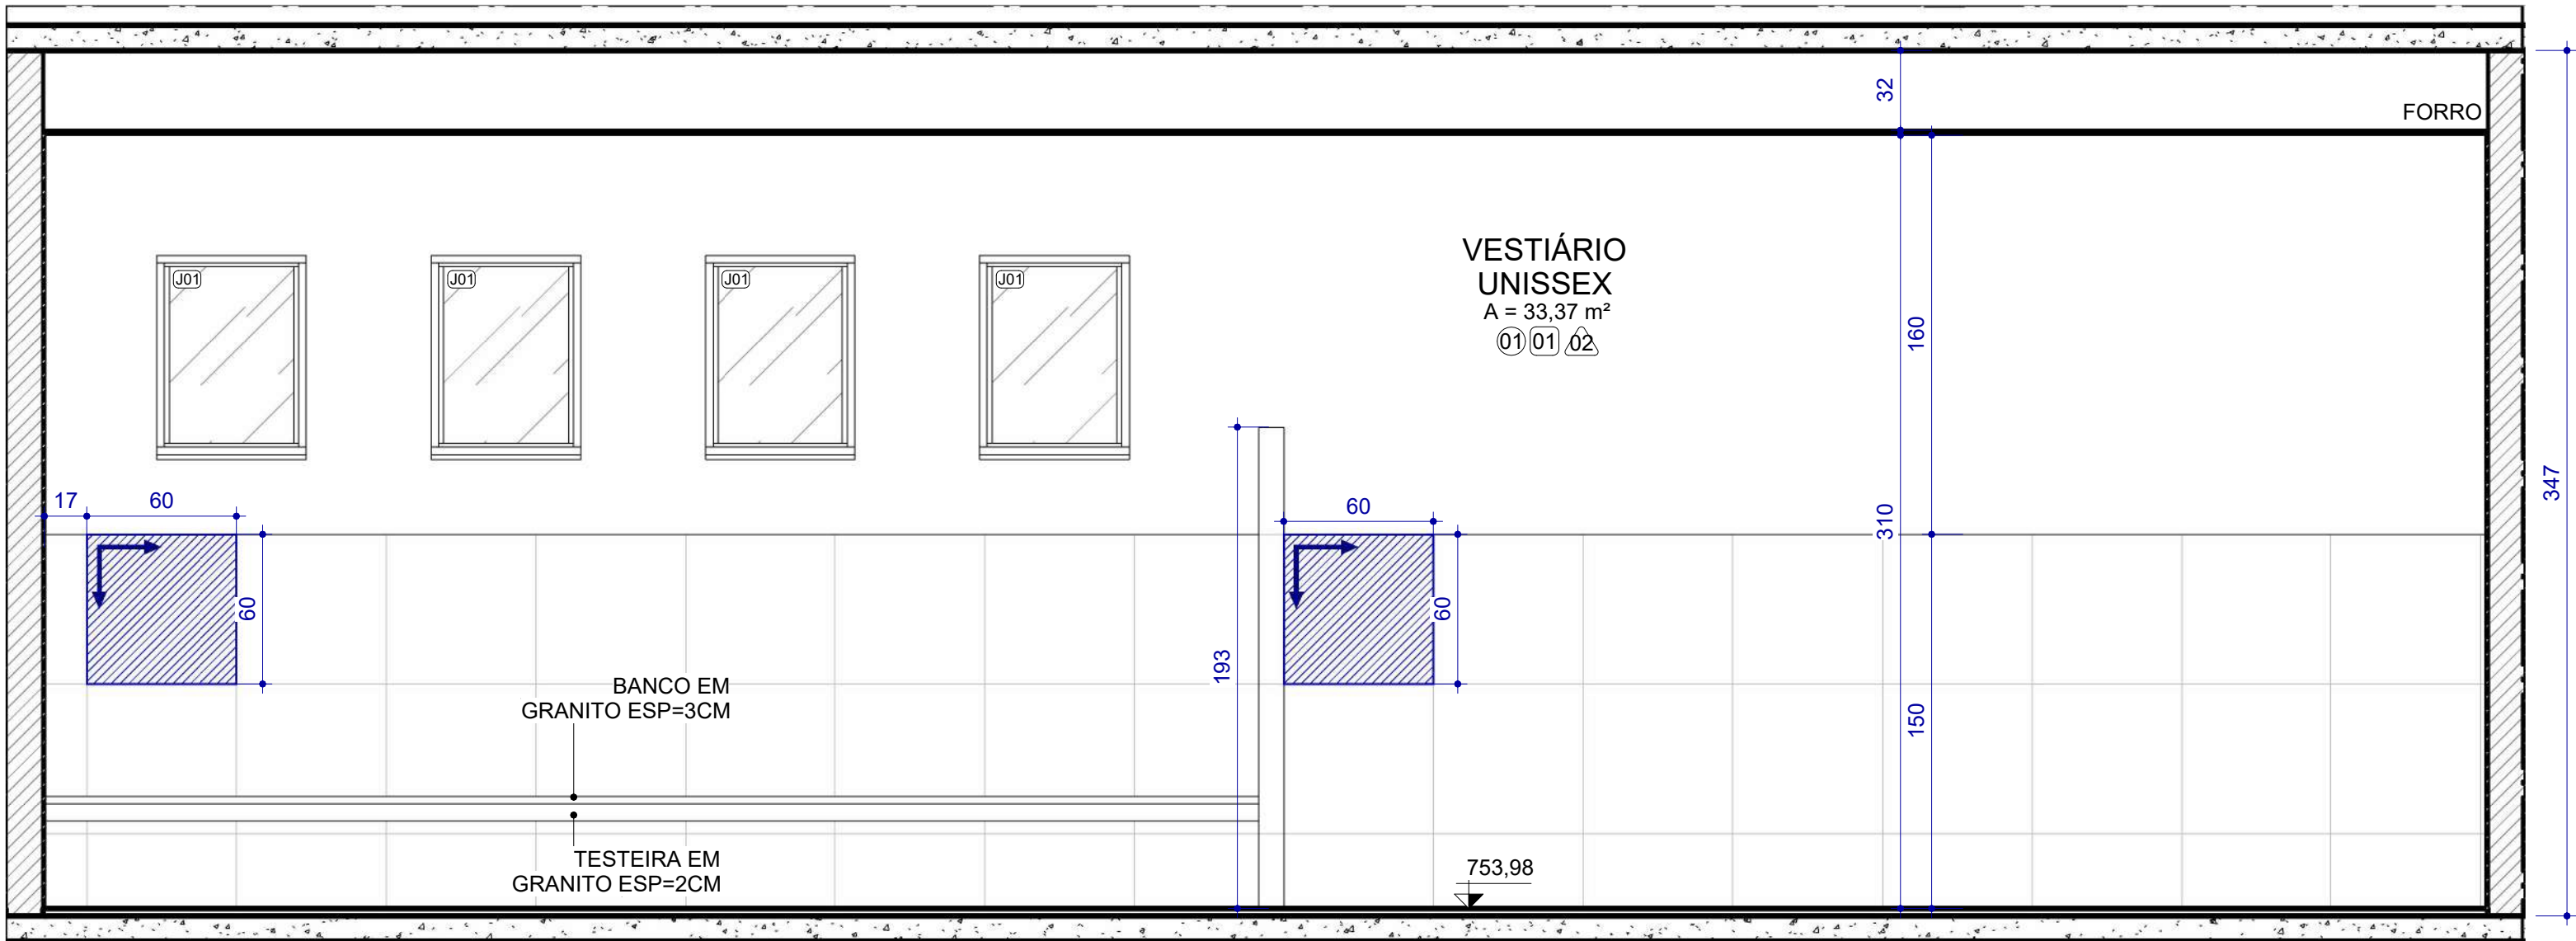


A REFORMA - ELEVAÇÃO C - VESTIÁRIO

ESCALA: 1 : 25

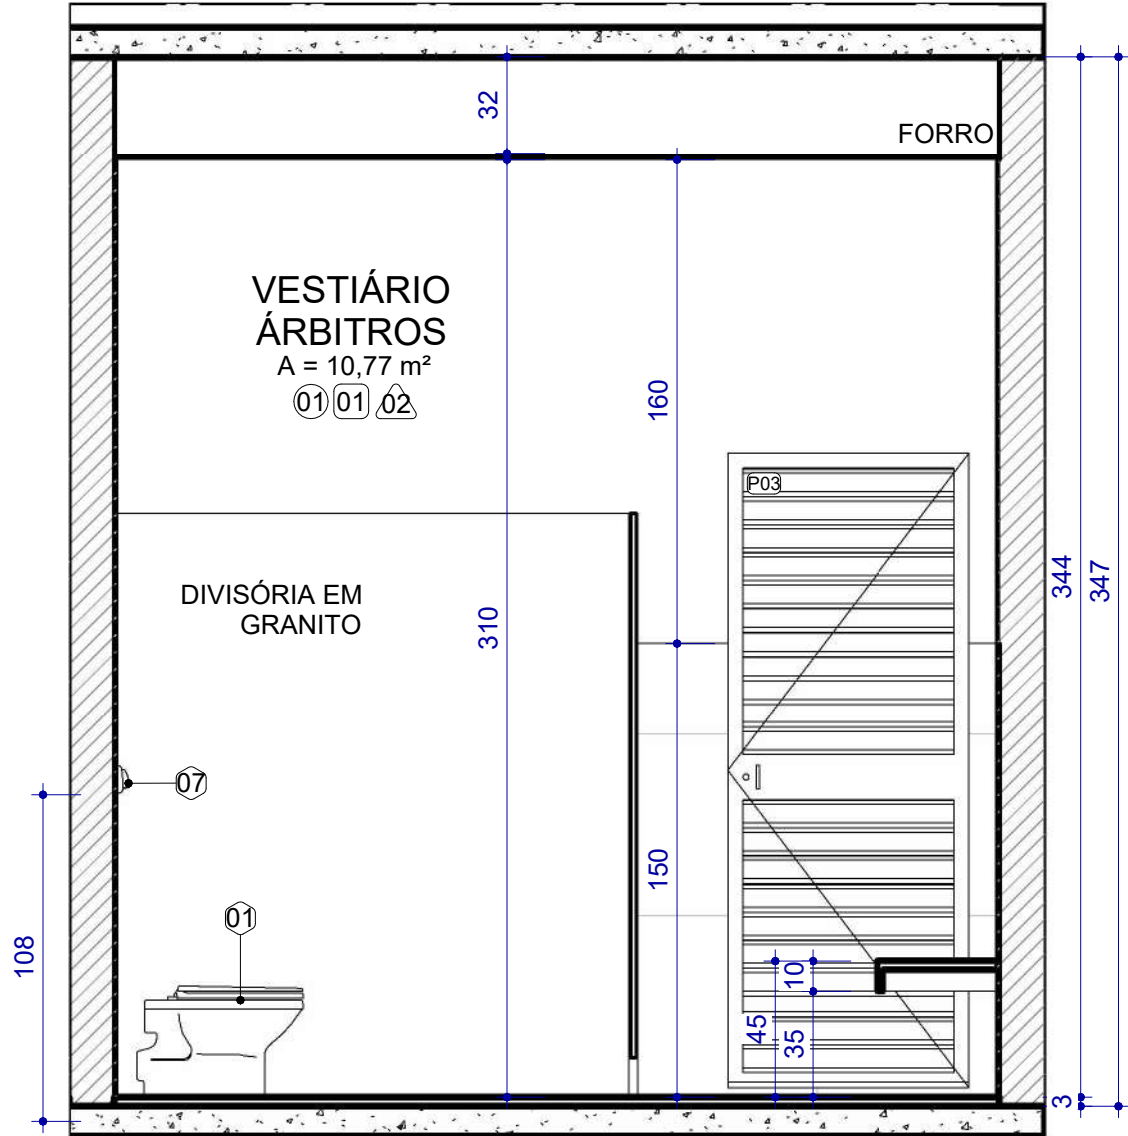


B REFORMA - ELEVAÇÃO A - VESTIÁRIO ÁRBITROS

ESCALA: 1 : 25

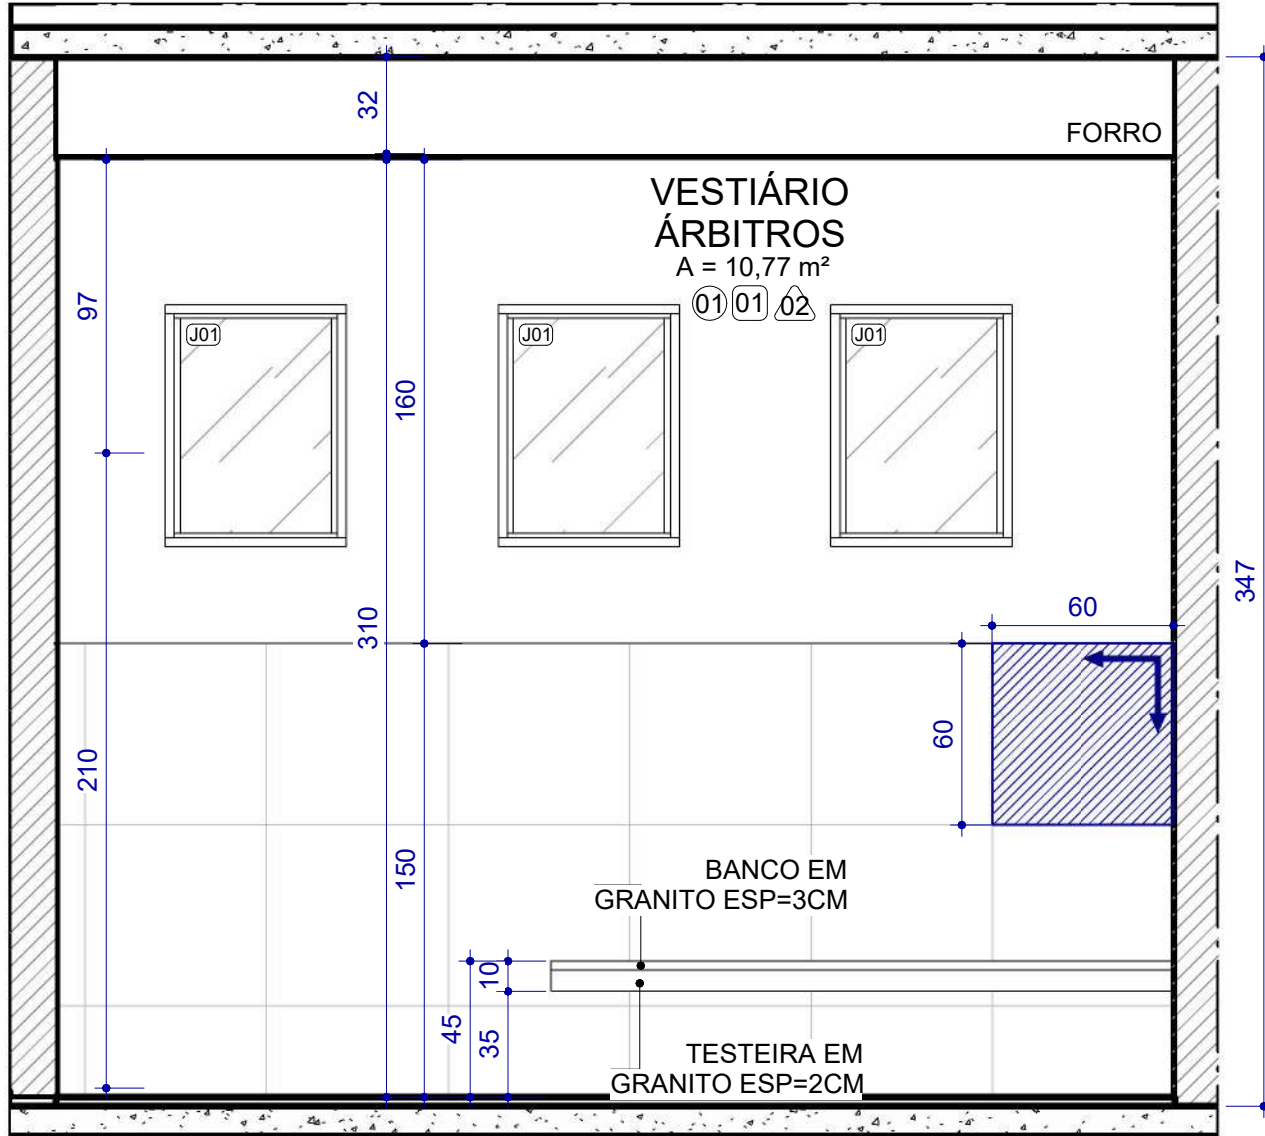


C REFORMA - ELEVAÇÃO B - VESTIÁRIO ÁRBITROS

ESCALA: 1 : 25

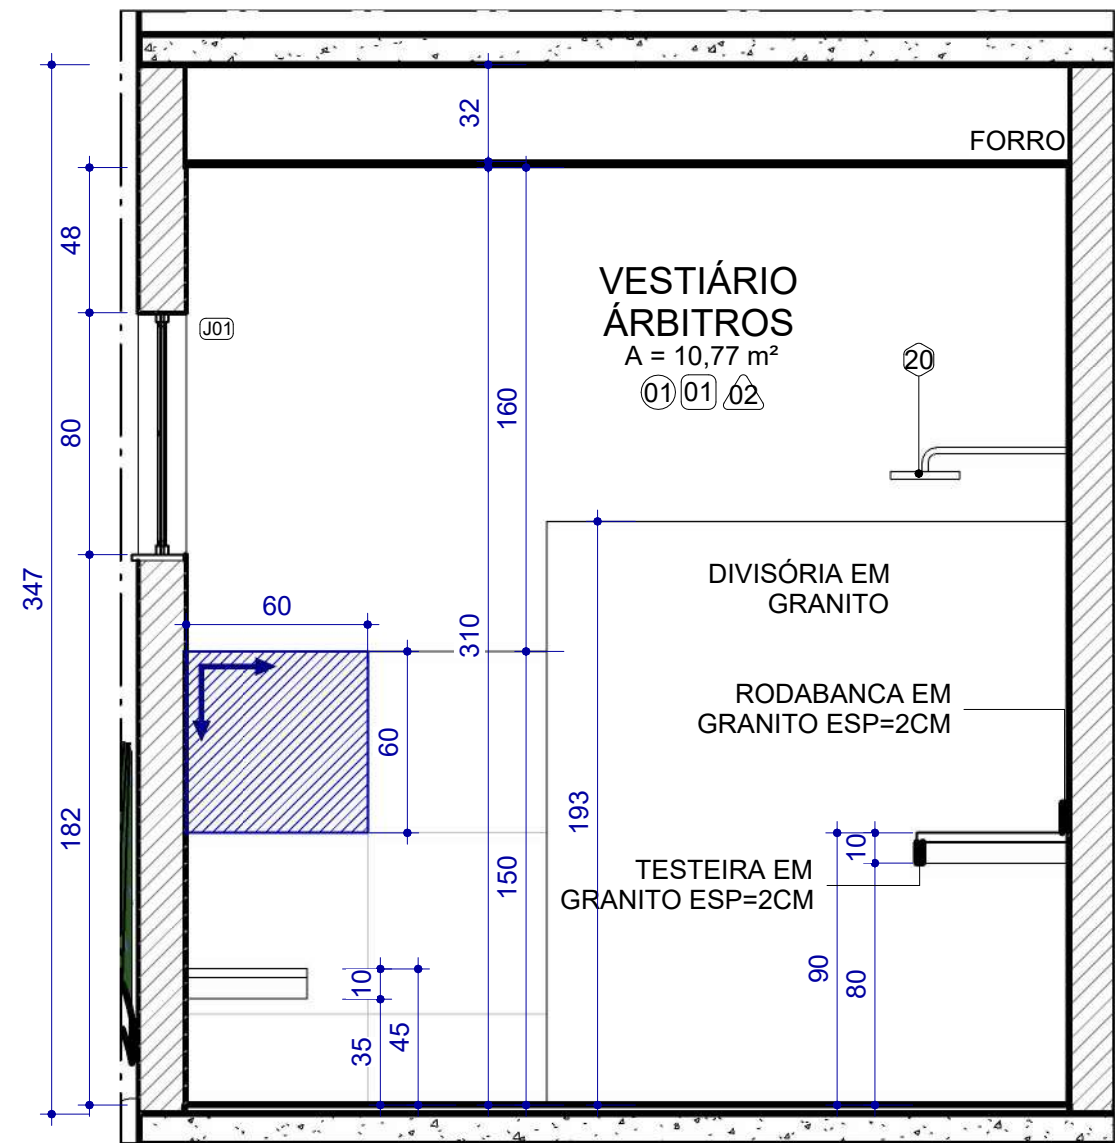

D REFORMA - ELEVAÇÃO C - VESTIÁRIO ÁRBITROS

ESCALA: 1 : 25

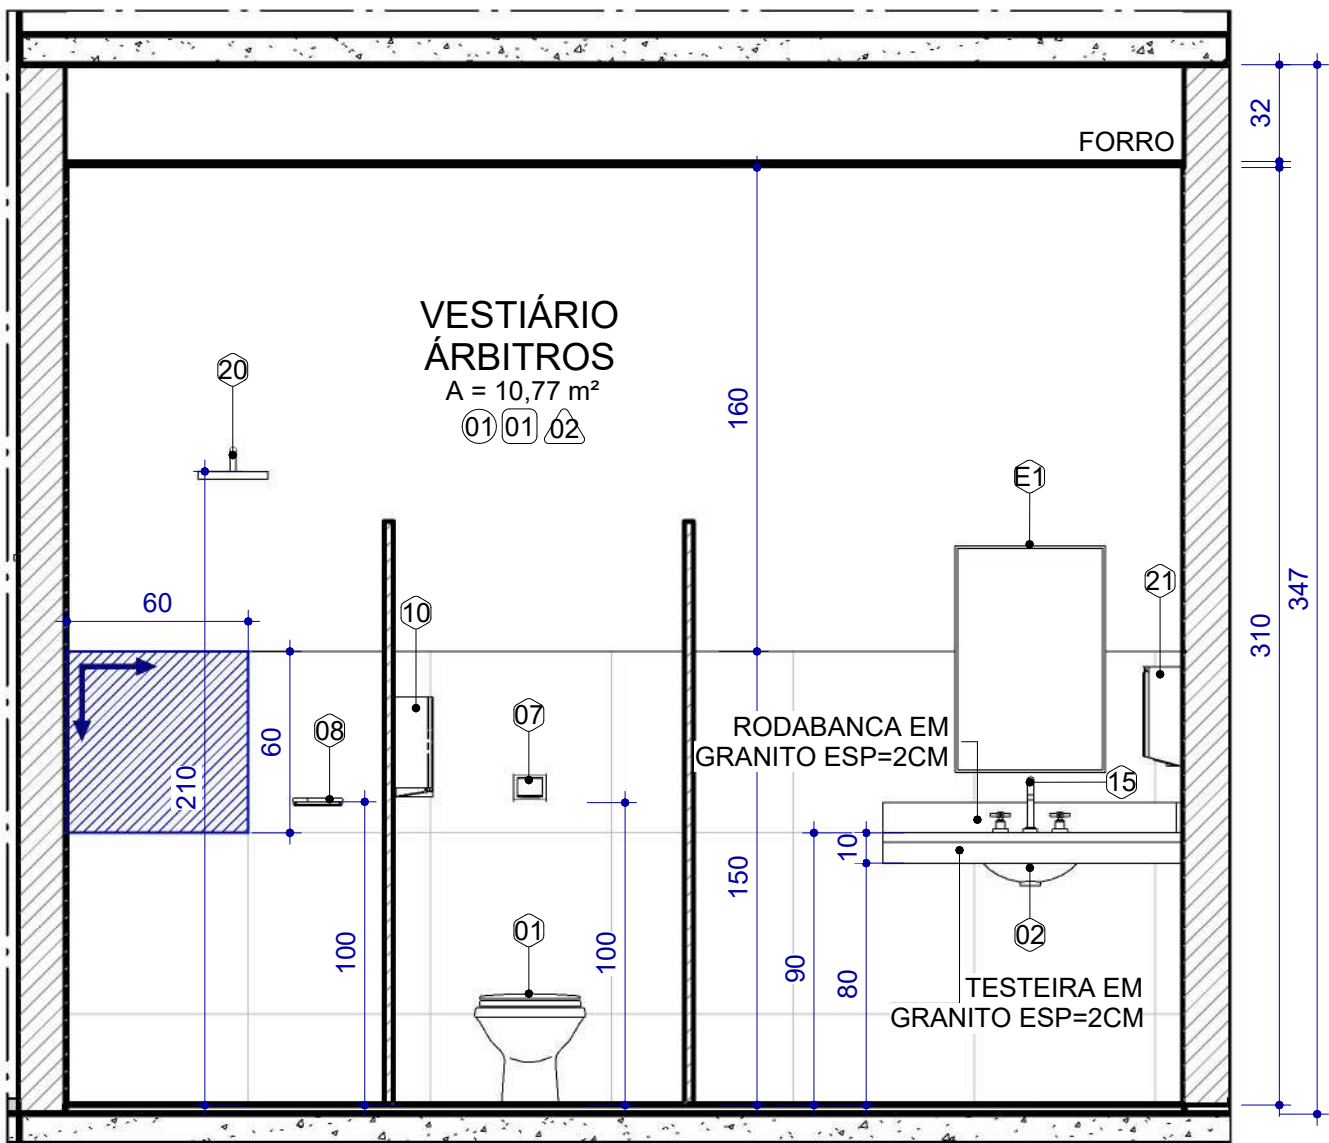

E REFORMA - ELEVAÇÃO D - VESTIÁRIO ÁRBITROS

ESCALA: 1 : 25

LEGENDA ESPECIFICAÇÕES DE PISO						
LEGENDA PAGINAÇÃO DE PISO						
	INÍCIO E SENTIDO DA PAGINAÇÃO DE PISO E REVESTIMENTOS					
QUADRO GERAL DE ESPECIFICAÇÕES - ACABAMENTOS						
CÓD.	PISO / SUPERFÍCIES HORIZONTAIS					
01	PISO EM CERÂMICA 60X60CM NA COR BRANCO					
QUADRO GERAL DE ESPECIFICAÇÕES - PAREDE						
CÓD.	VEDAÇÕES / REVESTIMENTOS / ELEMENTOS VERTICAIS					
02	REVESTIMENTO EM CERÂMICA 60X60CM NA COR BRANCO ATÉ 150CM DE ALTURA DO PISO, SEGUIDA DE PINTURA ACRÍLICA NA COR BRANCO NEVE ATÉ O FORRO					
05	REVESTIMENTO EM PINTURA ACRÍLICA, COR BRANCO					
QUADRO GERAL DE ESPECIFICAÇÕES - TETO						
CÓD.	TETOS					
01	FORRO EM GESSO COM PINTURA EM TINTA ACRÍLICA NA COR BRANCO NEVE					
02	PINTURA EM TETO COM TINTA ACRÍLICA NA COR BRANCO NEVE					
QUADRO GERAL DE ESQUADRIAS - JANELAS						
CÓD.	LARGURA	ALTURA	ALTURA PEITORIL	ABERTURA E NÚM. FOLHAS	MATERIAL/ACABAMENTO	QNTD.
J01	60	80	180	ABRIR, 1 FOLHA	JANELA EM VIDRO LISO, COMUM, INCOLOR, E=6MM, PERFIS DE ALUMÍNIO COR NATURAL	8
QUADRO GERAL DE ESQUADRIAS - PORTAS						
CÓD.	LARGURA	ALTURA	ABERTURA E NÚM. FOLHAS	MATERIAL/ACABAMENTO		QNTD.
P03	80	210	ABRIR, 1 FOLHA	PORTA VENEZIANA COM PERFIL EM ALUMÍNIO ANODIZADO NA COR NATURAL		1
P04	70	180	ABRIR, 1 FOLHA	PORTA VENEZIANA DE ALUMÍNIO		6
DIVERSOS						
CÓD.	MOBILIÁRIOS / PEÇAS HIDROSSANITÁRIAS / ACESSÓRIOS / DIVERSOS					QNTD.
01	Bacia sanitária convencional					2
02	CUBA DE EMBUTIR OVAL EM LOUÇA BRANCA, 35 X 50CM OU EQUIVALENTE					1
07	VÁLVULA DE DESCARGA					1
08	SABONETEIRA					4
09	SABONETEIRA PLÁSTICA TIPO DISPENSER PARA SABONETE LIQUIDO COM RESERVATÓRIO DE 800ML					1
10	PAPELEIRA PLÁSTICA TIPO DISPENSER PARA PAPEL HIGIÊNICO ROLÃO					2
15	TORNEIRA CROMADA DE MESA, COM MISTURADOR, 1/2 OU 3/4, PARA LAVATÓRIO					1
20	CHUVEIRO					4
21	DISPENSER EM PLÁSTICO PARA PAPEL TOALHA 2 OU 3 FOLHAS					1
23	CAIXA D'ÁGUA DE POLIETILENO, 3000 L					1